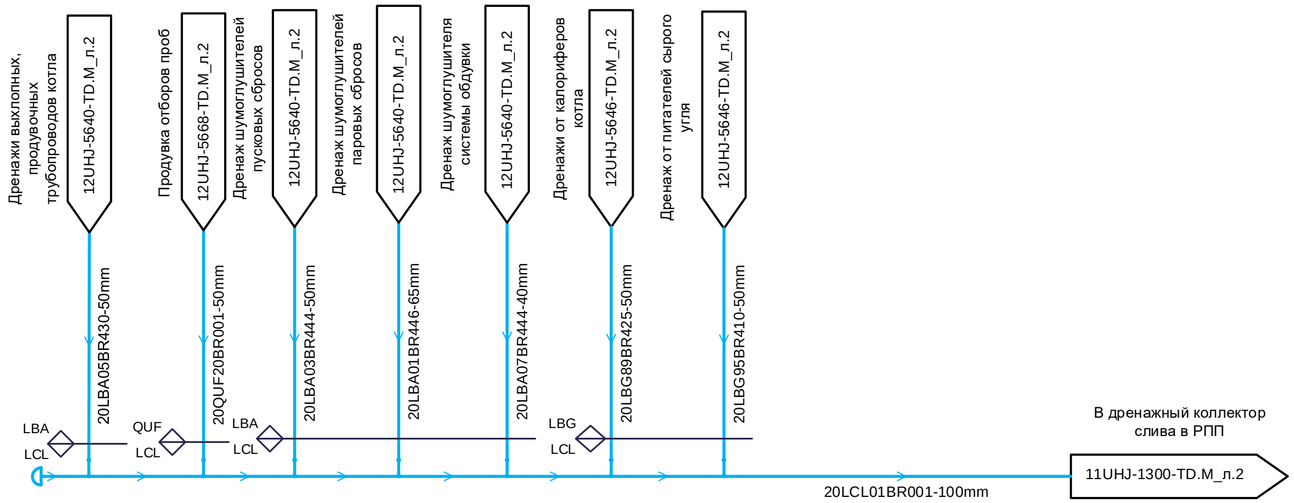

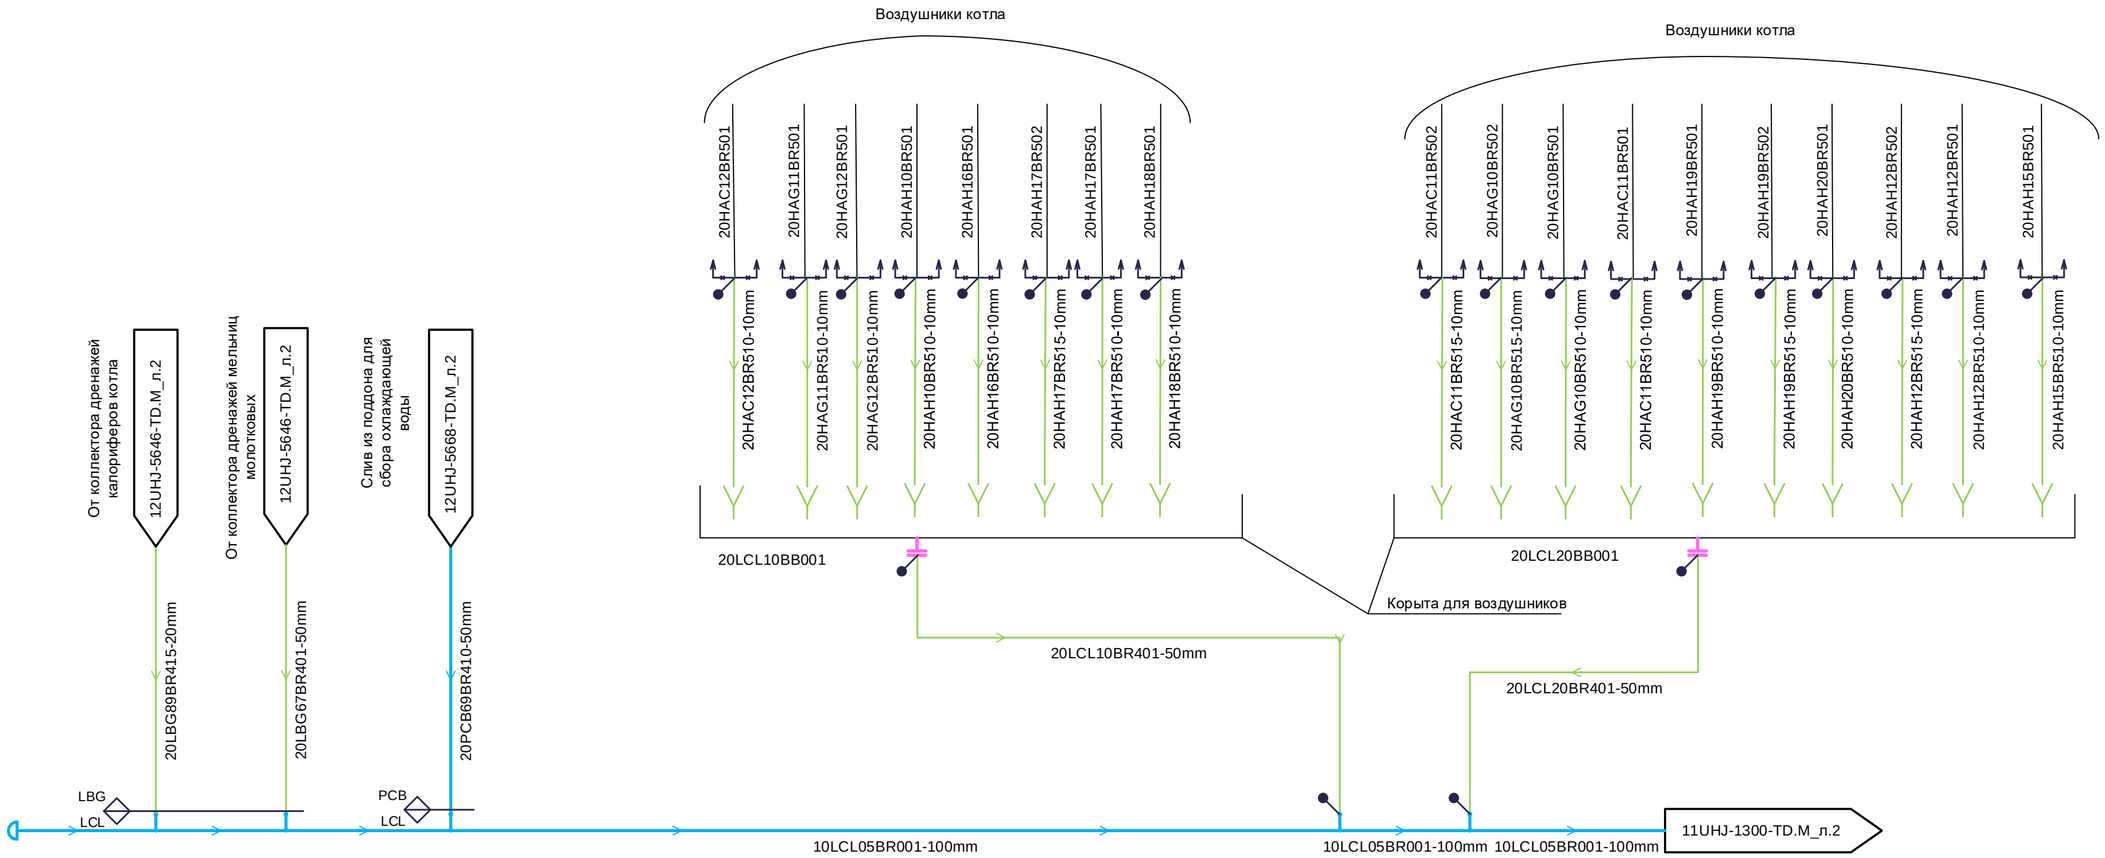

						132N32-12UHJ-5706-TD.M
1						Строительство Сахалинской ГРЭС-2. Основной производственный комплекс. Внутриплощадочные объекты (1очередь)
Изм.	Кол.уч	Лист	№ док.	Подп.	Дата	
Разработал		Федорцова				Главный корпус. Блок №2. PI-диаграмма дренажей, воздушников и вспомогательных трубопроводов котла
Проверил		Калинкина				Стадия: Р; Лист: 2; Листов:
Нач.гр.		Бобров				
Гл.спец.		Бакатин				PI-диаграмма дренажей, воздушников и вспомогательных трубопроводов котла. Система LCQ, LCL
Н. контр.		Гридчина				АКЦИОНЕРНОЕ ОБЩЕСТВО ИНСТИТУТ ТЕПЛОЭЛЕКТРОПРОЕКТ г. МОСКВА

Согласовано

ОАСУ Соболева

Взам. инв. №

Подпись и дата

Инв. № подл.

Формат А1