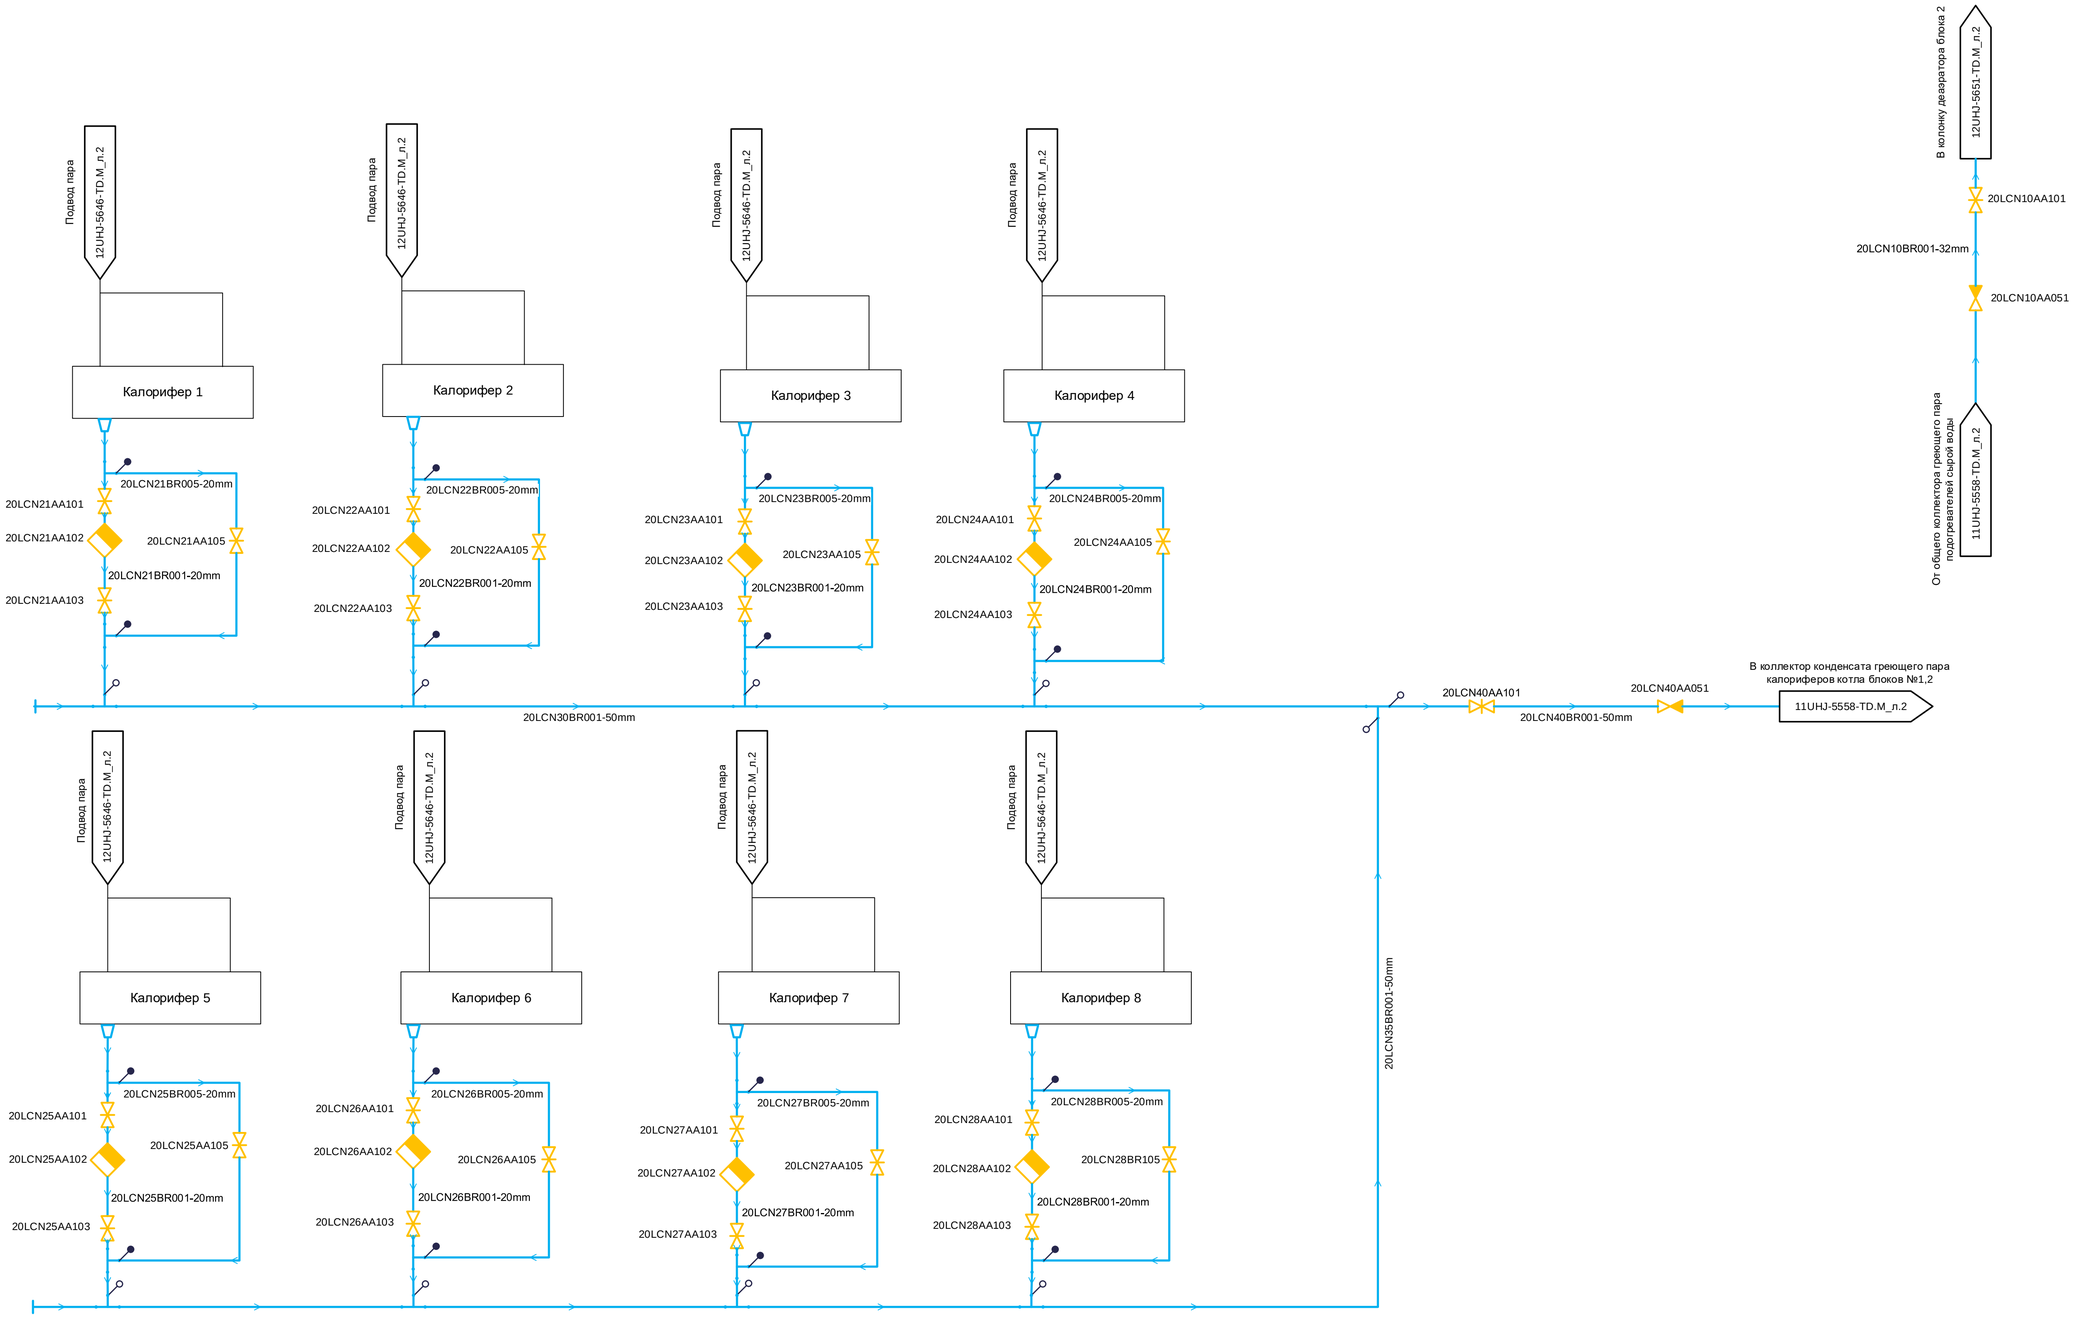

Изм.	Кол.уч	Лист	№ док.	Подп.	Дата	132N32 – 12UHJ – 5708 – TD.M
						Строительство сахалинской ГРЭС-2. Основной производственный комплекс. Внутриплощадочные объекты (1 очередь)
Разработал		Тян				Главный корпус. Блок №2. PI-диаграмма трубопроводов конденсата греющего пара подогревателей сырой воды и калориферов котла
Проверил		Калинкина				
Нач. гр.		Бобров				
Гл. спец.		Бакатин				PI-диаграмма трубопроводов конденсата греющего пара подогревателей сырой воды и калориферов котла. Система LCN
Н. контр.		Гридчина				

Стадия	Лист	Листов
Р	2	

АКЦИОНЕРНОЕ ОБЩЕСТВО «ВНИИПИЭТ» ТЕПЛОЭЛЕКТРОПРОЕКТ г. МОСКВА

Согласовано

ОАСУ	Соболева

Взам. инв. №

Подпись и дата

Инв. № подл.

Формат А1