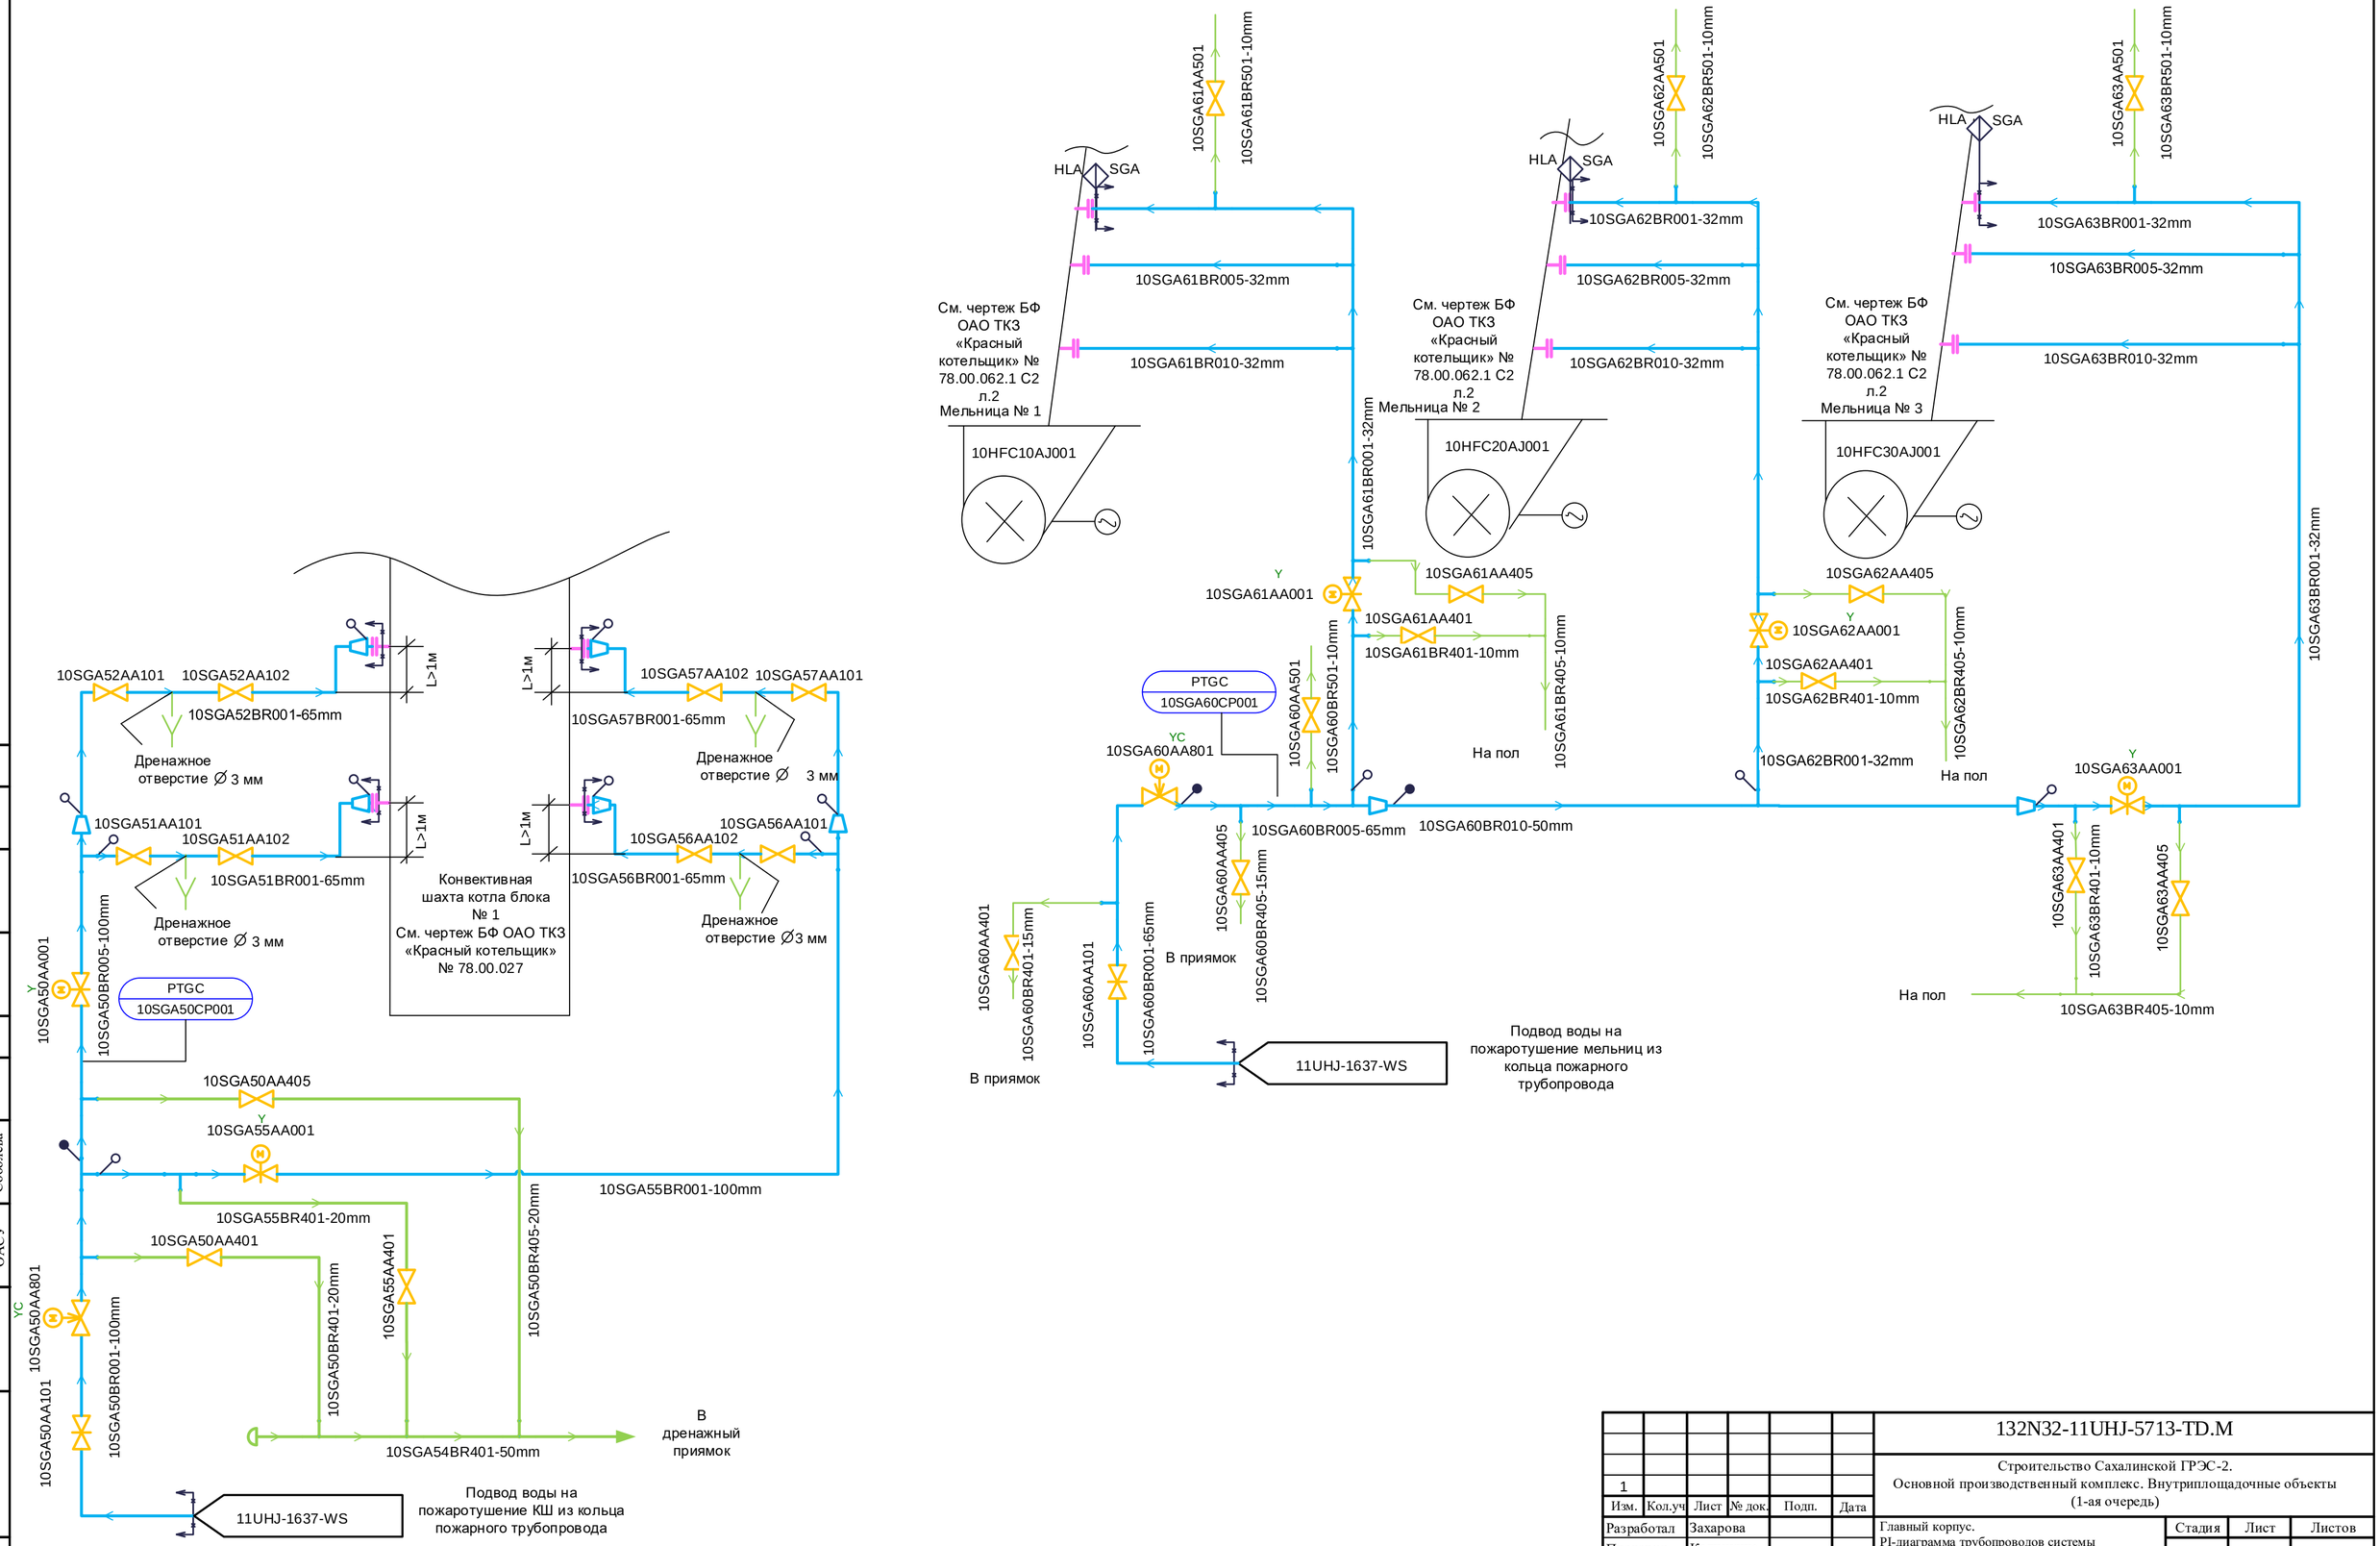

						132N32-11UHJ-5713-TD.M		
						Строительство Сахалинской ГРЭС-2. Основной производственный комплекс. Внутриплощадочные объекты (1-ая очередь)		
1								
Изм.	Кол.уч	Лист	№ док.	Подп.	Дата			
Разработал		Захарова				Главный корпус. PI-диаграмма трубопроводов системы пожаротушения конвективных шахт и мельниц котла	Стадия	Лист	Листов
Проверил		Калинкина					Р	2	
Гл.спец.		Бакатин							
						PI-диаграмма трубопроводов системы пожаротушения конвективных шахт и мельниц котла. Система SGA	АКЦИОНЕРНОЕ ОБЩЕСТВО ИНСТИТУТ ТЕПЛОЭЛЕКТРОПРОЕКТ Г. МОСКВА		
Н. контр.		Гридчина							

Согласовано

Соболева

ОАСУ

Взам. инв. №

Подпись и дата

Инв. № подл.

Формат А2