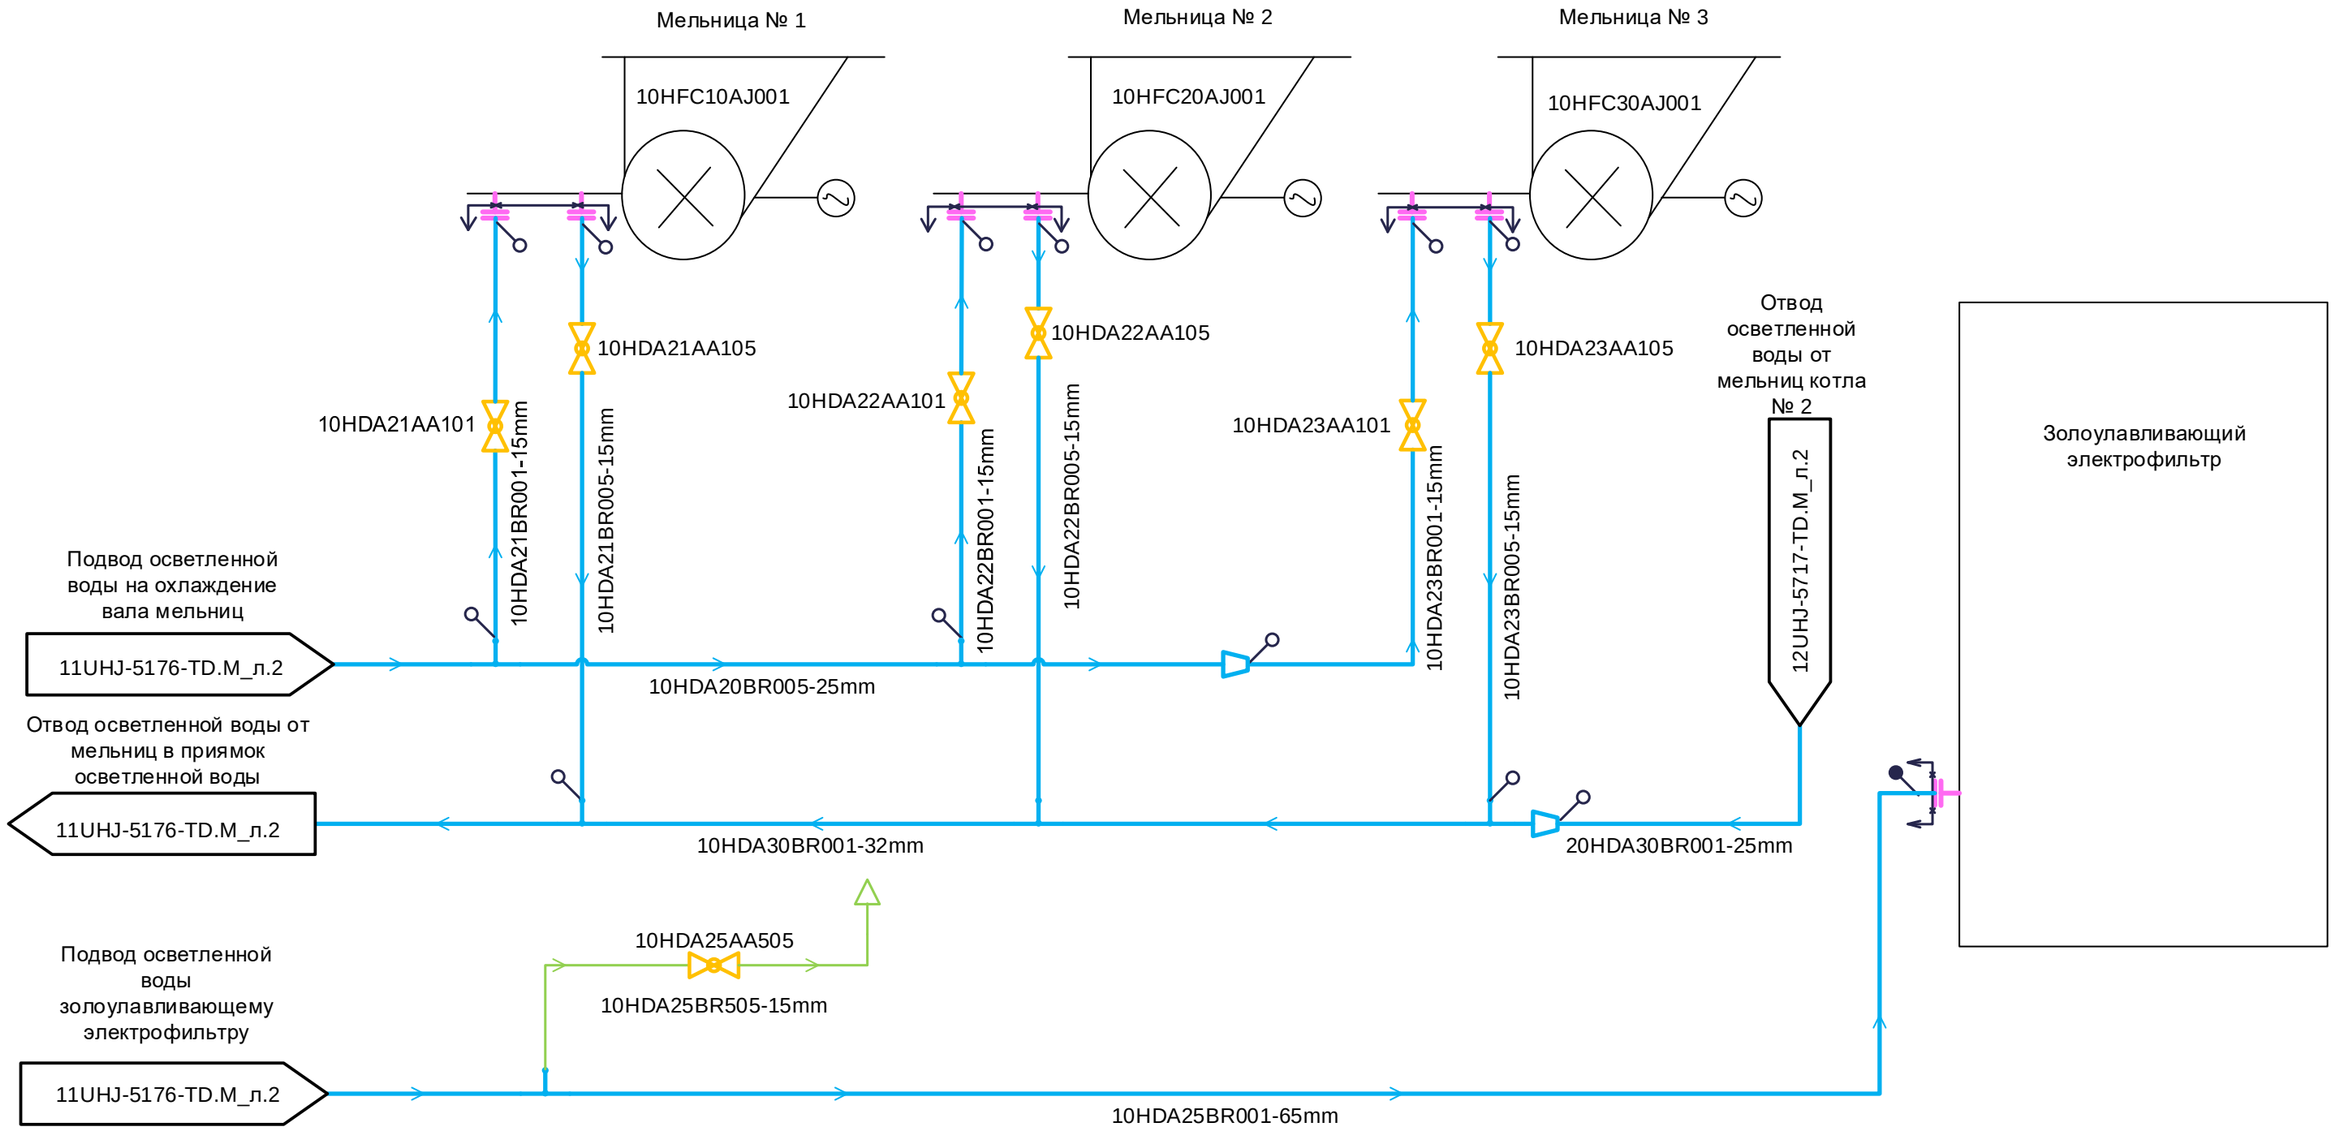

Согласовано

Соболева

ОАСУ

Взам. инв. №

Подпись и дата

Инв. № подл.

Изм.	Кол.уч	Лист	№ док.	Подп.	Дата
Разработал		Захарова			
Проверил		Калинкина			
Гл. спец.		Бакатин			
Н. контр.		Гридчина			

132N32-11UHJ-5714-TD.M

Строительство Сахалинской ГРЭС-2.
Основной производственный комплекс. Внутриплощадочные объекты
(1-ая очередь)

Главный корпус.
PI-диаграмма трубопроводов охлаждающей воды валов мельниц и электрофильтров

Стадия	Лист	Листов
Р	2	

PI-диаграмма трубопроводов охлаждающей воды валов мельниц и электрофильтров. Система HDA

АКЦИОНЕРНОЕ ОБЩЕСТВО ИНСТИТУТ ТЕПЛОЭЛЕКТРОПРОЕКТ Г. МОСКВА

Формат А3