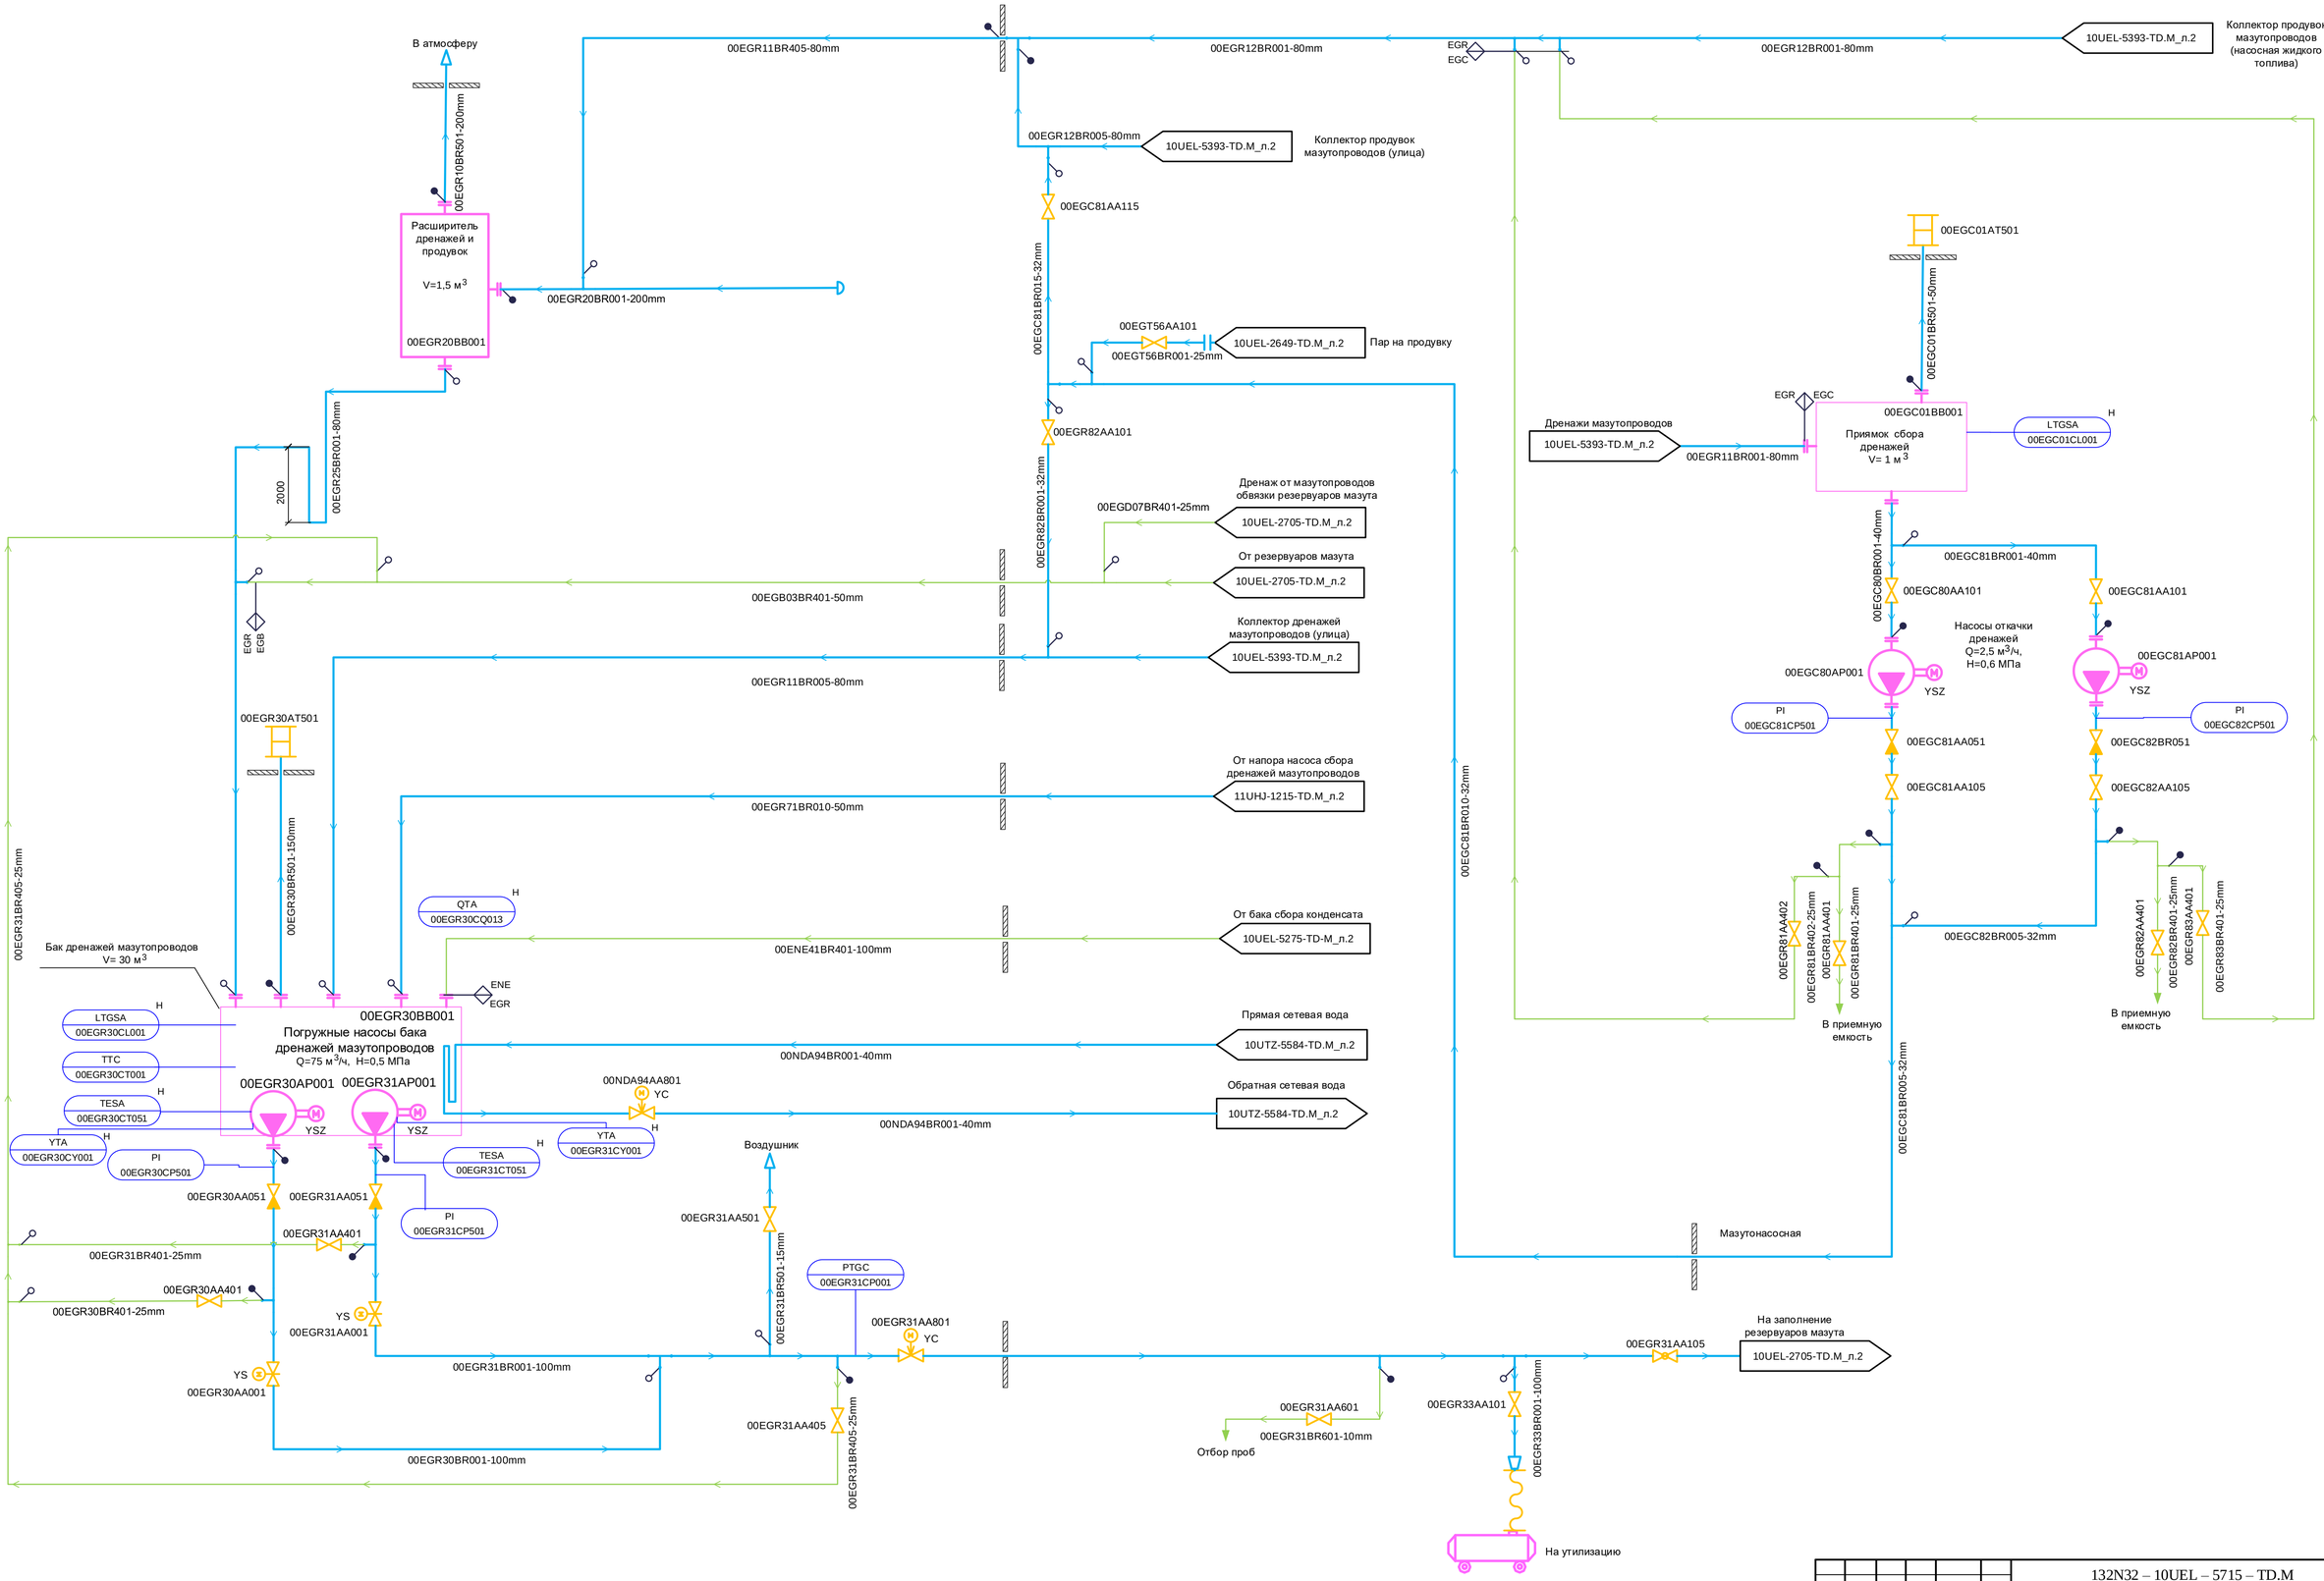

1	-	Зам	74-17			
Изм.	Кол.уч	Лист	№ док.	Подп.	Дата	

132N32 – 10UEL – 5715 – TD.M

Строительство Сахалинской ГРЭС-2. Основной производственный комплекс.
Внутриплощадочные объекты (1-ая очередь)

Разработал	Полянская	
Проверил	Бобров	
Гл.спец.	Егоров	
Н. контр.	Гридчина	

Насосная жидкого топлива.
PI-диаграмма тубопроводов дренажей и продувок мазутопроводов и оборудования

PI-Диаграмма трубопроводов дренажей и продувок мазутопроводов и оборудования. Система EGR

Стадия	Лист	Листов
Р	2	

ОТКРЫТОЕ АКЦИОНЕРНОЕ ОБЩЕСТВО ИНСТИТУТ ТЕПЛОЭЛЕКТРОПРОЕКТ МОСКВА

Согласовано

Взам. инв. №

Подпись и дата

Инв. № подл.

Формат А1