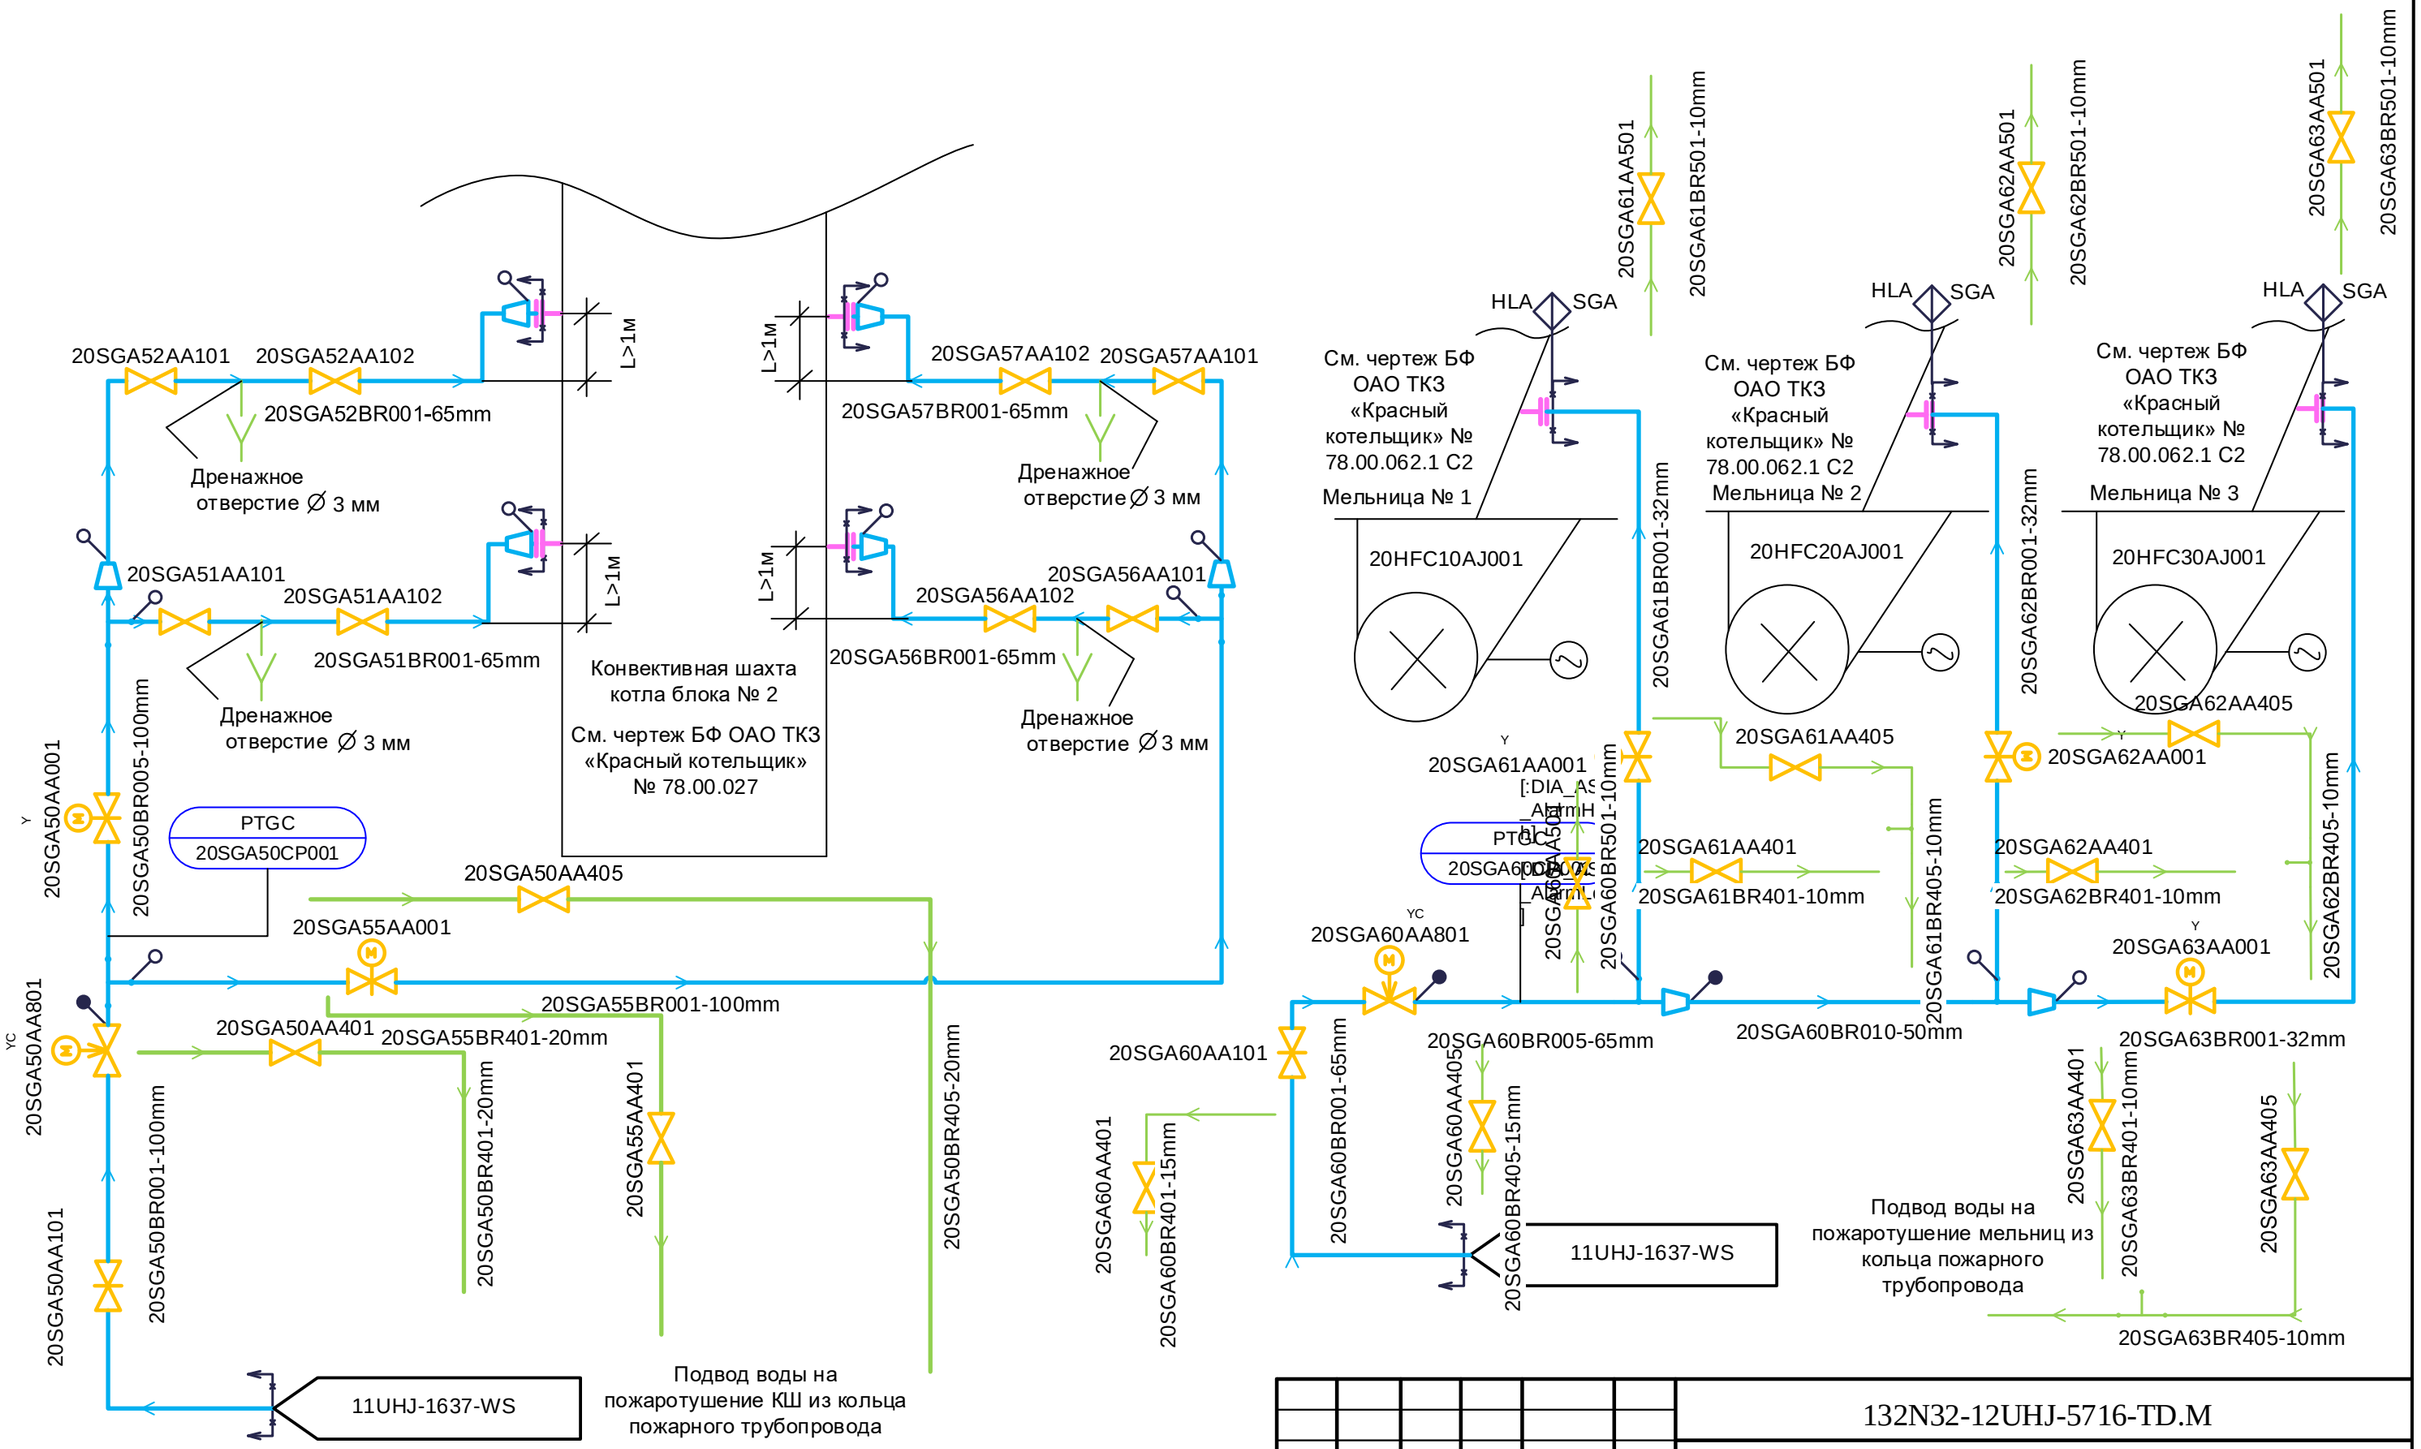

Изм.	Кол.уч	Лист	№ док.	Подп.	Дата
Разработал		Захарова			
Проверил		Калинкина			
Гл.спец.		Бакатин			
Н. контр.		Гридчина			

132N32-12UHJ-5716-TD.M

Строительство Сахалинской ГРЭС-2.
Основной производственный комплекс. Внутриплощадочные объекты (1-ая очередь)

Главный корпус.Блок№ 2
PI-диаграмма трубопроводов системы пожаротушения конвективных шахт и мельниц котла

Стадия	Лист	Листов
Р	2	

PI-диаграмма трубопроводов системы пожаротушения конвективных шахт и мельниц котла. Система SGA

АКЦИОНЕРНОЕ ОБЩЕСТВО ИНСТИТУТ ТЕПЛОЭЛЕКТРОПРОЕКТ Г. МОСКВА

Согласовано
Соболева
ОАСУ
Взам. инв. №
Подпись и дата
Инв. № подл.

Формат А3