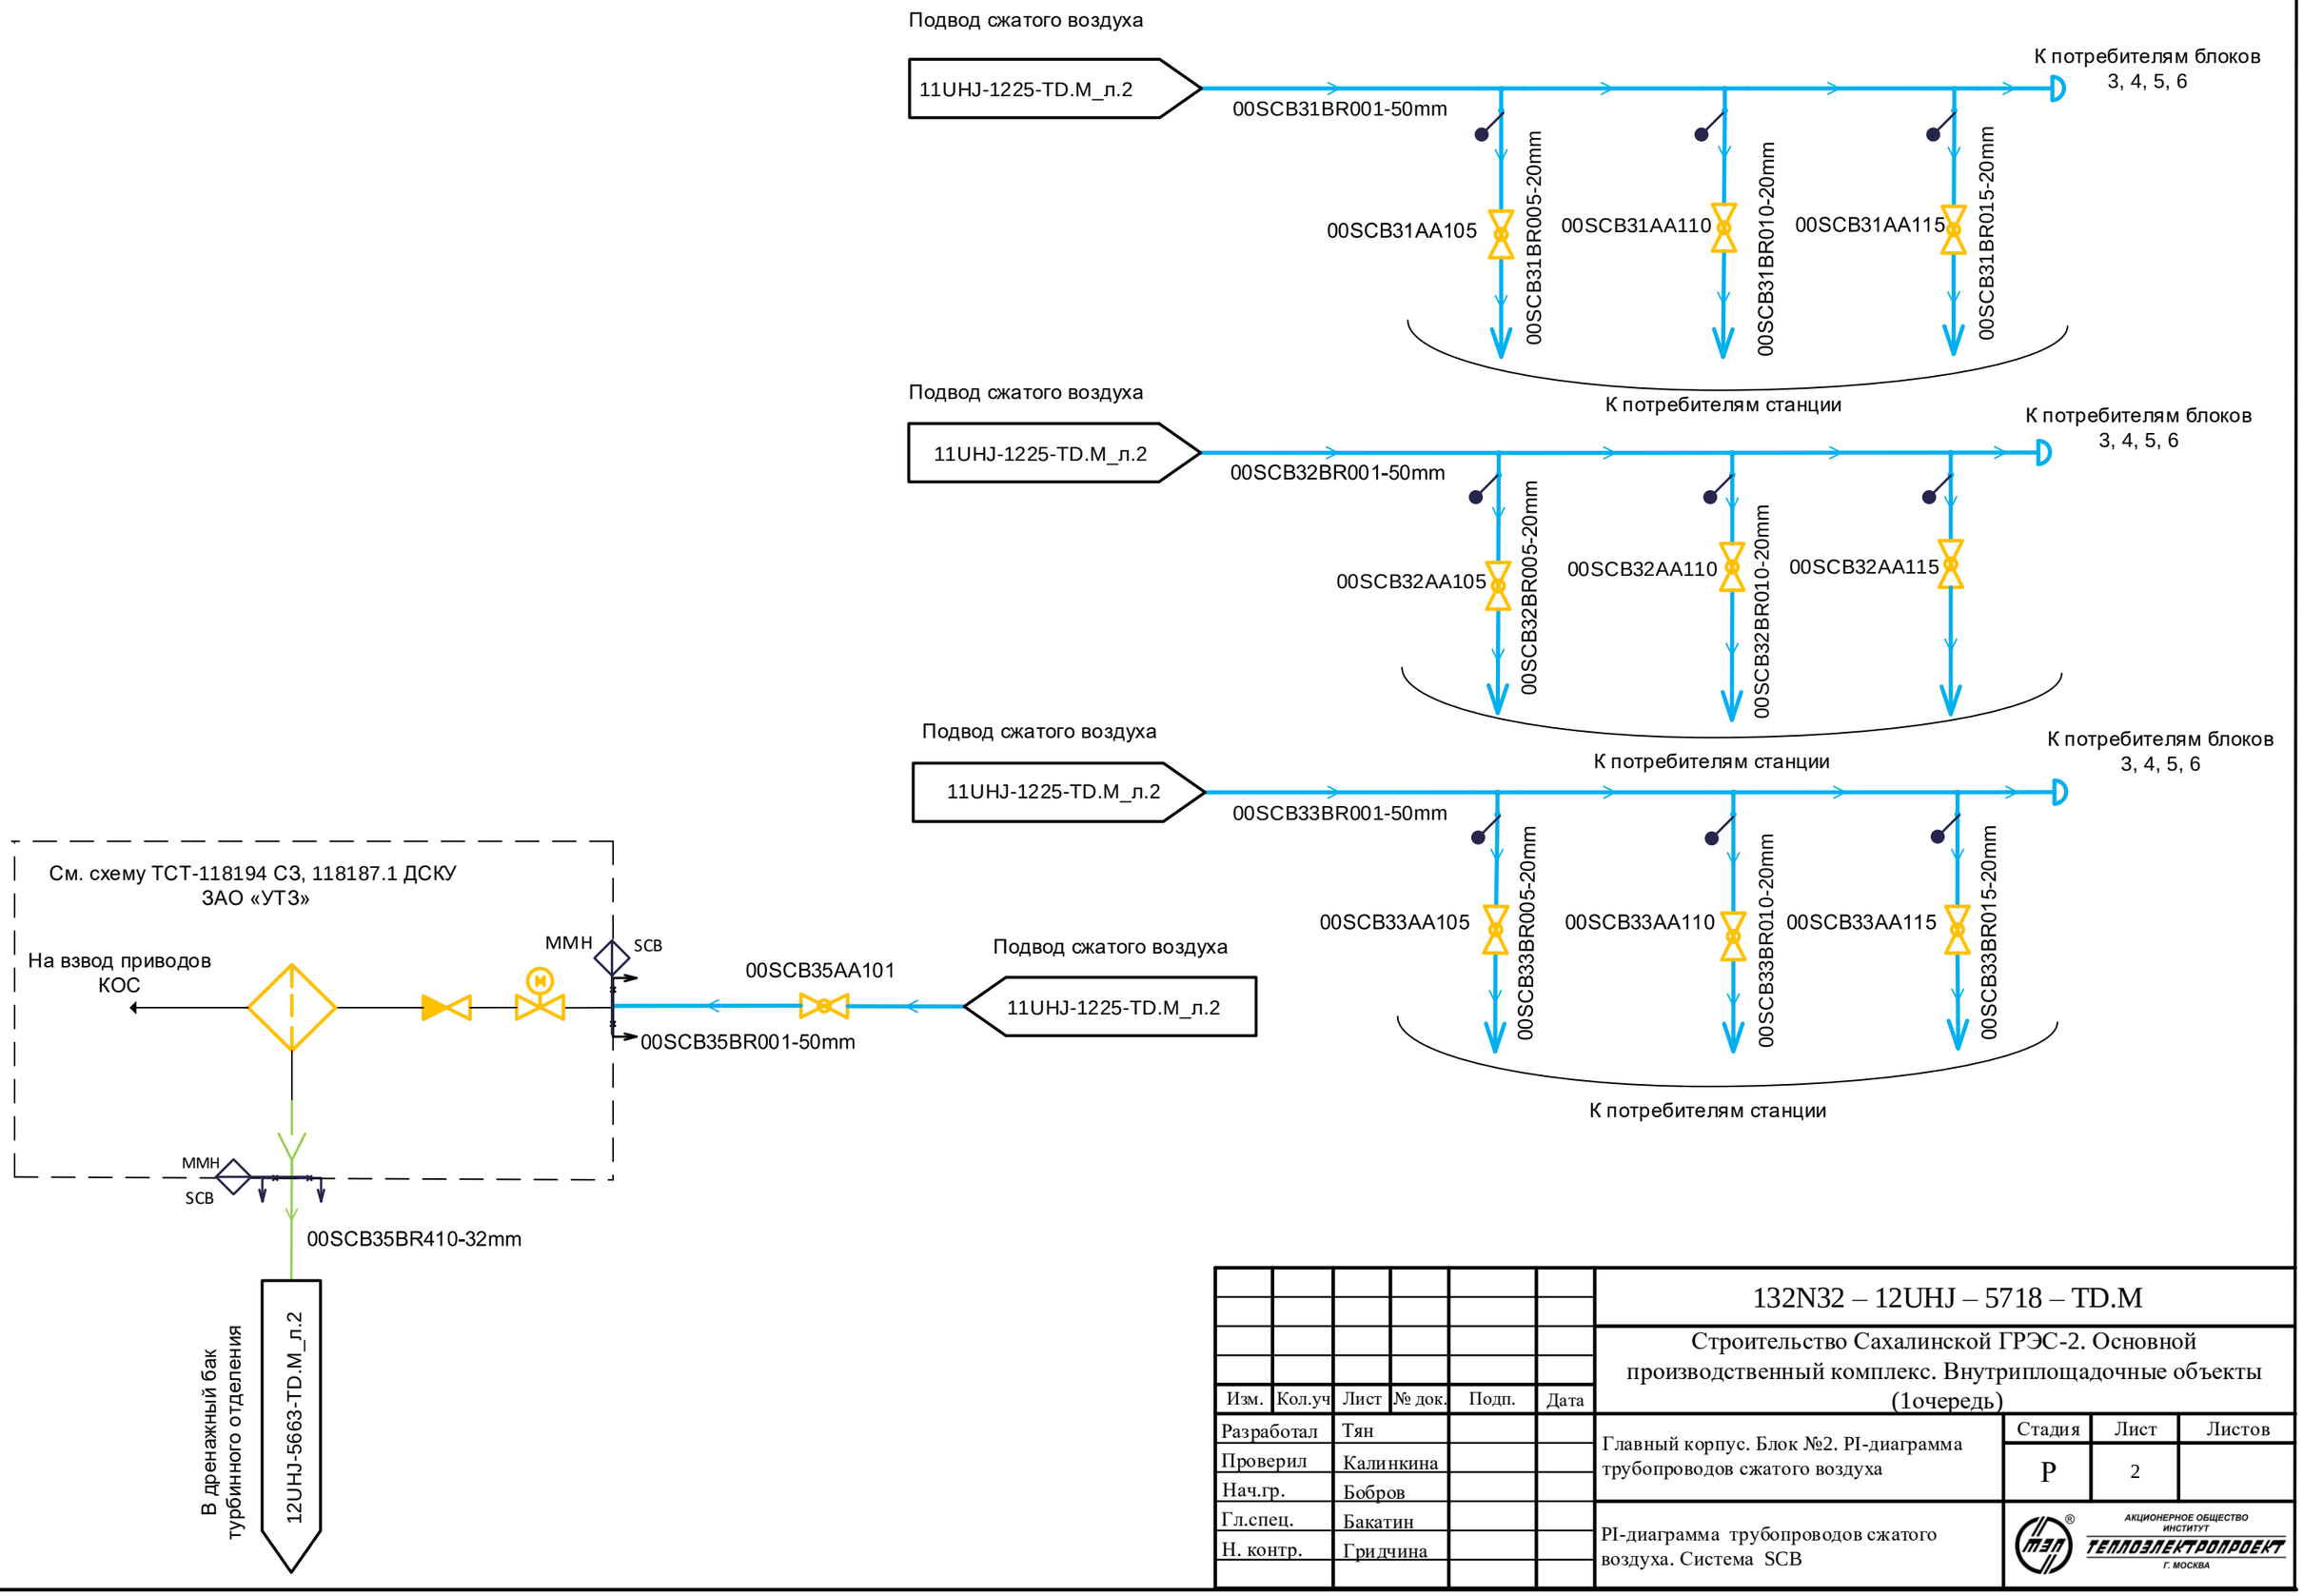

Согласовано

Соболева

ОАСУ

Взам. инв. №

Подпись и дата

Инв. № подл.

Изм.	Кол.уч	Лист	№ док.	Подп.	Дата
Разработал		Тян			
Проверил		Калинкина			
Нач.гр.		Бобров			
Гл.спец.		Бакатин			
Н. контр.		Гридчина			

132N32 – 12UHJ – 5718 – TD.M

Строительство Сахалинской ГРЭС-2. Основной производственный комплекс. Внутриплощадочные объекты (1очередь)

Главный корпус. Блок №2. PI-диаграмма трубопроводов сжатого воздуха

Стадия	Лист	Листов
Р	2	

PI-диаграмма трубопроводов сжатого воздуха. Система SCB

АКЦИОНЕРНОЕ ОБЩЕСТВО ИНСТИТУТ ТЕПЛОЭЛЕКТРОПРОЕКТ Г. МОСКВА

Формат А3