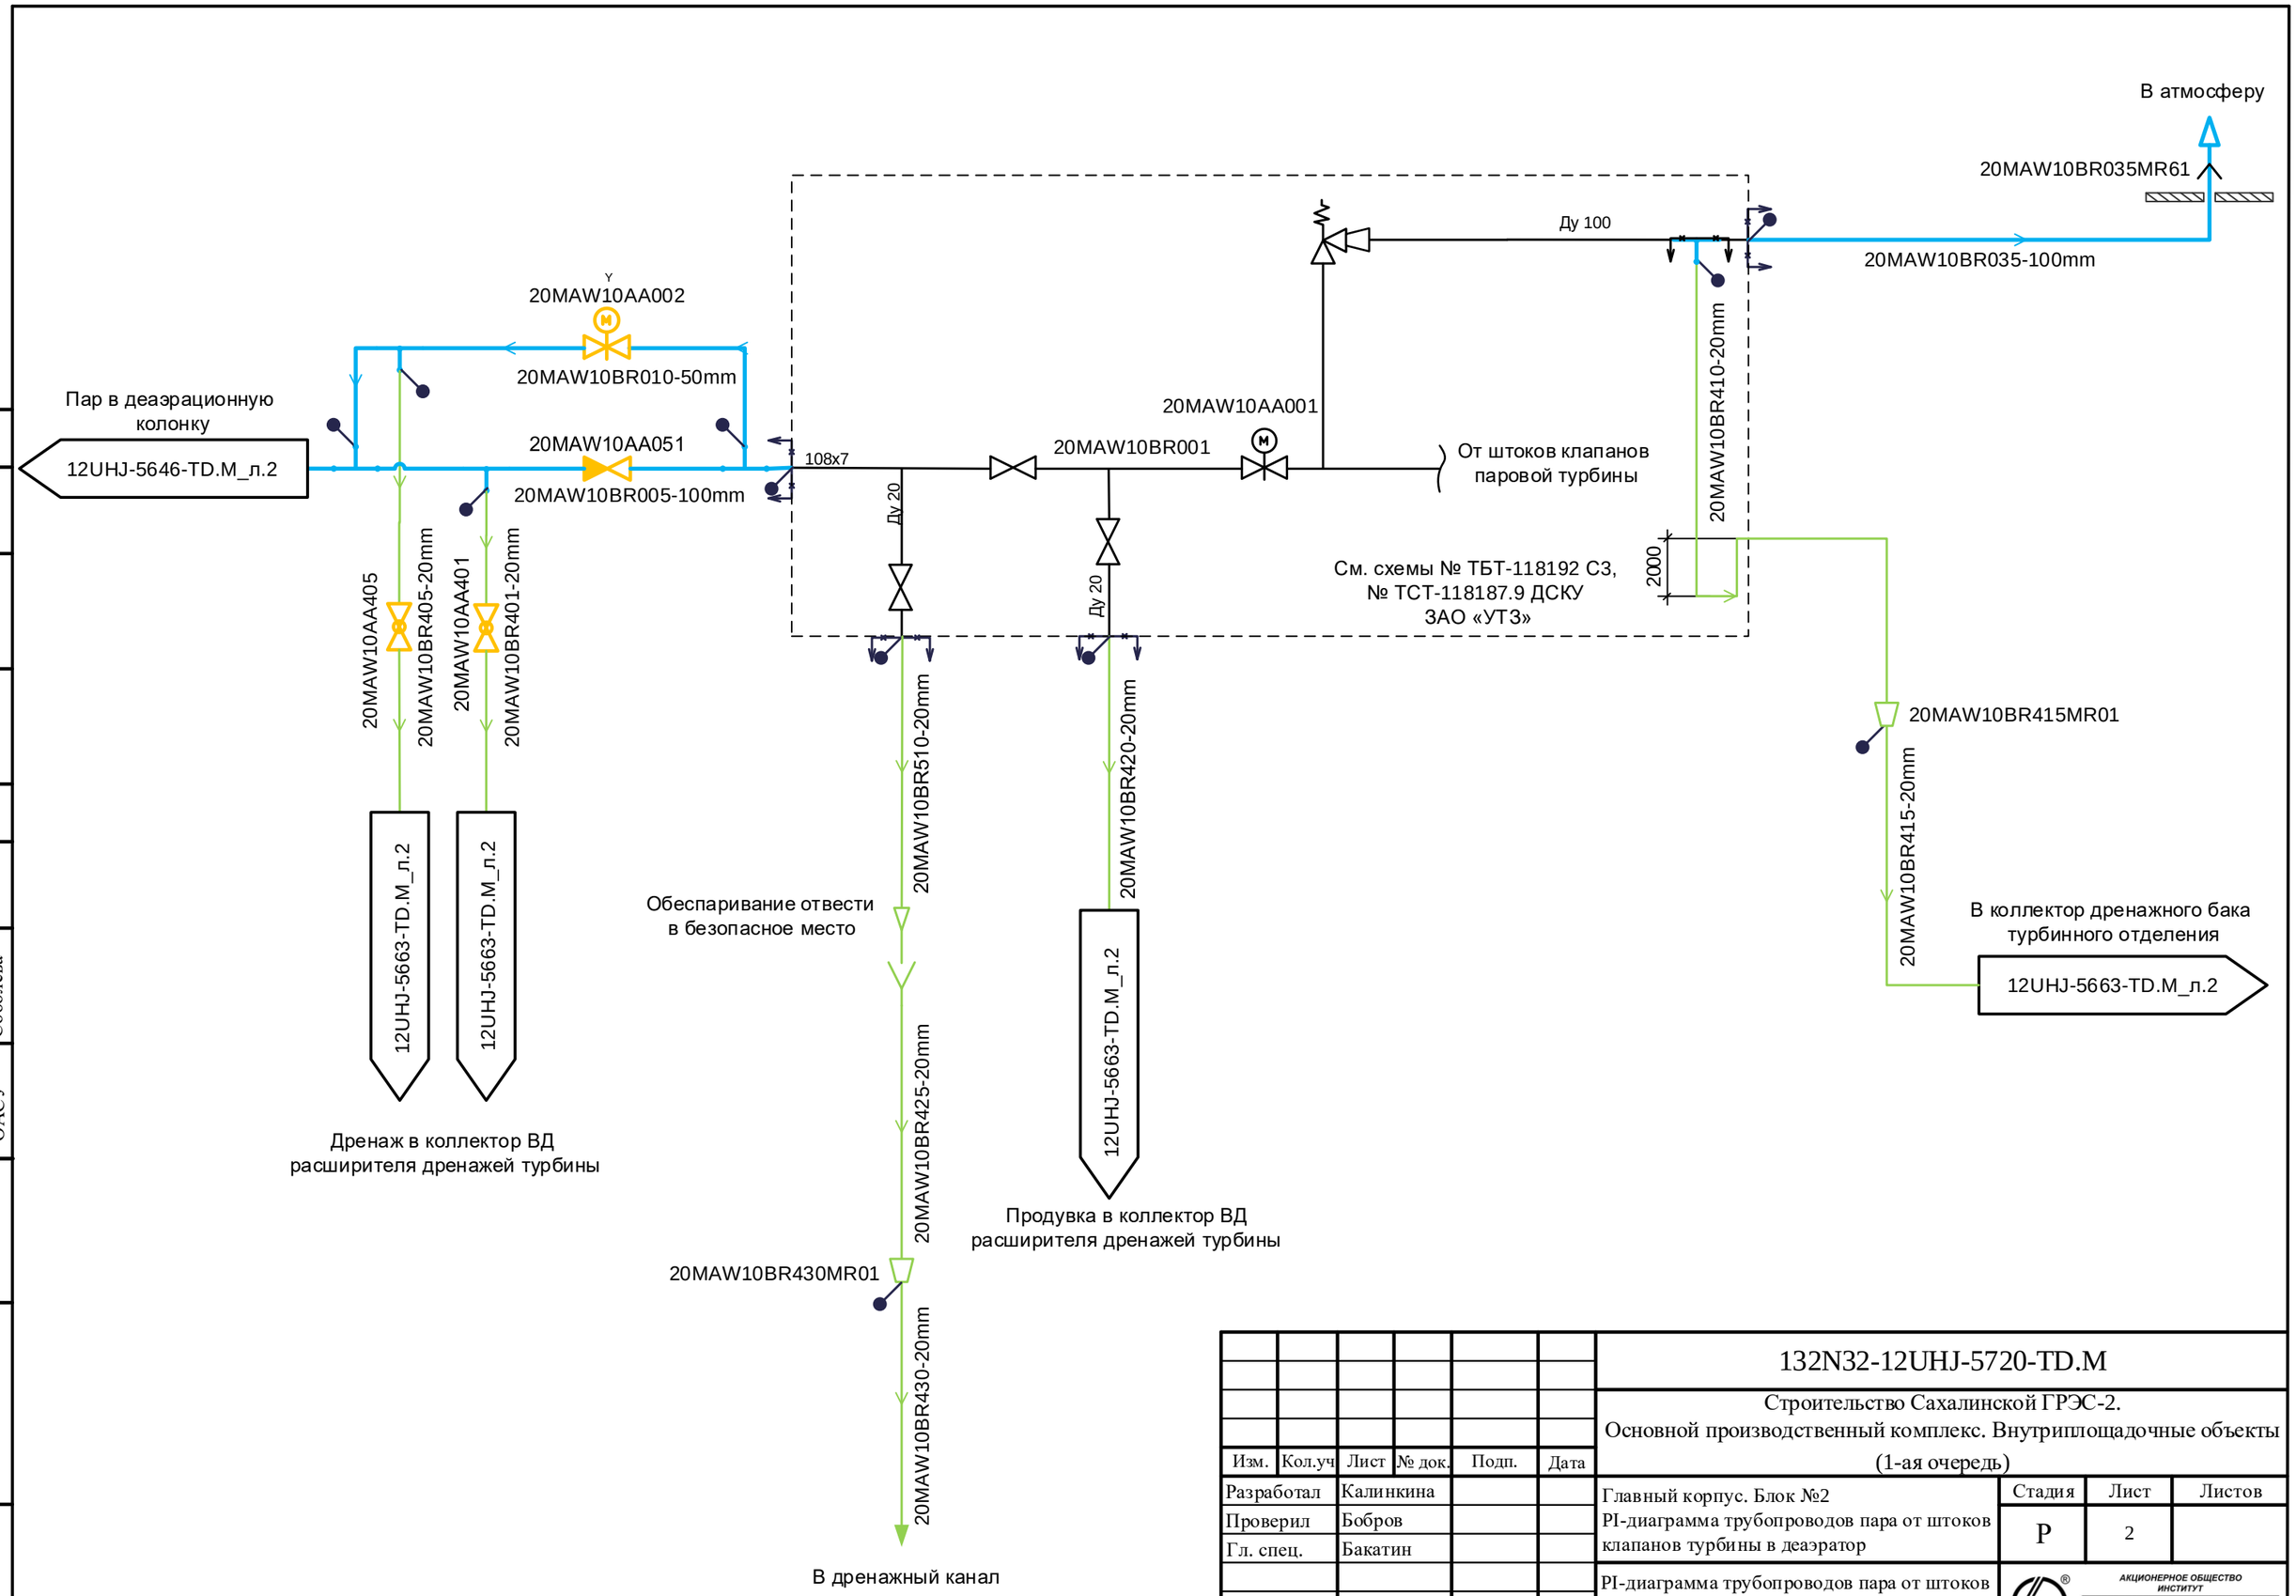

Согласовано

Соболева

ОАСУ

Взам. инв. №

Подпись и дата

Инв. № подл.

Изм.	Кол.уч	Лист	№ док.	Подп.	Дата
Разработал		Калинкина			
Проверил		Бобров			
Гл. спец.		Бакатин			
Н. контр.		Гридчина			

132N32-12UHJ-5720-TD.M

Строительство Сахалинской ГРЭС-2.
Основной производственный комплекс. Внутриплощадочные объекты (1-ая очередь)

Главный корпус. Блок №2
PI-диаграмма трубопроводов пара от штоков клапанов турбины в деаэратор

Стадия	Лист	Листов
Р	2	

PI-диаграмма трубопроводов пара от штоков клапанов турбины в деаэратор.
Система MAW

АКЦИОНЕРНОЕ ОБЩЕСТВО ИНСТИТУТ ТЕПЛОЭЛЕКТРОПРОЕКТ Г. МОСКВА

Формат А3