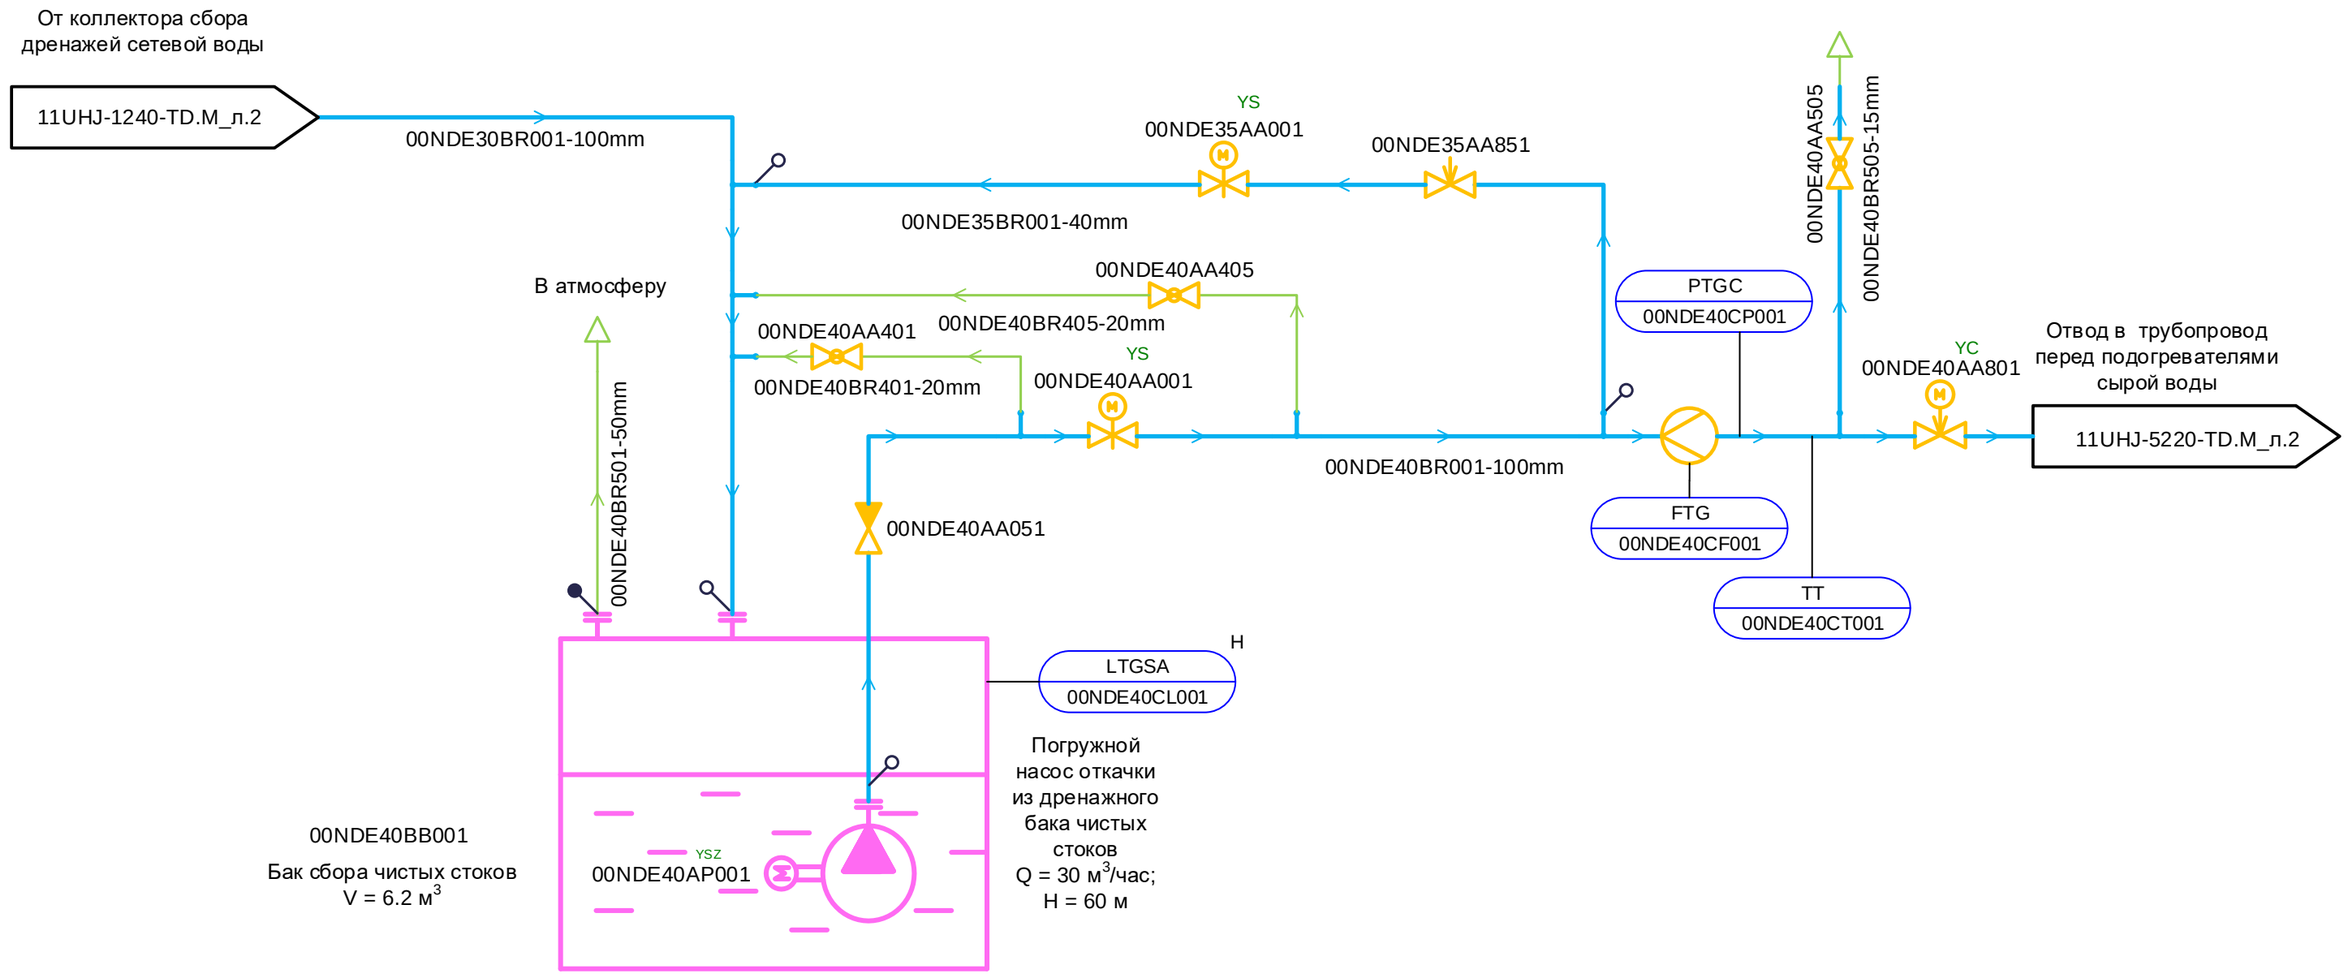

Изм.	Кол.уч	Лист	№ док.	Подп.	Дата
Разработал		Захарова			
Проверил		Калинкина			
Гл.спец.		Бакатин			
Н. контр.		Черемушкина			

132N32-11UHJ-5755-TD.M

Строительство Сахалинской ГРЭС-2.
Основной производственный комплекс. Внутриплощадочные объекты
(1-ая очередь)

Главный корпус.
PI-диаграмма трубопроводов сбора дренажей сетевой воды

Стадия	Лист	Листов
Р	2	

PI-диаграмма трубопроводов сбора дренажей сетевой воды. Система NDE

АКЦИОНЕРНОЕ ОБЩЕСТВО ИНСТИТУТ ТЕПЛОЭЛЕКТРОПРОЕКТ г. МОСКВА

Согласовано
Соболева
ОАСУ
Взам. инв. №
Подпись и дата
Инв. № подл.

Формат А3