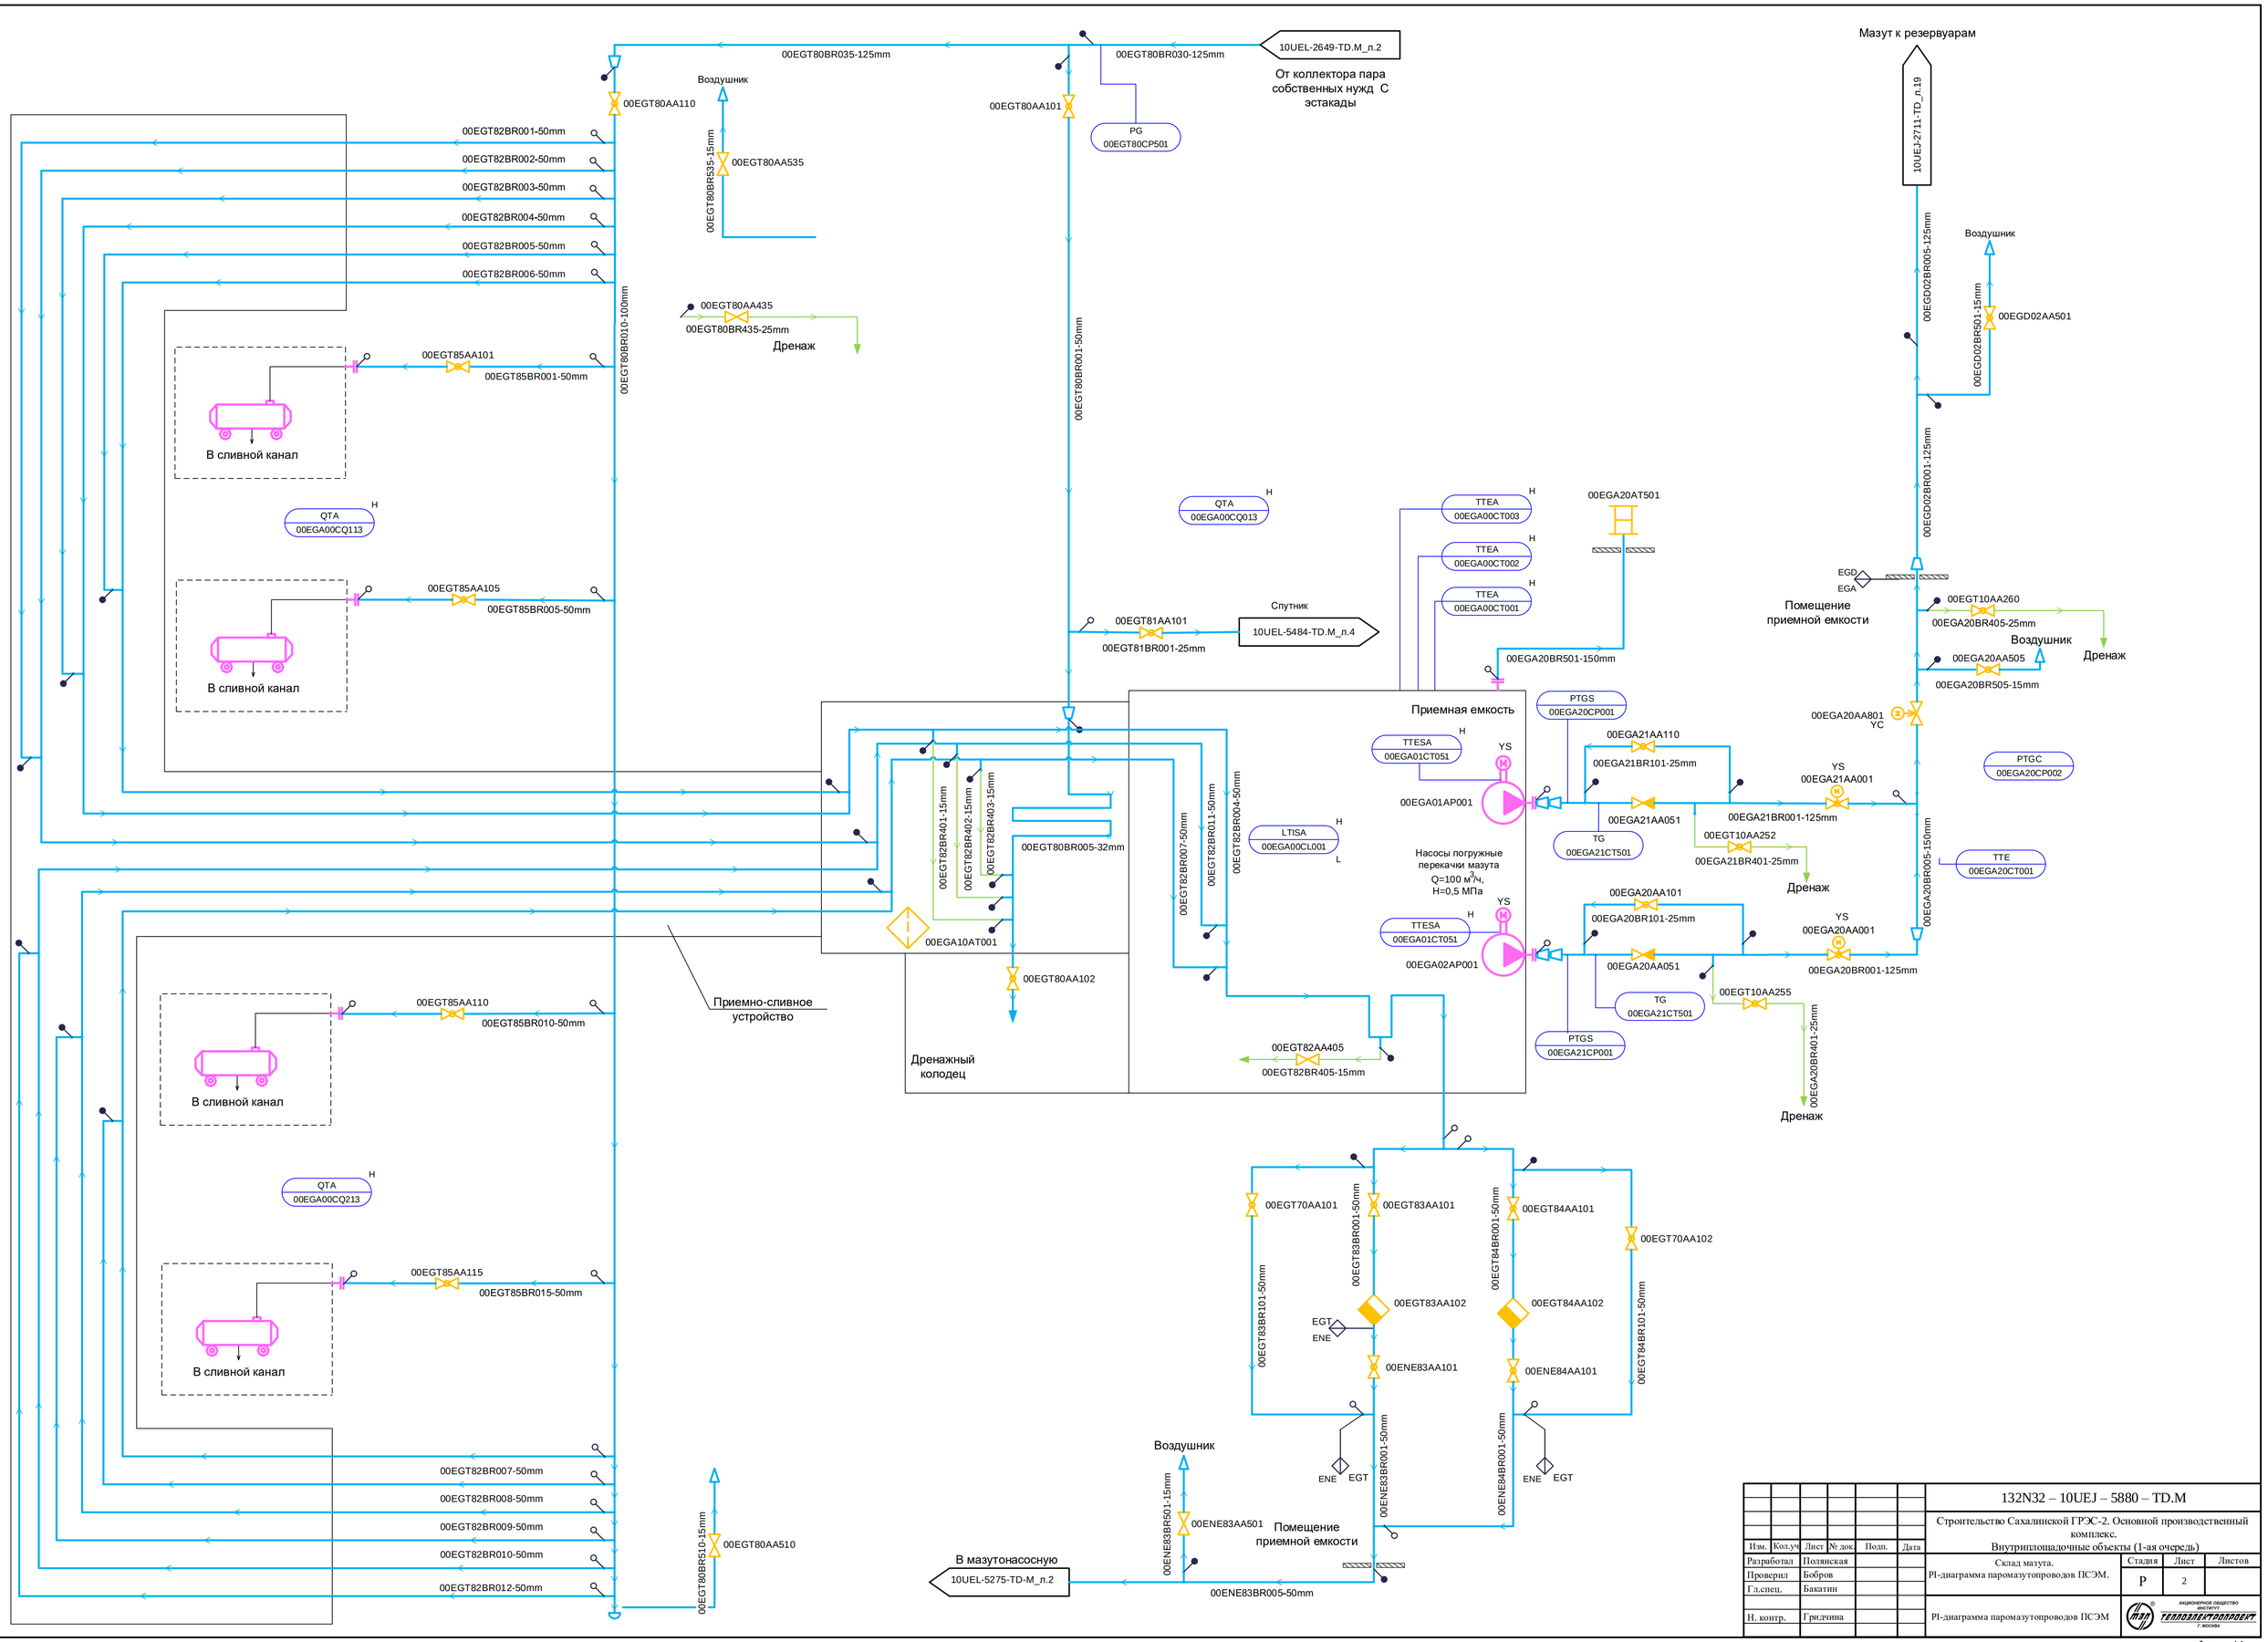

Изм.	Кол.уч	Лист	№ док.	Подп.	Дата	132N32 – 10UEJ – 5880 – TD.M
						Строительство Сахалинской ГРЭС-2. Основной производственный комплекс. Внутриплощадочные объекты (1-ая очередь)
Разработал		Полянская				Склад мазута. PI-диаграмма паромазутопроводов ПСЭМ.
Проверил		Бобров				Стадия: Р; Лист: 2; Листов:
Гл.спец.		Бакатин				
Н. контр.		Гридчина				PI-диаграмма паромазутопроводов ПСЭМ

АКЦИОНЕРНОЕ ОБЩЕСТВО ИНСТИТУТ ТЕПЛОЭЛЕКТРОПРОЕКТ г. МОСКВА

Согласовано

ОАСУ

Взам. инв. №

Подпись и дата

Инв. № подл.

Формат А1