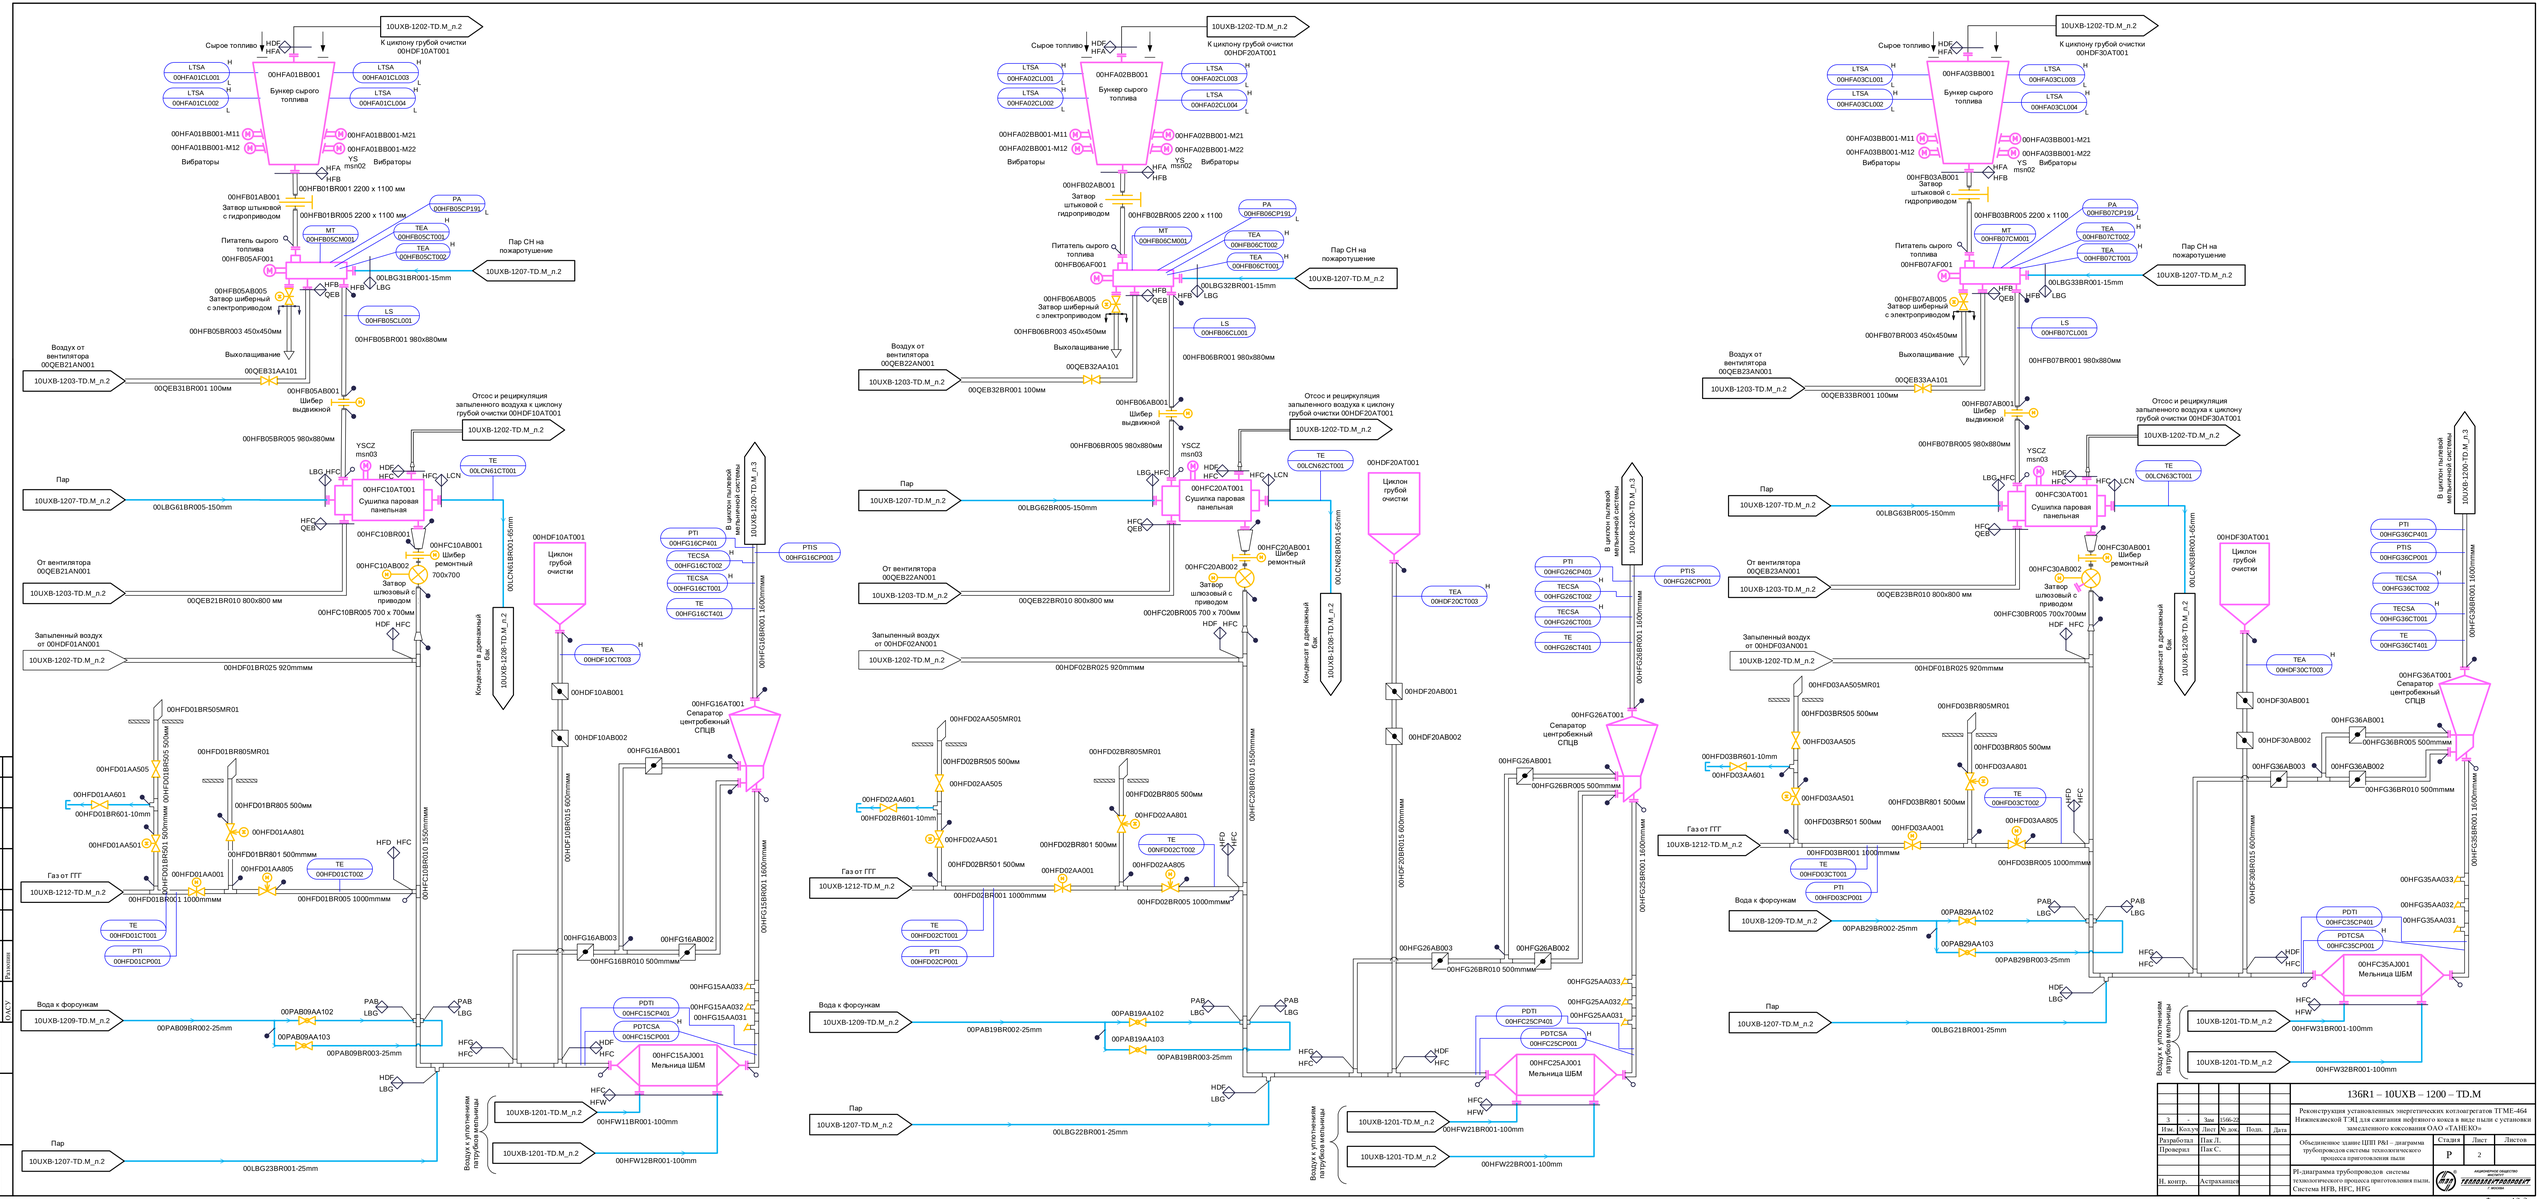

Изм.	Кол.уч.	Лист	№ док.	Подп.	Дата		
Разработал		Пан Л.				Стадия	Лист	Листов
Проверил		Пан С.				Р	2	
Н. контр.		Астраханцев						

Реконструкция установленных энергетических котлоагрегатов ТГМЕ-464 Нижнекамской ТЭЦ для сжигания нефтяного кокса в виде пыли с установки замедленного коксования ОАО «ТАНЕКО»

Объединение зданий ШПП РК4 – диаграмма трубопроводов системы технологического процесса приготовления пыли

ГП-диаграмма трубопроводов системы технологического процесса приготовления пыли. Система HFB, HFC, HFG

ЗАПОРНАЯ АРМАТУРА ТЕХНОПРОМЭКСПОРТ

Согласовано

Взам. инв. №

Подпись и дата

Инв. № подл.

Формат А2х3