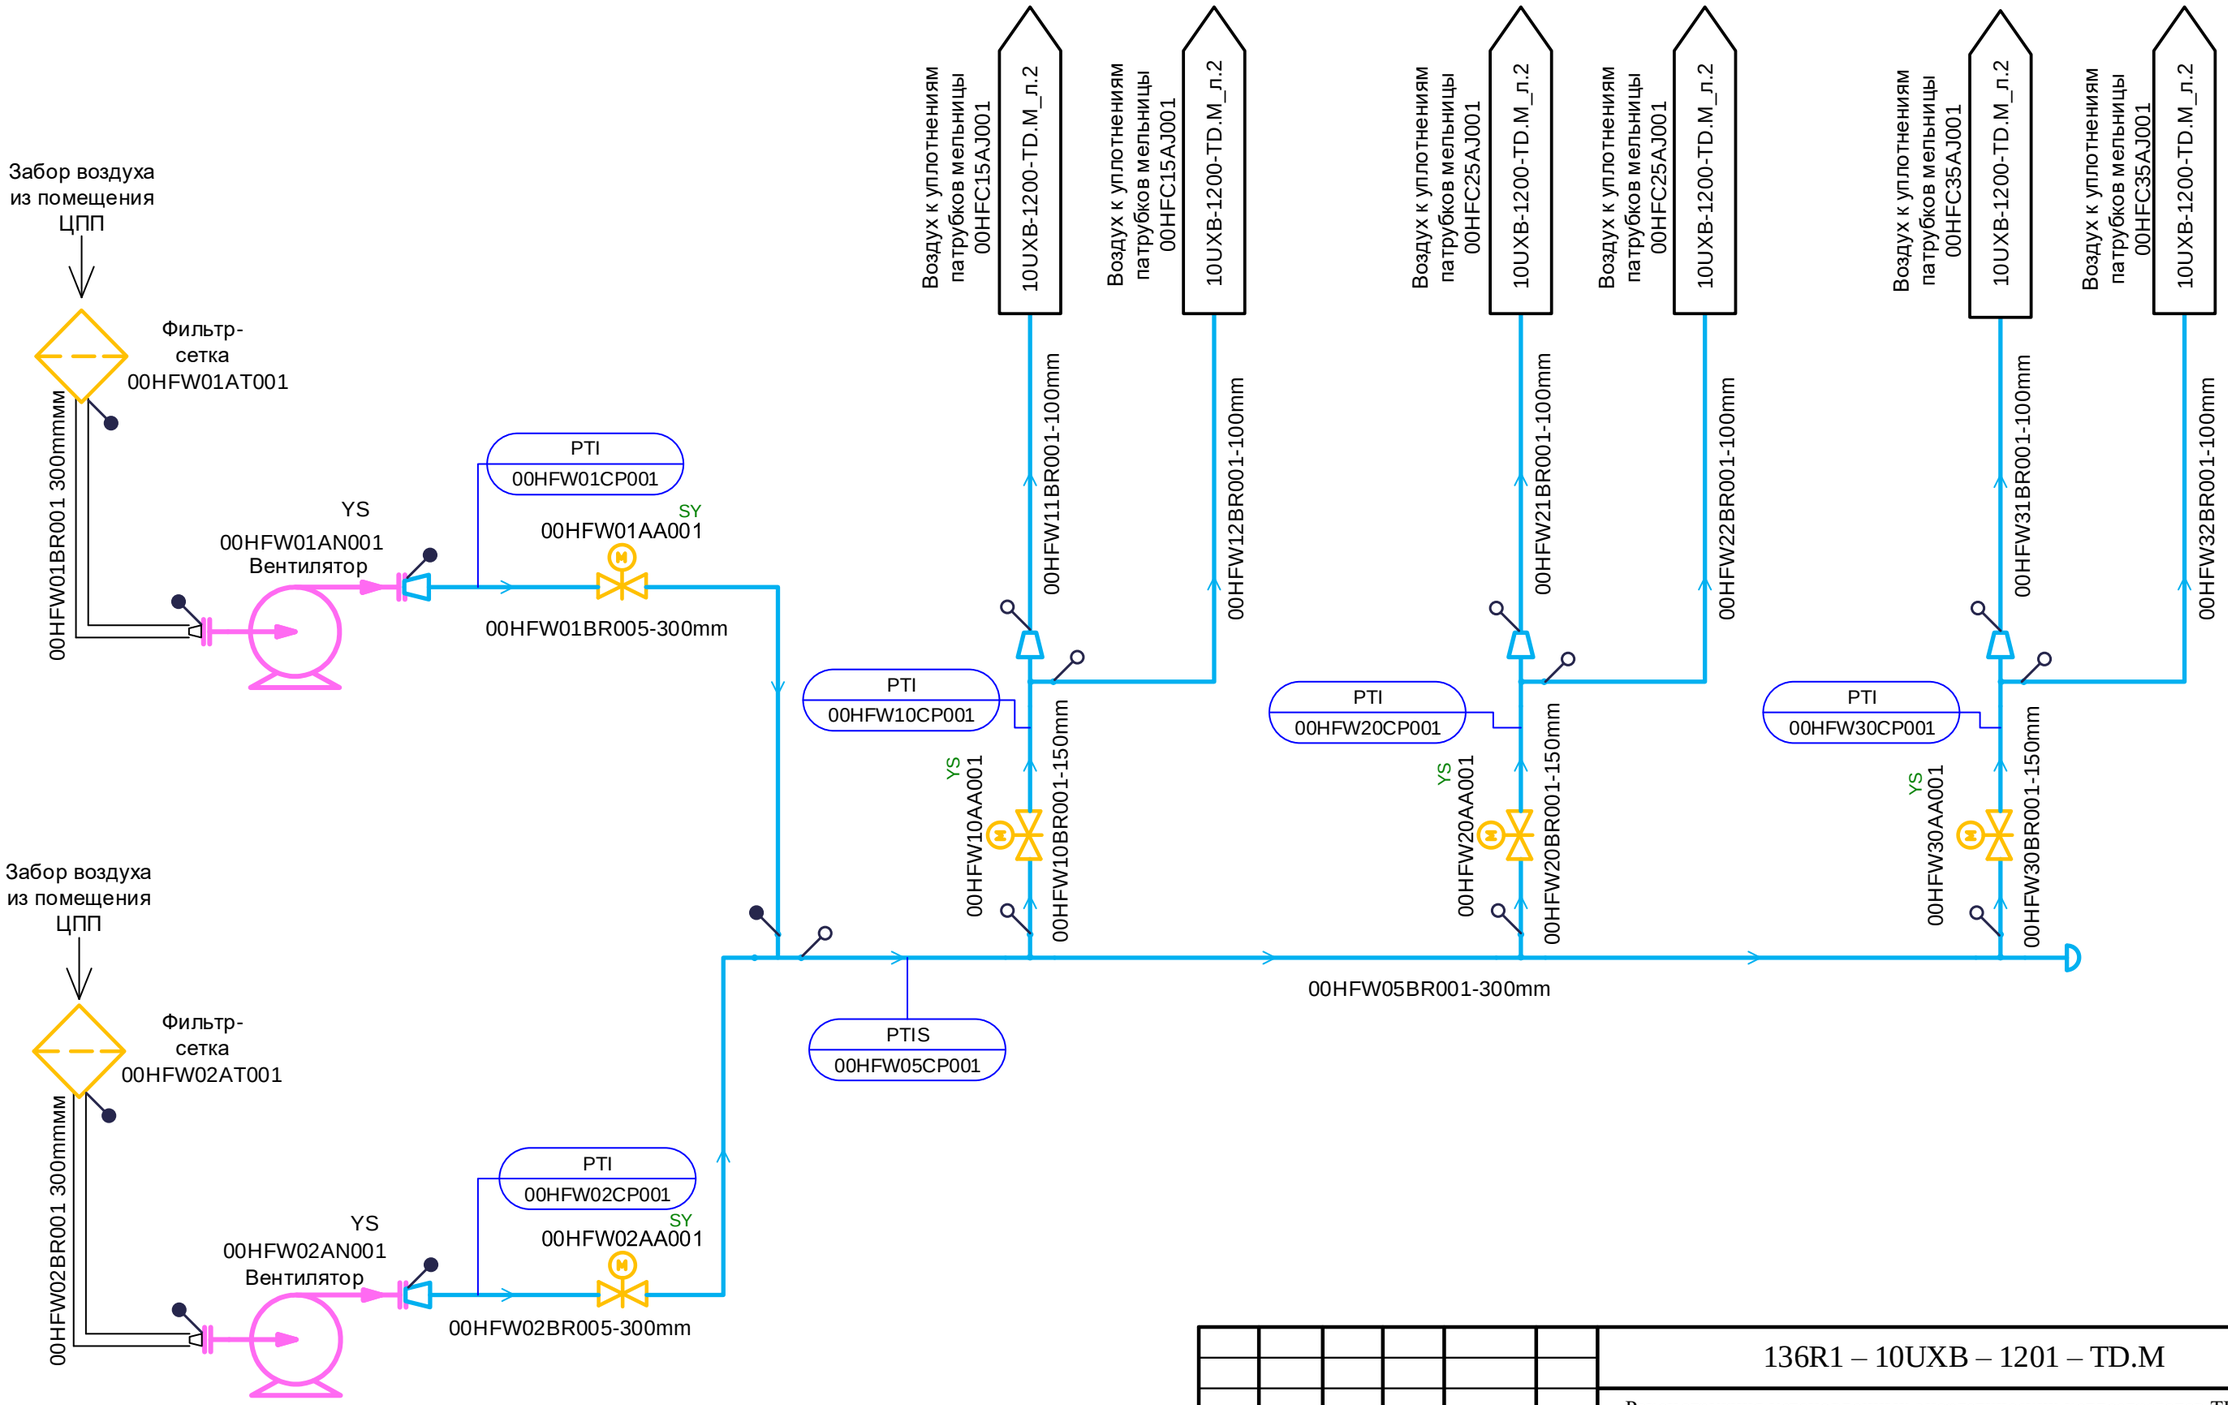

2	-	Зам	354-22		04.22	136R1 – 10UXB – 1201 – TD.M
Изм.	Кол.уч	Лист	№ док.	Подп.	Дата	Реконструкция установленных энергетических котлоагрегатов ТГМЕ-464 Нижнекамской ТЭЦ для сжигания нефтяного кокса в виде пыли с установки замедленного коксования ОАО «ТАНЕКО»
Разработал		Пак Л.			04.22	Объединенное здание ЦПП P&I – диаграмма трубопроводов воздуха на уплотнение патрубков мельниц
Проверил		Пак С.			04.22	
Н. контр.		Астраханцев			04.22	PI-диаграмма трубопроводов воздуха на уплотнение патрубков мельниц. Система HFW

Стадия	Лист	Листов
Р	2	

АКЦИОНЕРНОЕ ОБЩЕСТВО ИНСТИТУТ ТЕПЛОЭЛЕКТРОПРОЕКТ Г. МОСКВА

Согласовано
ОАСУ Соболева 04.22

Взам. инв. №
Подпись и дата
Инв. № подл.

Формат А3