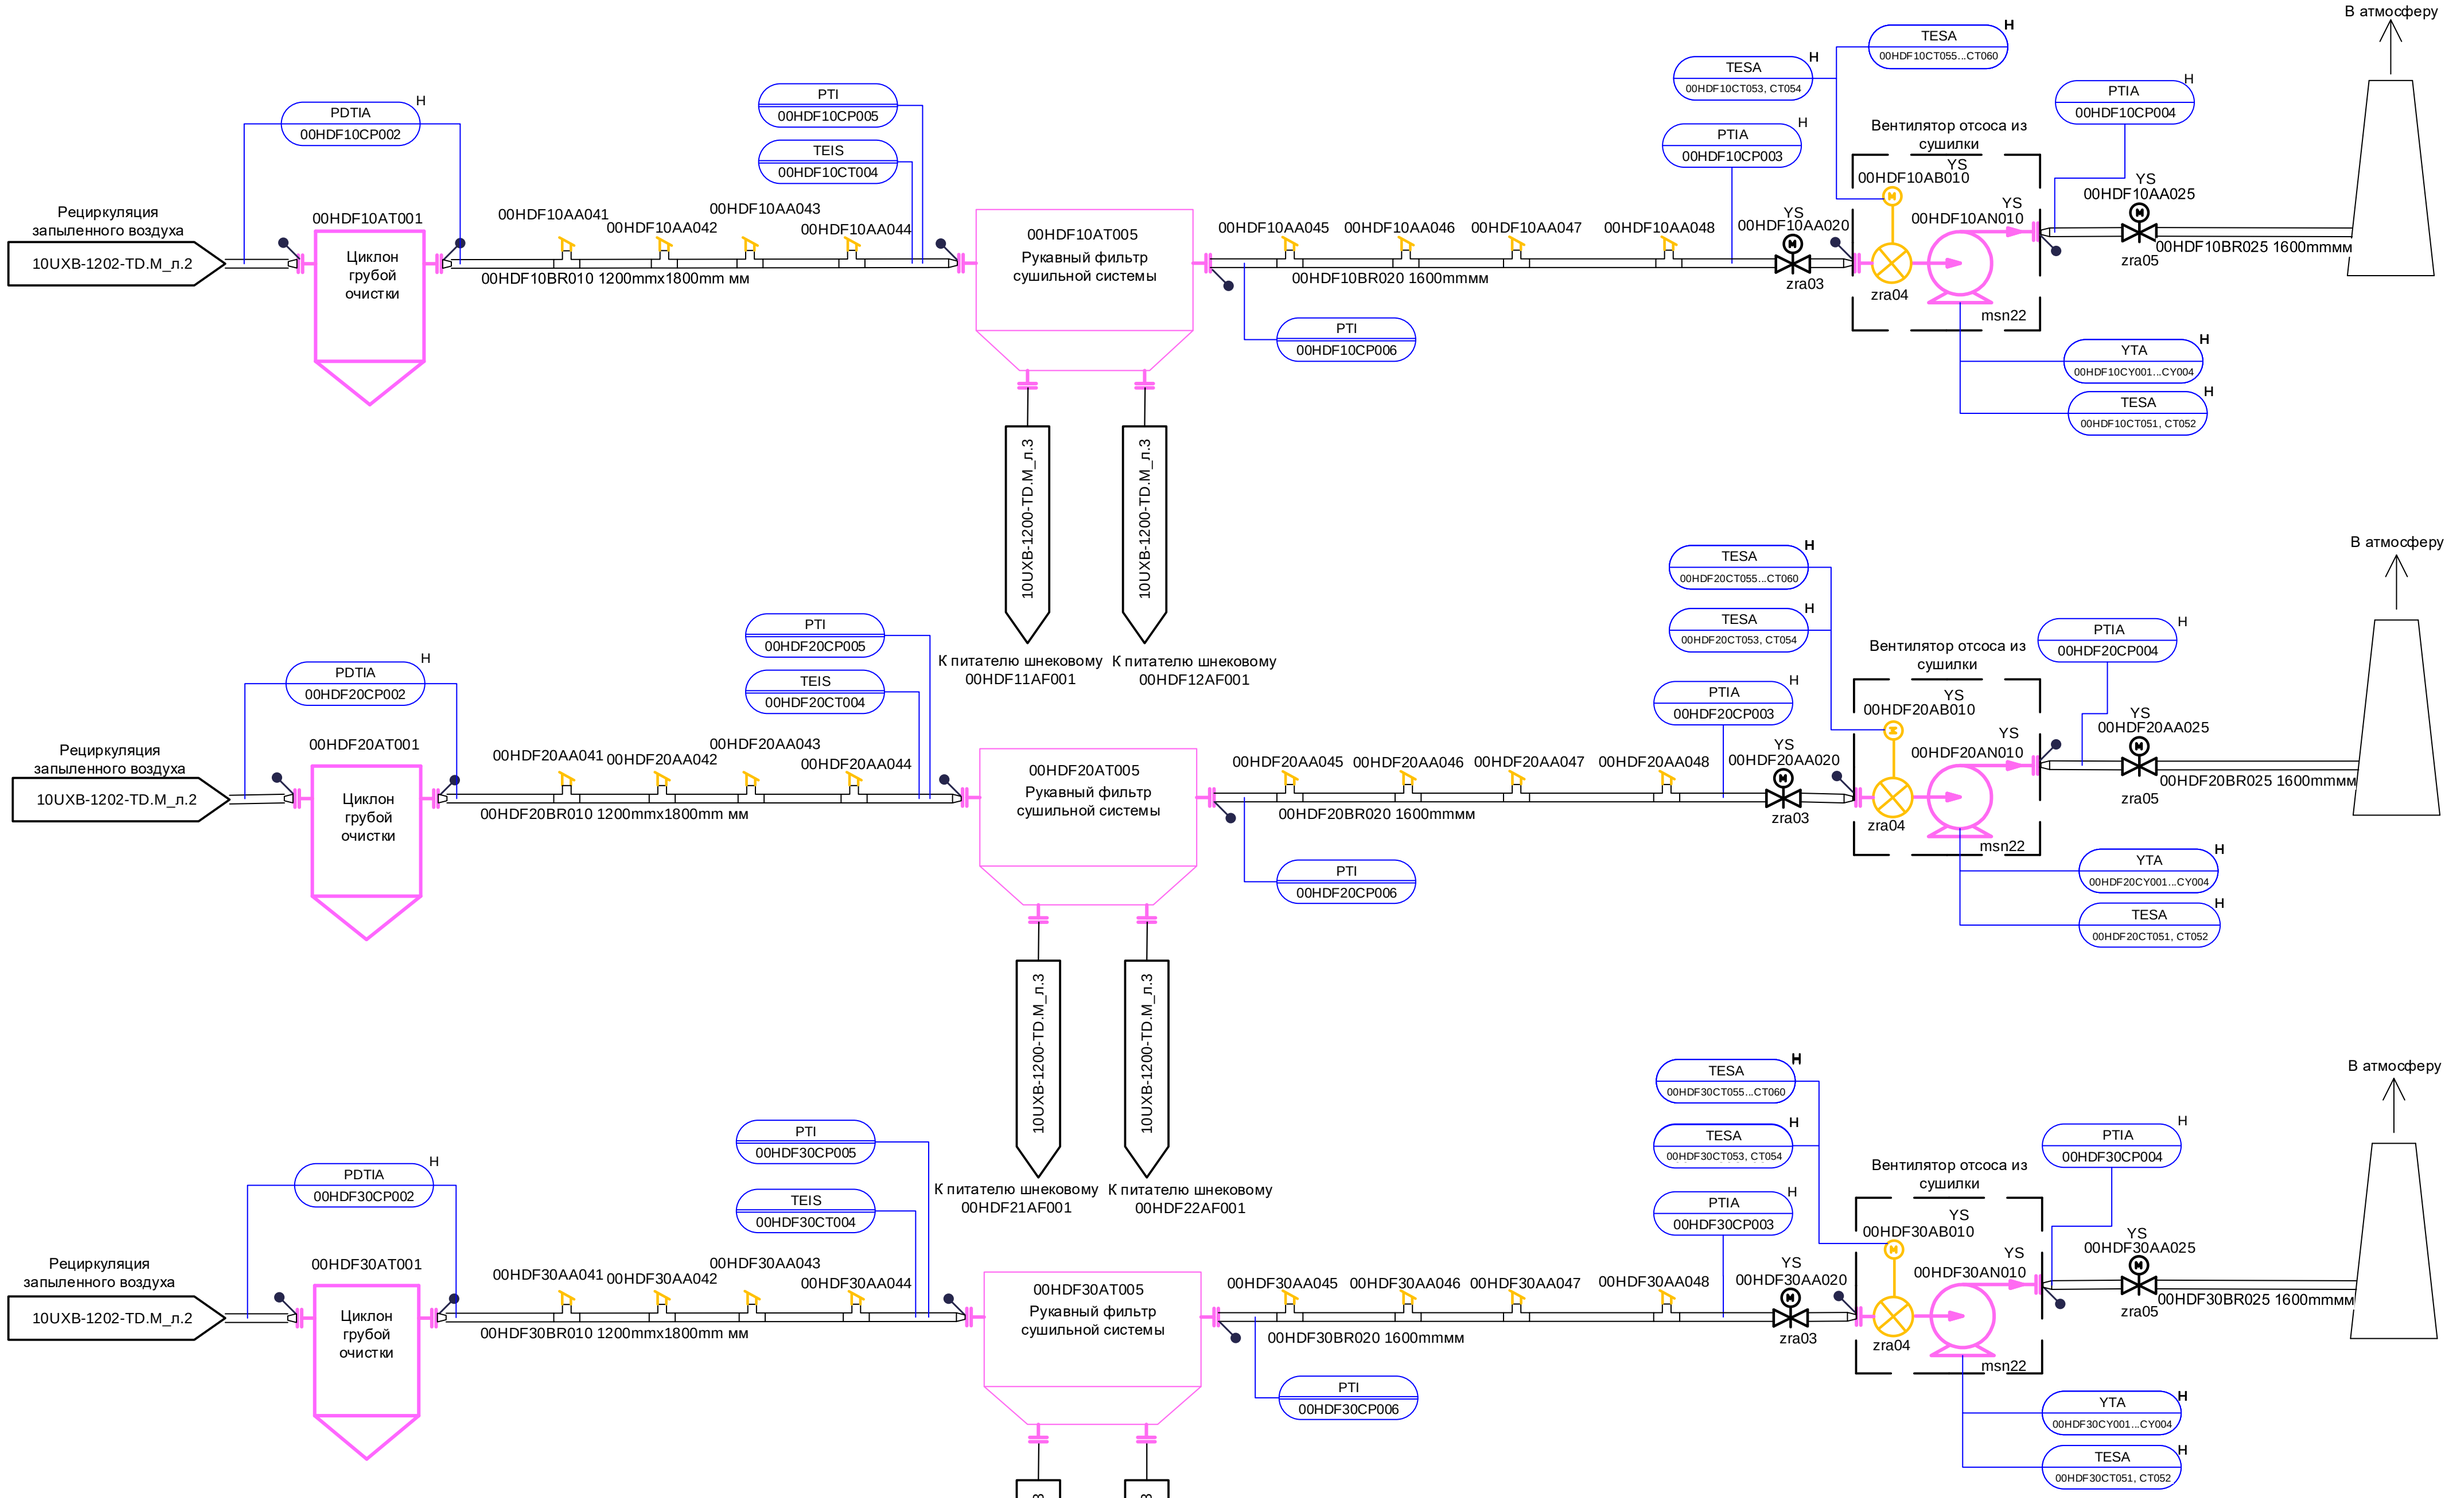

2	-	Зам	151-19			
Изм.	Кол.уч	Лист	№ док.	Подп.	Дата	
Разработал		Пак Л.				
Проверил		Пак С.				
Н. контр.		Астраханцев				

136R1 – 10UXB – 1202 – TD.M

Реконструкция установленных энергетических котлоагрегатов ТГМЕ-464 Нижнекамской ТЭЦ для сжигания нефтяного кокса в виде пыли с установки замедленного коксования ОАО «ТАНЕКО»

Объединенное здание ЦПП P&I – диаграмма трубопроводов отсоса и рециркуляции запыленного воздуха

Стадия	Лист	Листов
Р	3	

PI-диаграмма трубопроводов отсоса, рециркуляции и выброса запыленного воздуха. Система HDF

АКЦИОНЕРНОЕ ОБЩЕСТВО ИНСТИТУТ ТЕПЛОЭЛЕКТРОПРОЕКТ Г. МОСКВА

Согласовано

ОАСУ

Разозпин

Взам. инв. №

Подпись и дата

Инв. № подл.

Формат А2