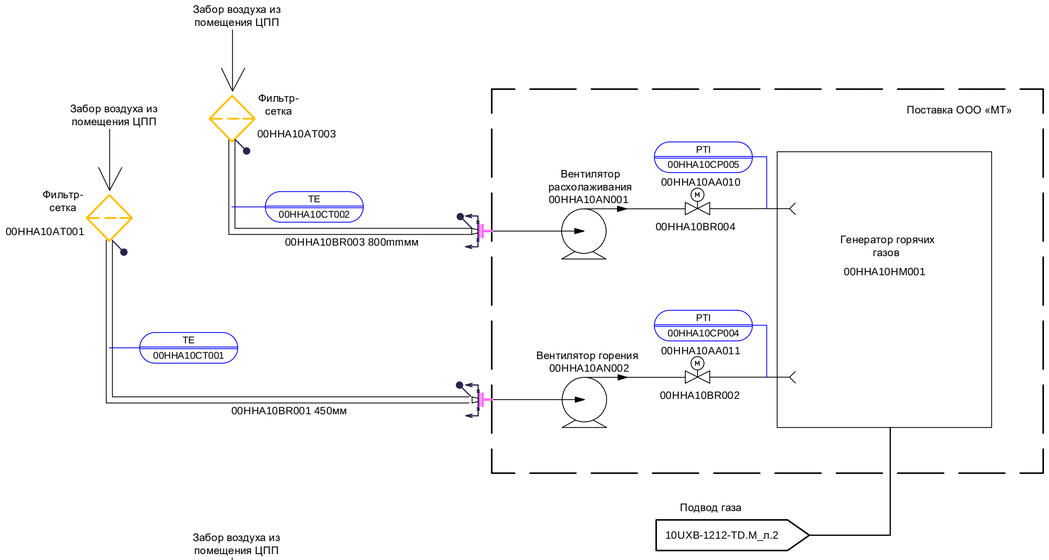

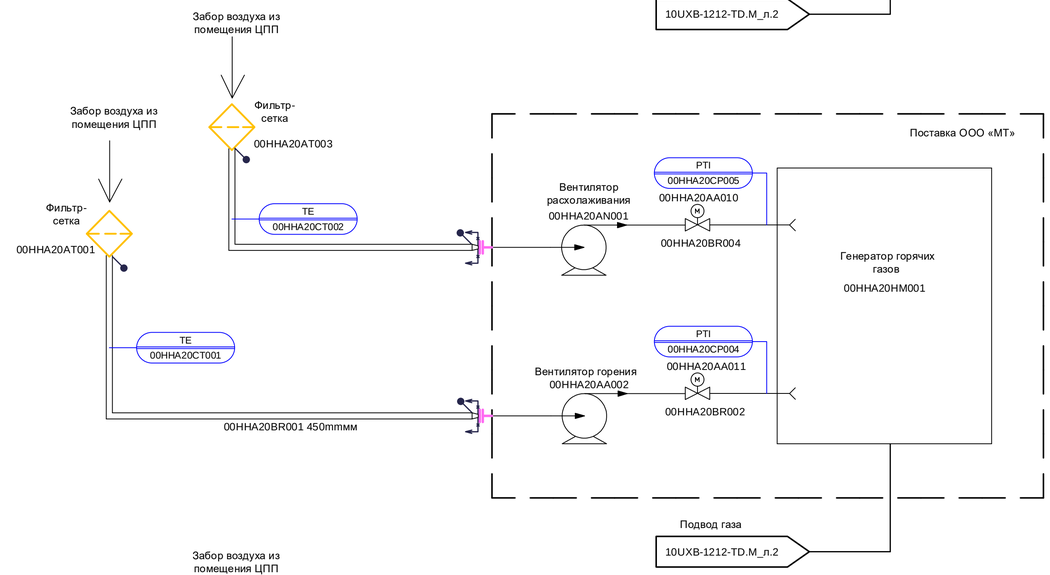

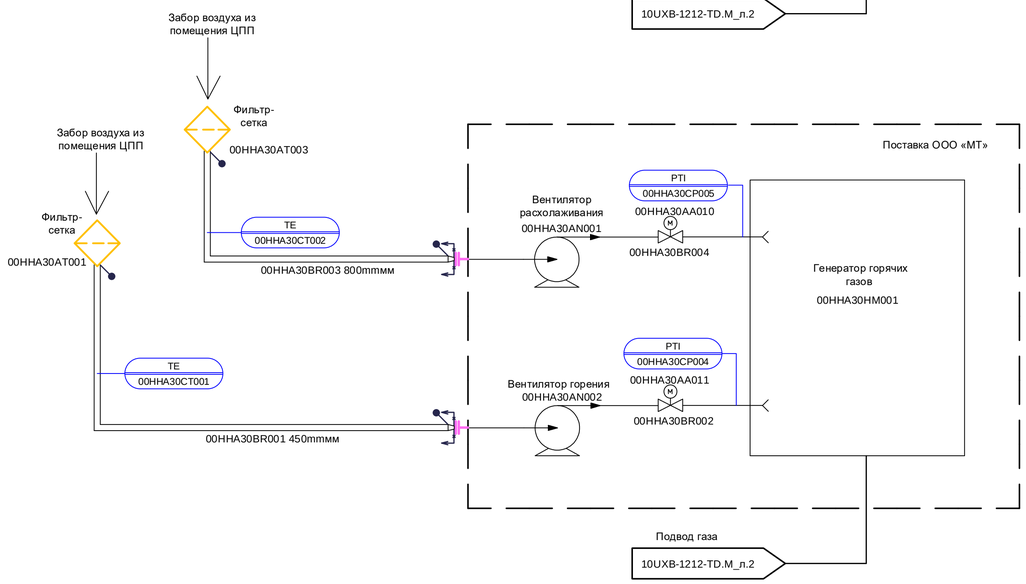

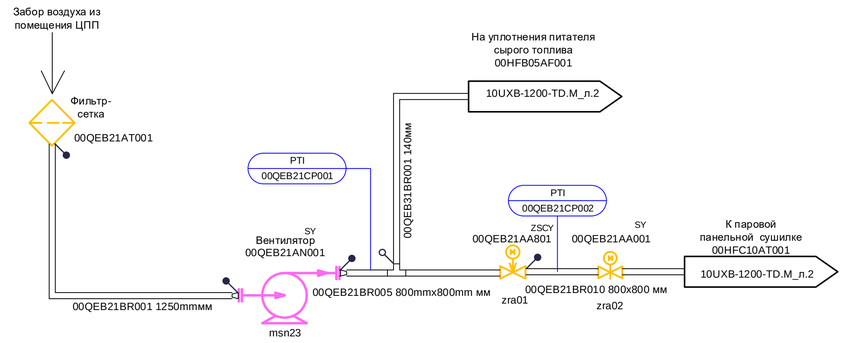

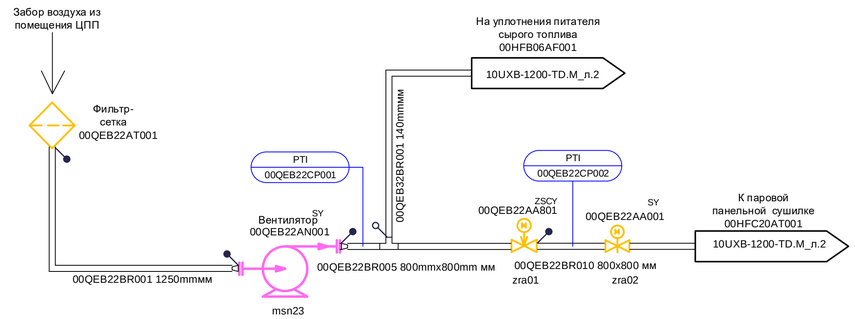

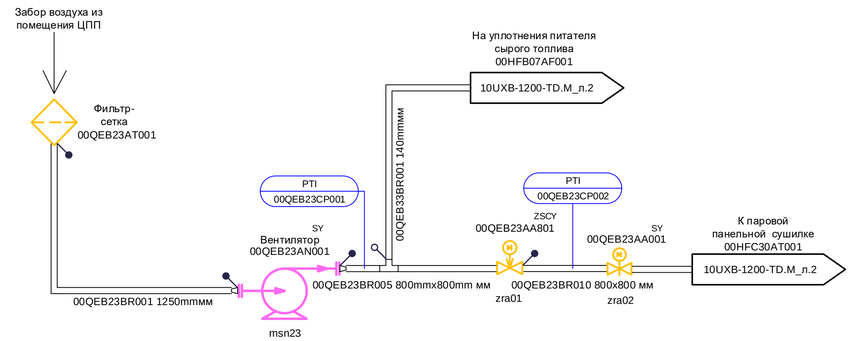

Температура воздуха в помещении ЦПП

TE
00QEB00CT001

2	-	Зам	354-22		04.22	136R1 – 10UXB – 1203 – TD.M
Изм.	Кол.уч	Лист	№ док.	Подп.	Дата	Реконструкция установленных энергетических котлоагрегатов ТГМЕ-464 Нижнекамской ТЭЦ для сжигания нефтяного кокса в виде пыли с установки замедленного коксования ОАО «ТАНЕКО»
Разработал		Кудрявцева			04.22	Объединенное здание ЦПП P&I – диаграмма трубопроводов системы воздухоотбора для вентиляции сушилки и подачи воздуха для газогенератора
Проверил		Пак С.			04.22	Стадия: Р; Лист: 2; Листов:
Н. контр.		Астраханцев			04.22	PI-диаграмма трубопроводов воздуха на ГТГ и ППС. Система ННА, QEB

АКЦИОНЕРНОЕ ОБЩЕСТВО ИНСТИТУТ ТЕПЛОЭЛЕКТРОПРОЕКТ г. МОСКВА

Согласовано
ОАСУ Соболева 04.22
Взам. инв. №
Подпись и дата
Инв. № подл.

Формат А1