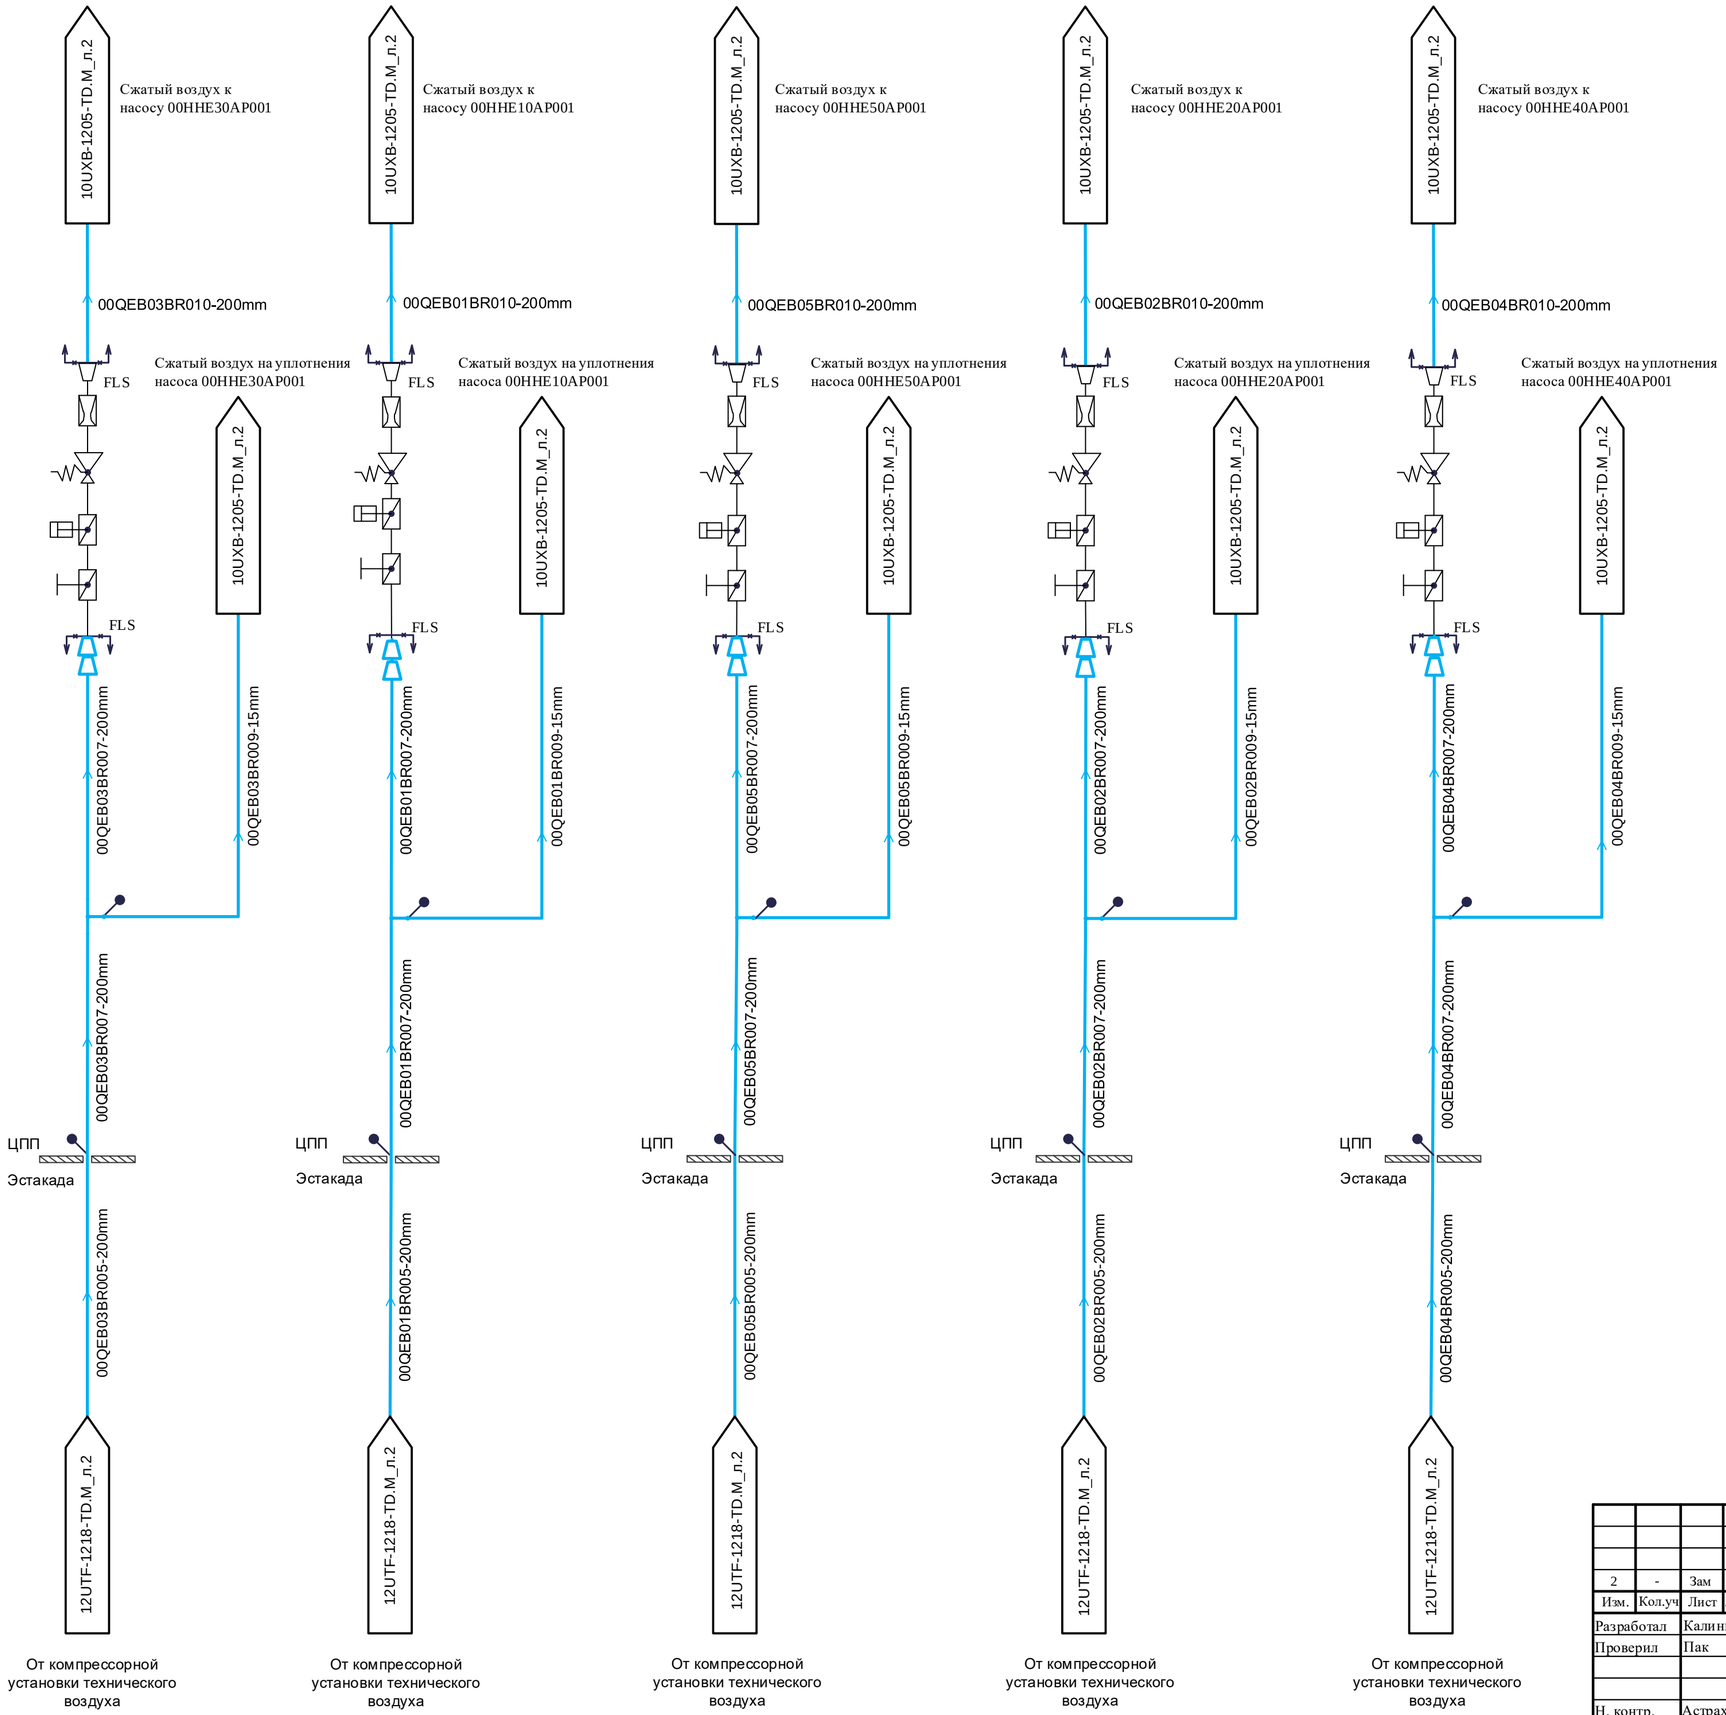

2	-	Зам	595-20			
Изм.	Кол.уч	Лист	№ док.	Подп.	Дата	
Разработал		Калинкина				
Проверил		Пак				
Н. контр.		Астраханцев				

136R1 – 10UXB – 1204 – TD.M

Реконструкция установленных энергетических котлоагрегатов ТГМЕ-464 Нижнекамской ТЭЦ для сжигания нефтяного кокса в виде пыли с установки замедленного коксования ОАО «ТАНЕКО»

Объединенное здание ЦПП. P&I – диаграмма трубопроводов сжатого воздуха для транспортировки пыли из бункера ЦПЗ в бункера пыли котлов

Стадия	Лист	Листов
Р	2	

PI-диаграмма трубопроводов сжатого воздуха для транспортировки пыли из бункера ЦПЗ в бункеры пыли котлов. Система QEB

АКЦИОНЕРНОЕ ОБЩЕСТВО ИНСТИТУТ ТЕПЛОЭЛЕКТРОПРОЕКТ Г. МОСКВА

Согласовано

ОАСУ Соболева

Взам. инв. №

Подпись и дата

Инв. № подл.

Формат А2