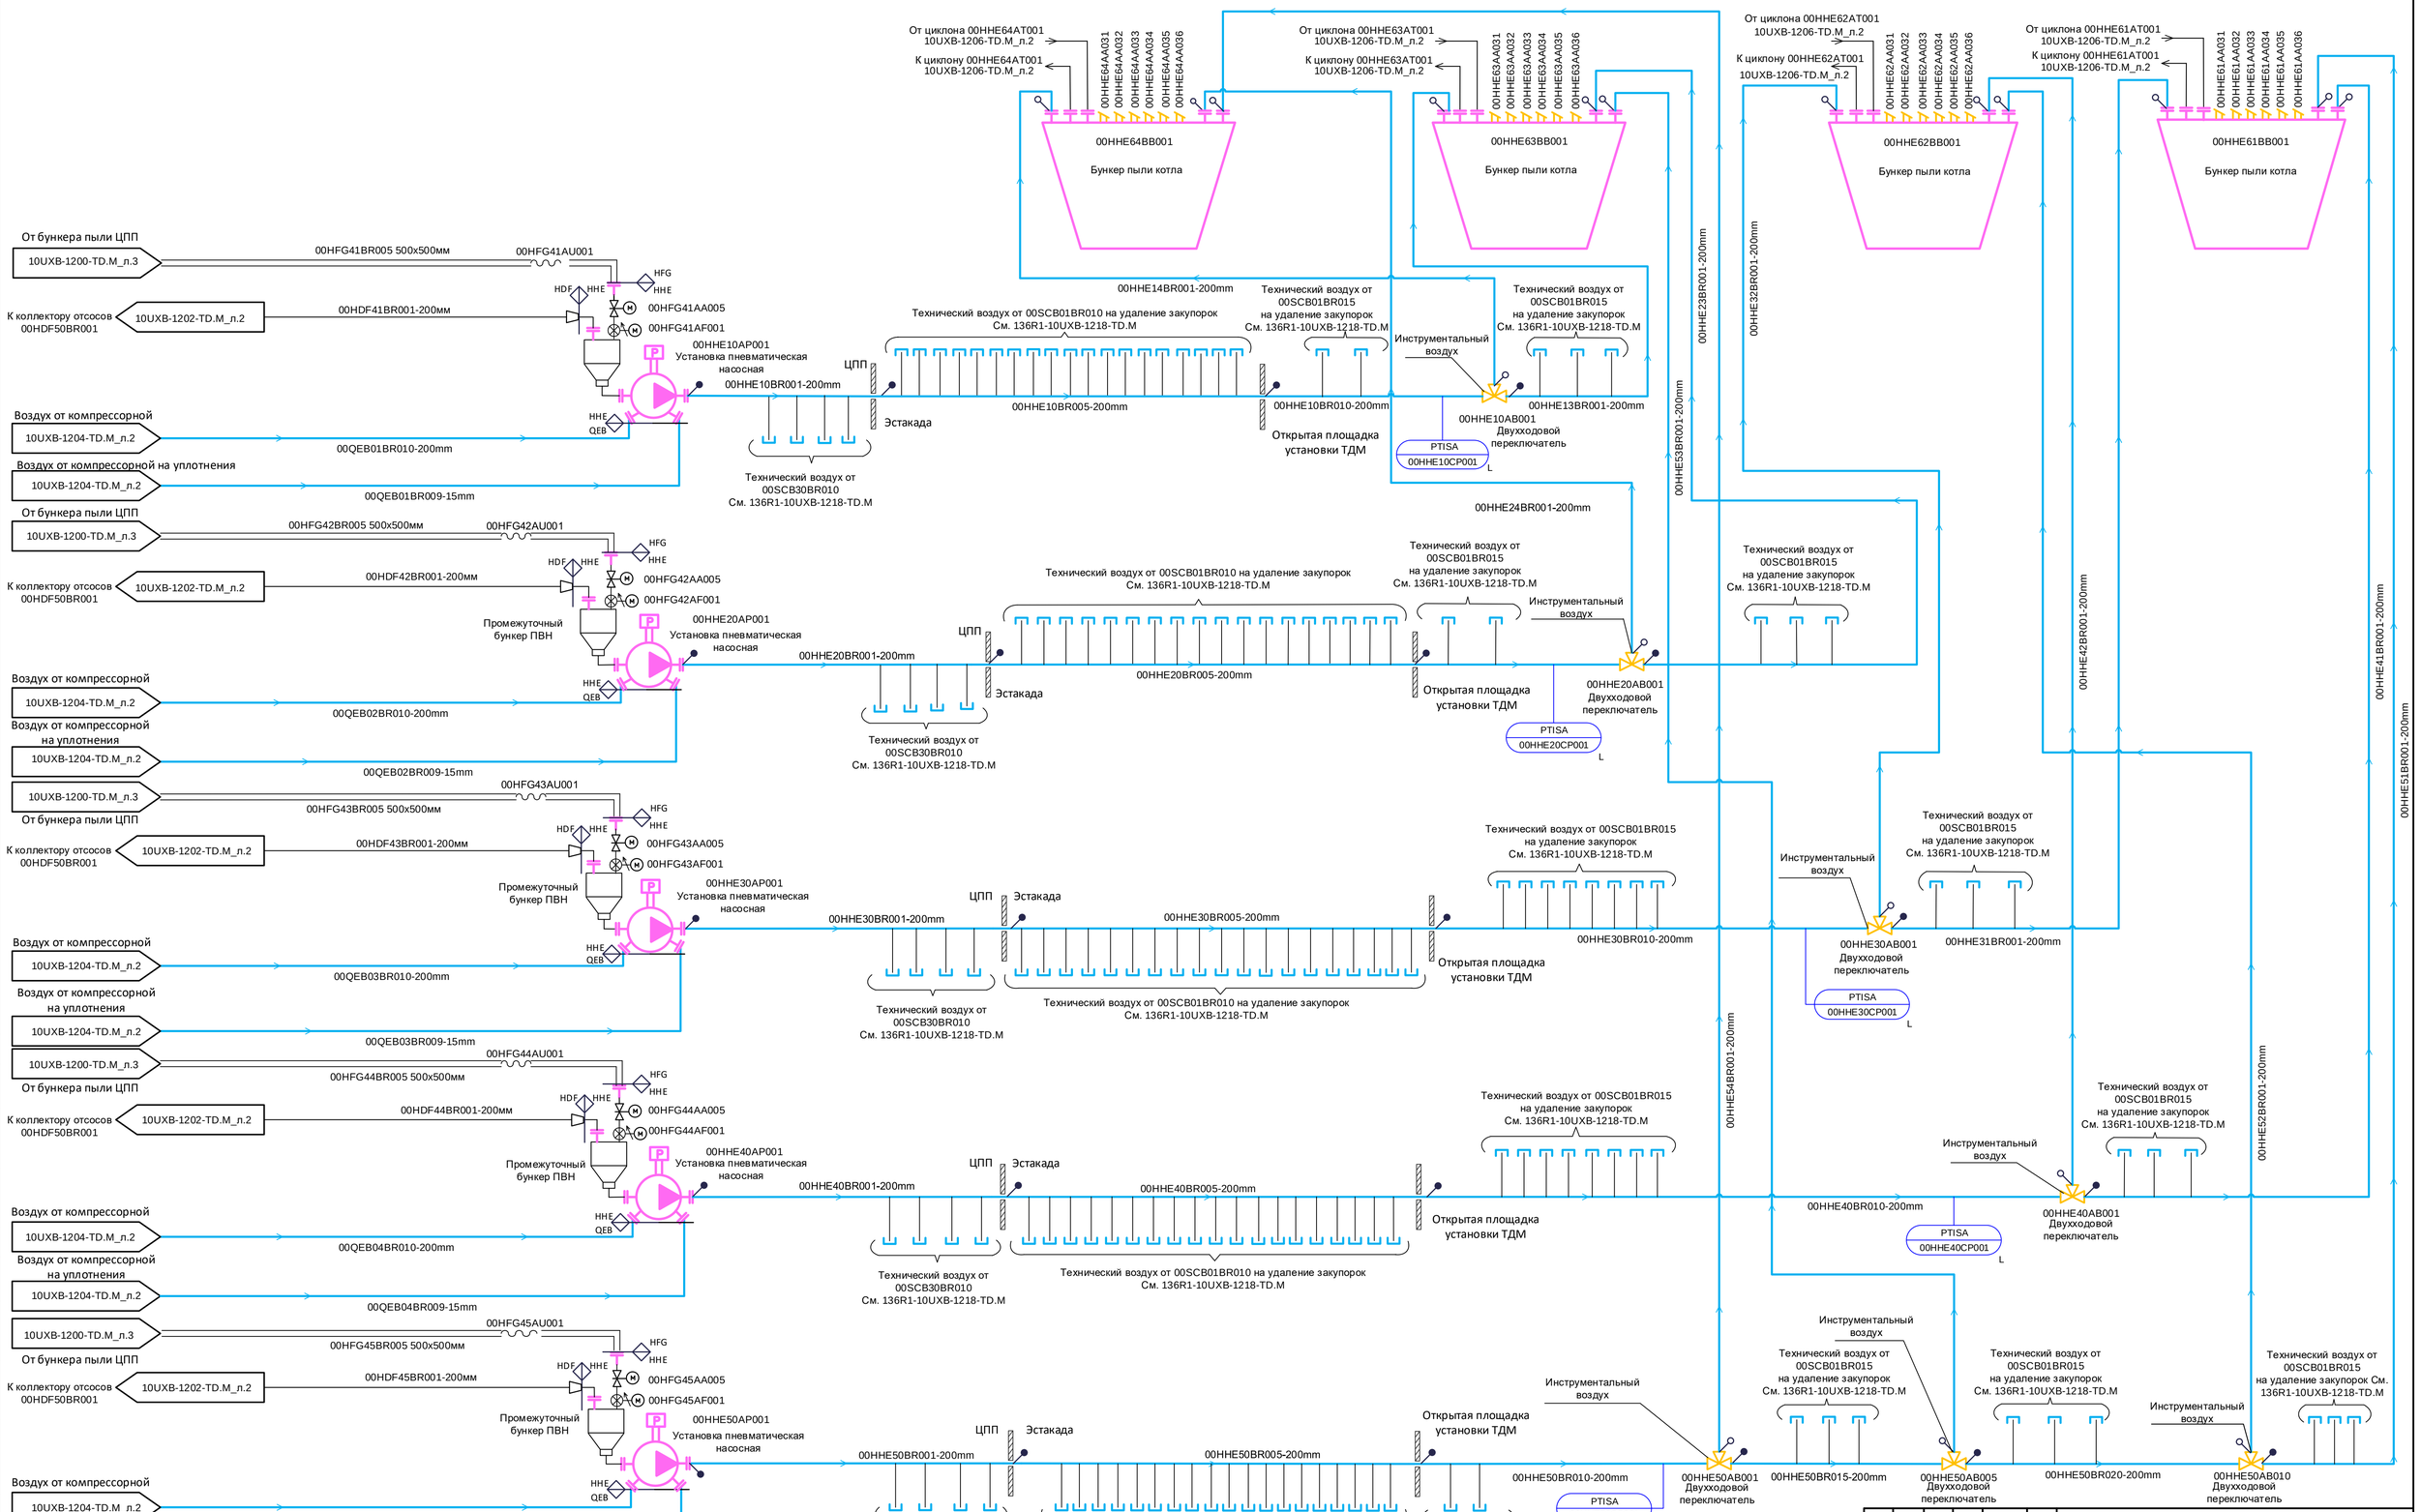

Примечание: Нет ИД на ПВН, двухходовые переключатели

1	-	Зам	151-19			
Изм.	Кол.уч	Лист	№ док.	Подп.	Дата	

136R1 – 10UXB – 1205 – TD.M

Реконструкция установленных энергетических котлоагрегатов ТГМЕ-464 Нижнекамской ТЭЦ для сжигания нефтяного кокса в виде пыли с установки замедленного коксования ОАО «ТАНЕКО»

Разработал	Пак Л.		
Проверил	Пак С.		
Н. контр.	Астраханцев		

Объединенное здание ЦПП P&I – диаграмма пылепроводов от бункера пыли ЦПП в бункеры пыли котлов

Стадия	Лист	Листов
Р	2	

PI-диаграмма пылепроводов от бункера пыли ЦПП в бункеры пыли котлов. Система HHE

АКЦИОНЕРНОЕ ОБЩЕСТВО ФИРМА ОРГЭНЕРГОСТРОЙ ТЕПЛОЭЛЕКТРОПРОЕКТ Г. МОСКВА

Согласовано

ОАСУ | Резунин

Взам. инв. № | Подпись и дата | Инв. № подл.

Формат А1