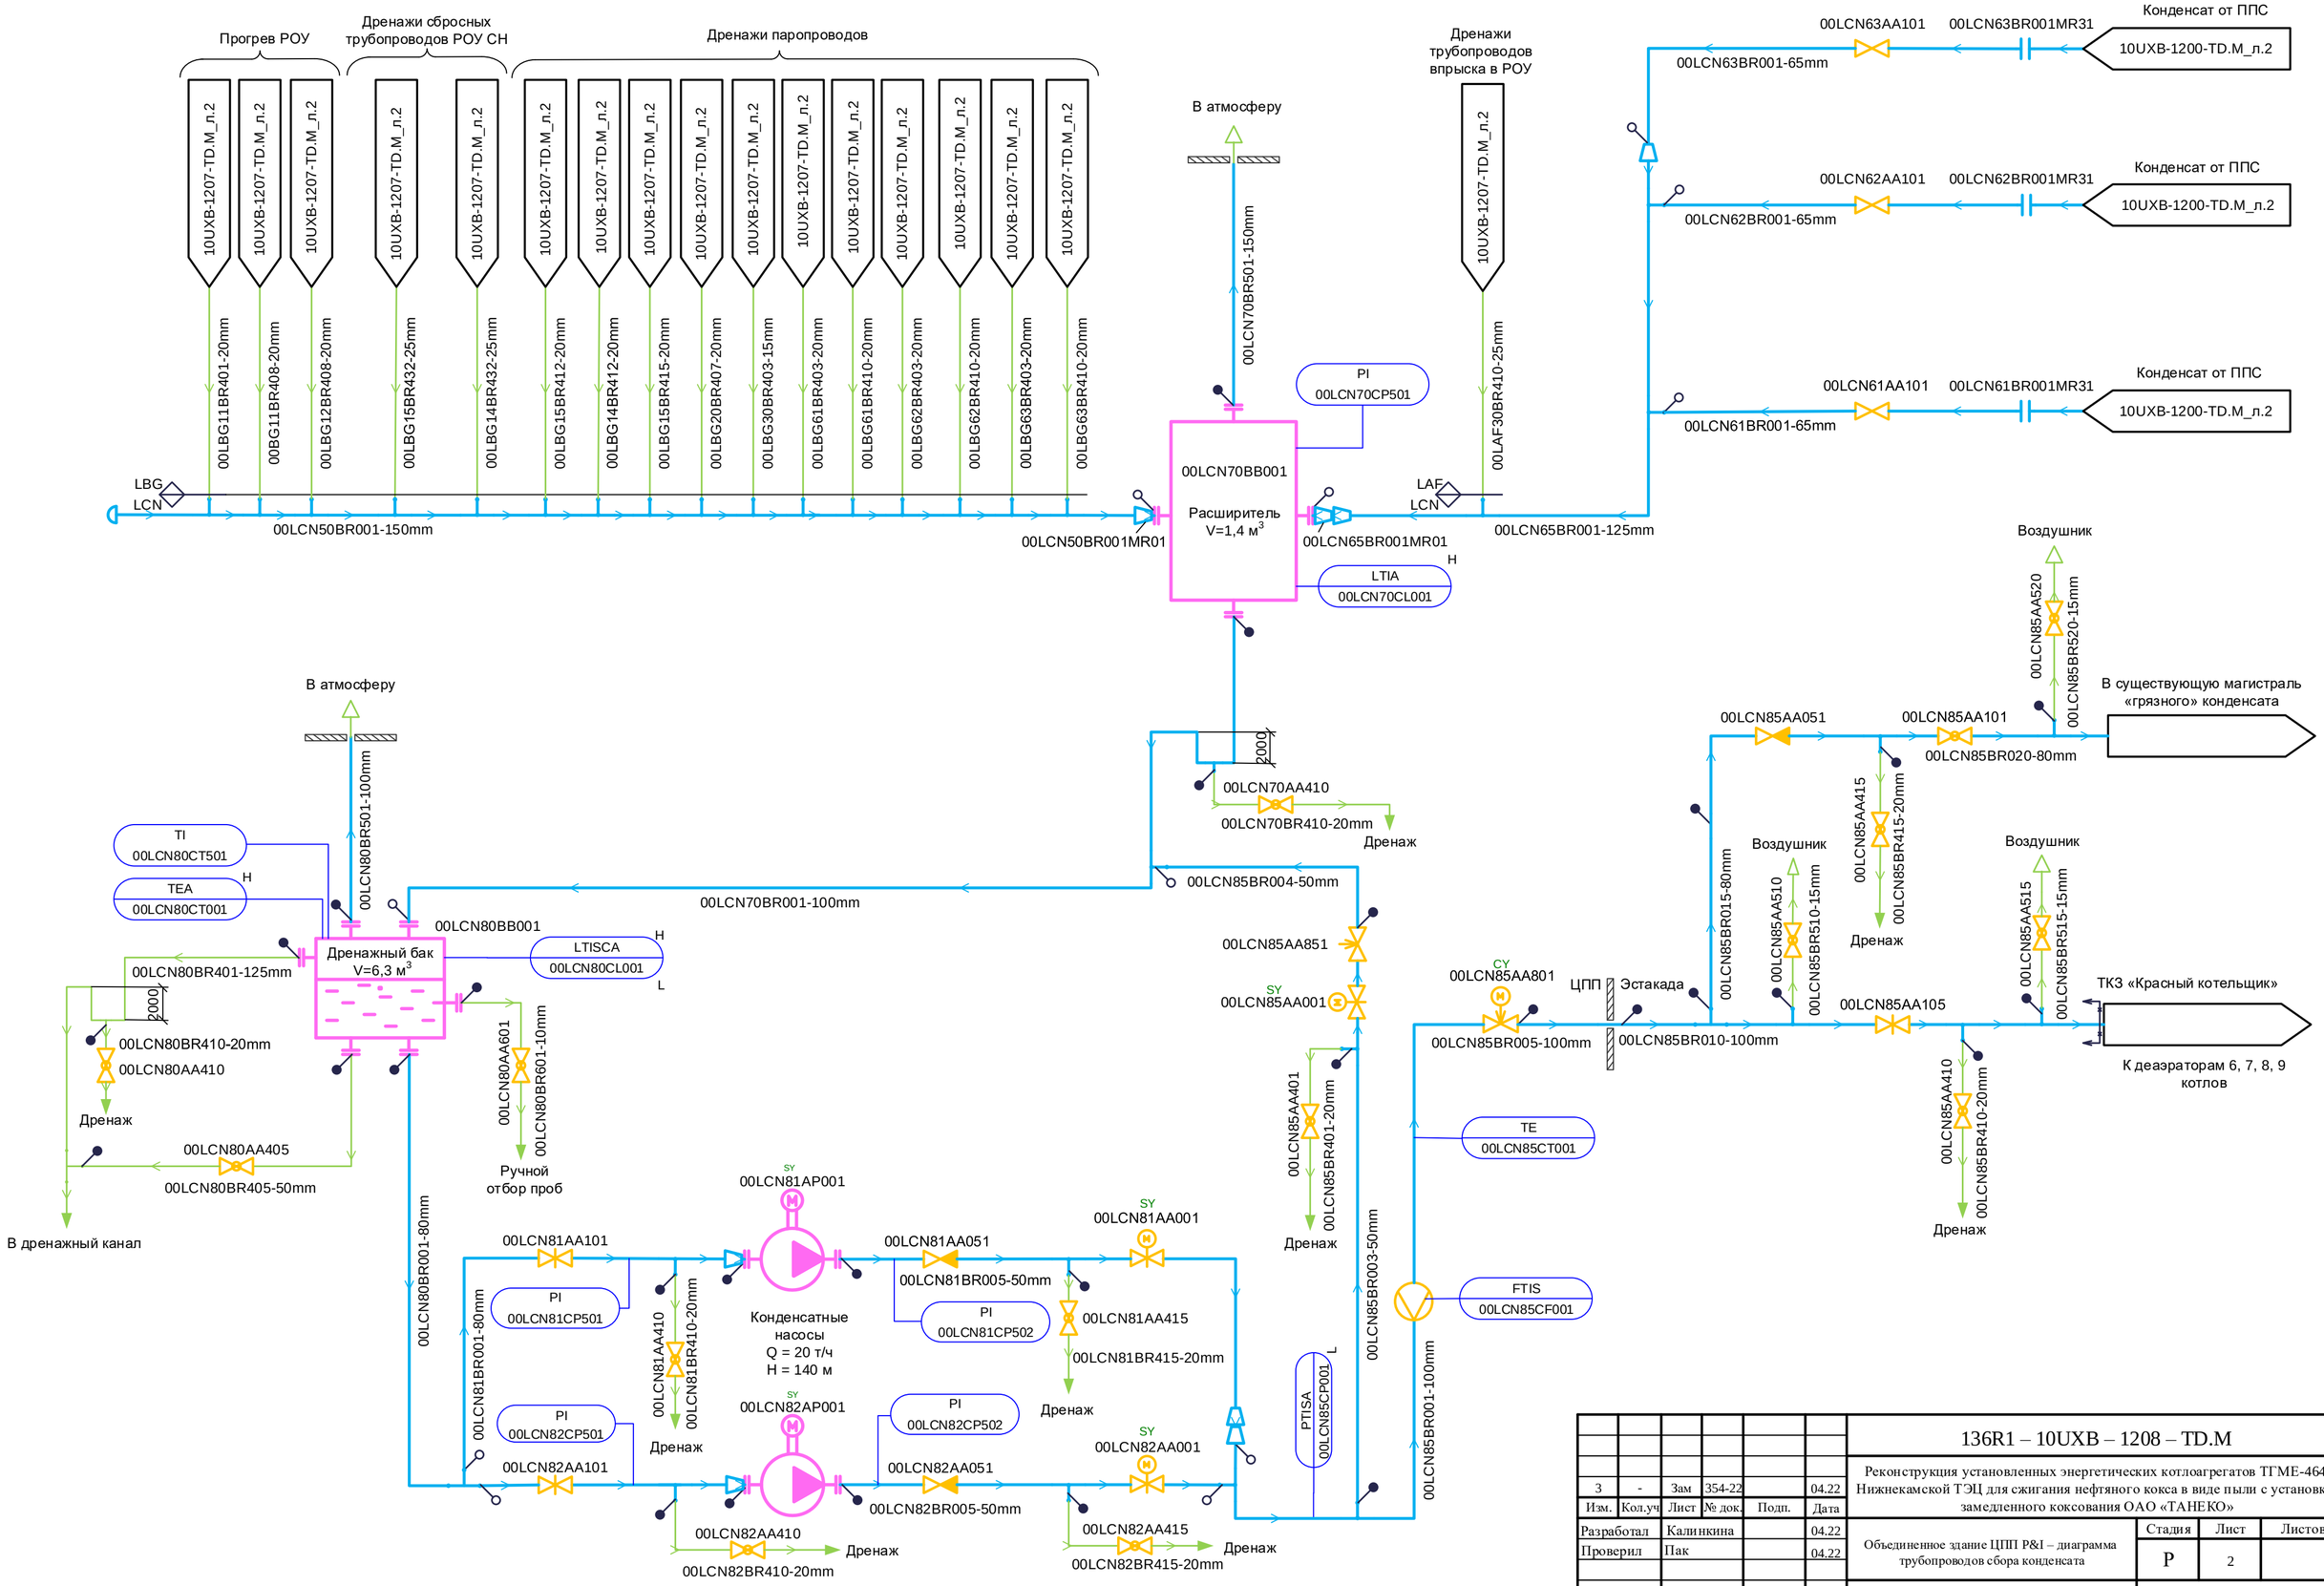

3	-	Зам	354-22		04.22	136R1 – 10UXB – 1208 – TD.M
Изм.	Кол.уч	Лист	№ док.	Подп.	Дата	Реконструкция установленных энергетических котлоагрегатов ТГМЕ-464 Нижнекамской ТЭЦ для сжигания нефтяного кокса в виде пыли с установки замедленного коксования ОАО «ТАНЕКО»
Разработал		Калинкина			04.22	Объединенное здание ЦПП P&I – диаграмма трубопроводов сбора конденсата
Проверил		Пак			04.22	Стадия: P; Лист: 2; Листов:
Н. контр.		Астраханцев			04.22	PI-диаграмма трубопроводов сбора конденсата. Система LCN

АКЦИОНЕРНОЕ ОБЩЕСТВО ИНСТИТУТ ТЕПЛОЭЛЕКТРОПРОЕКТ г. МОСКВА

Согласовано: ОАСУ Соболева 04.22

Взам. инв. № | Подпись и дата | Инв. № подл.

Формат А2