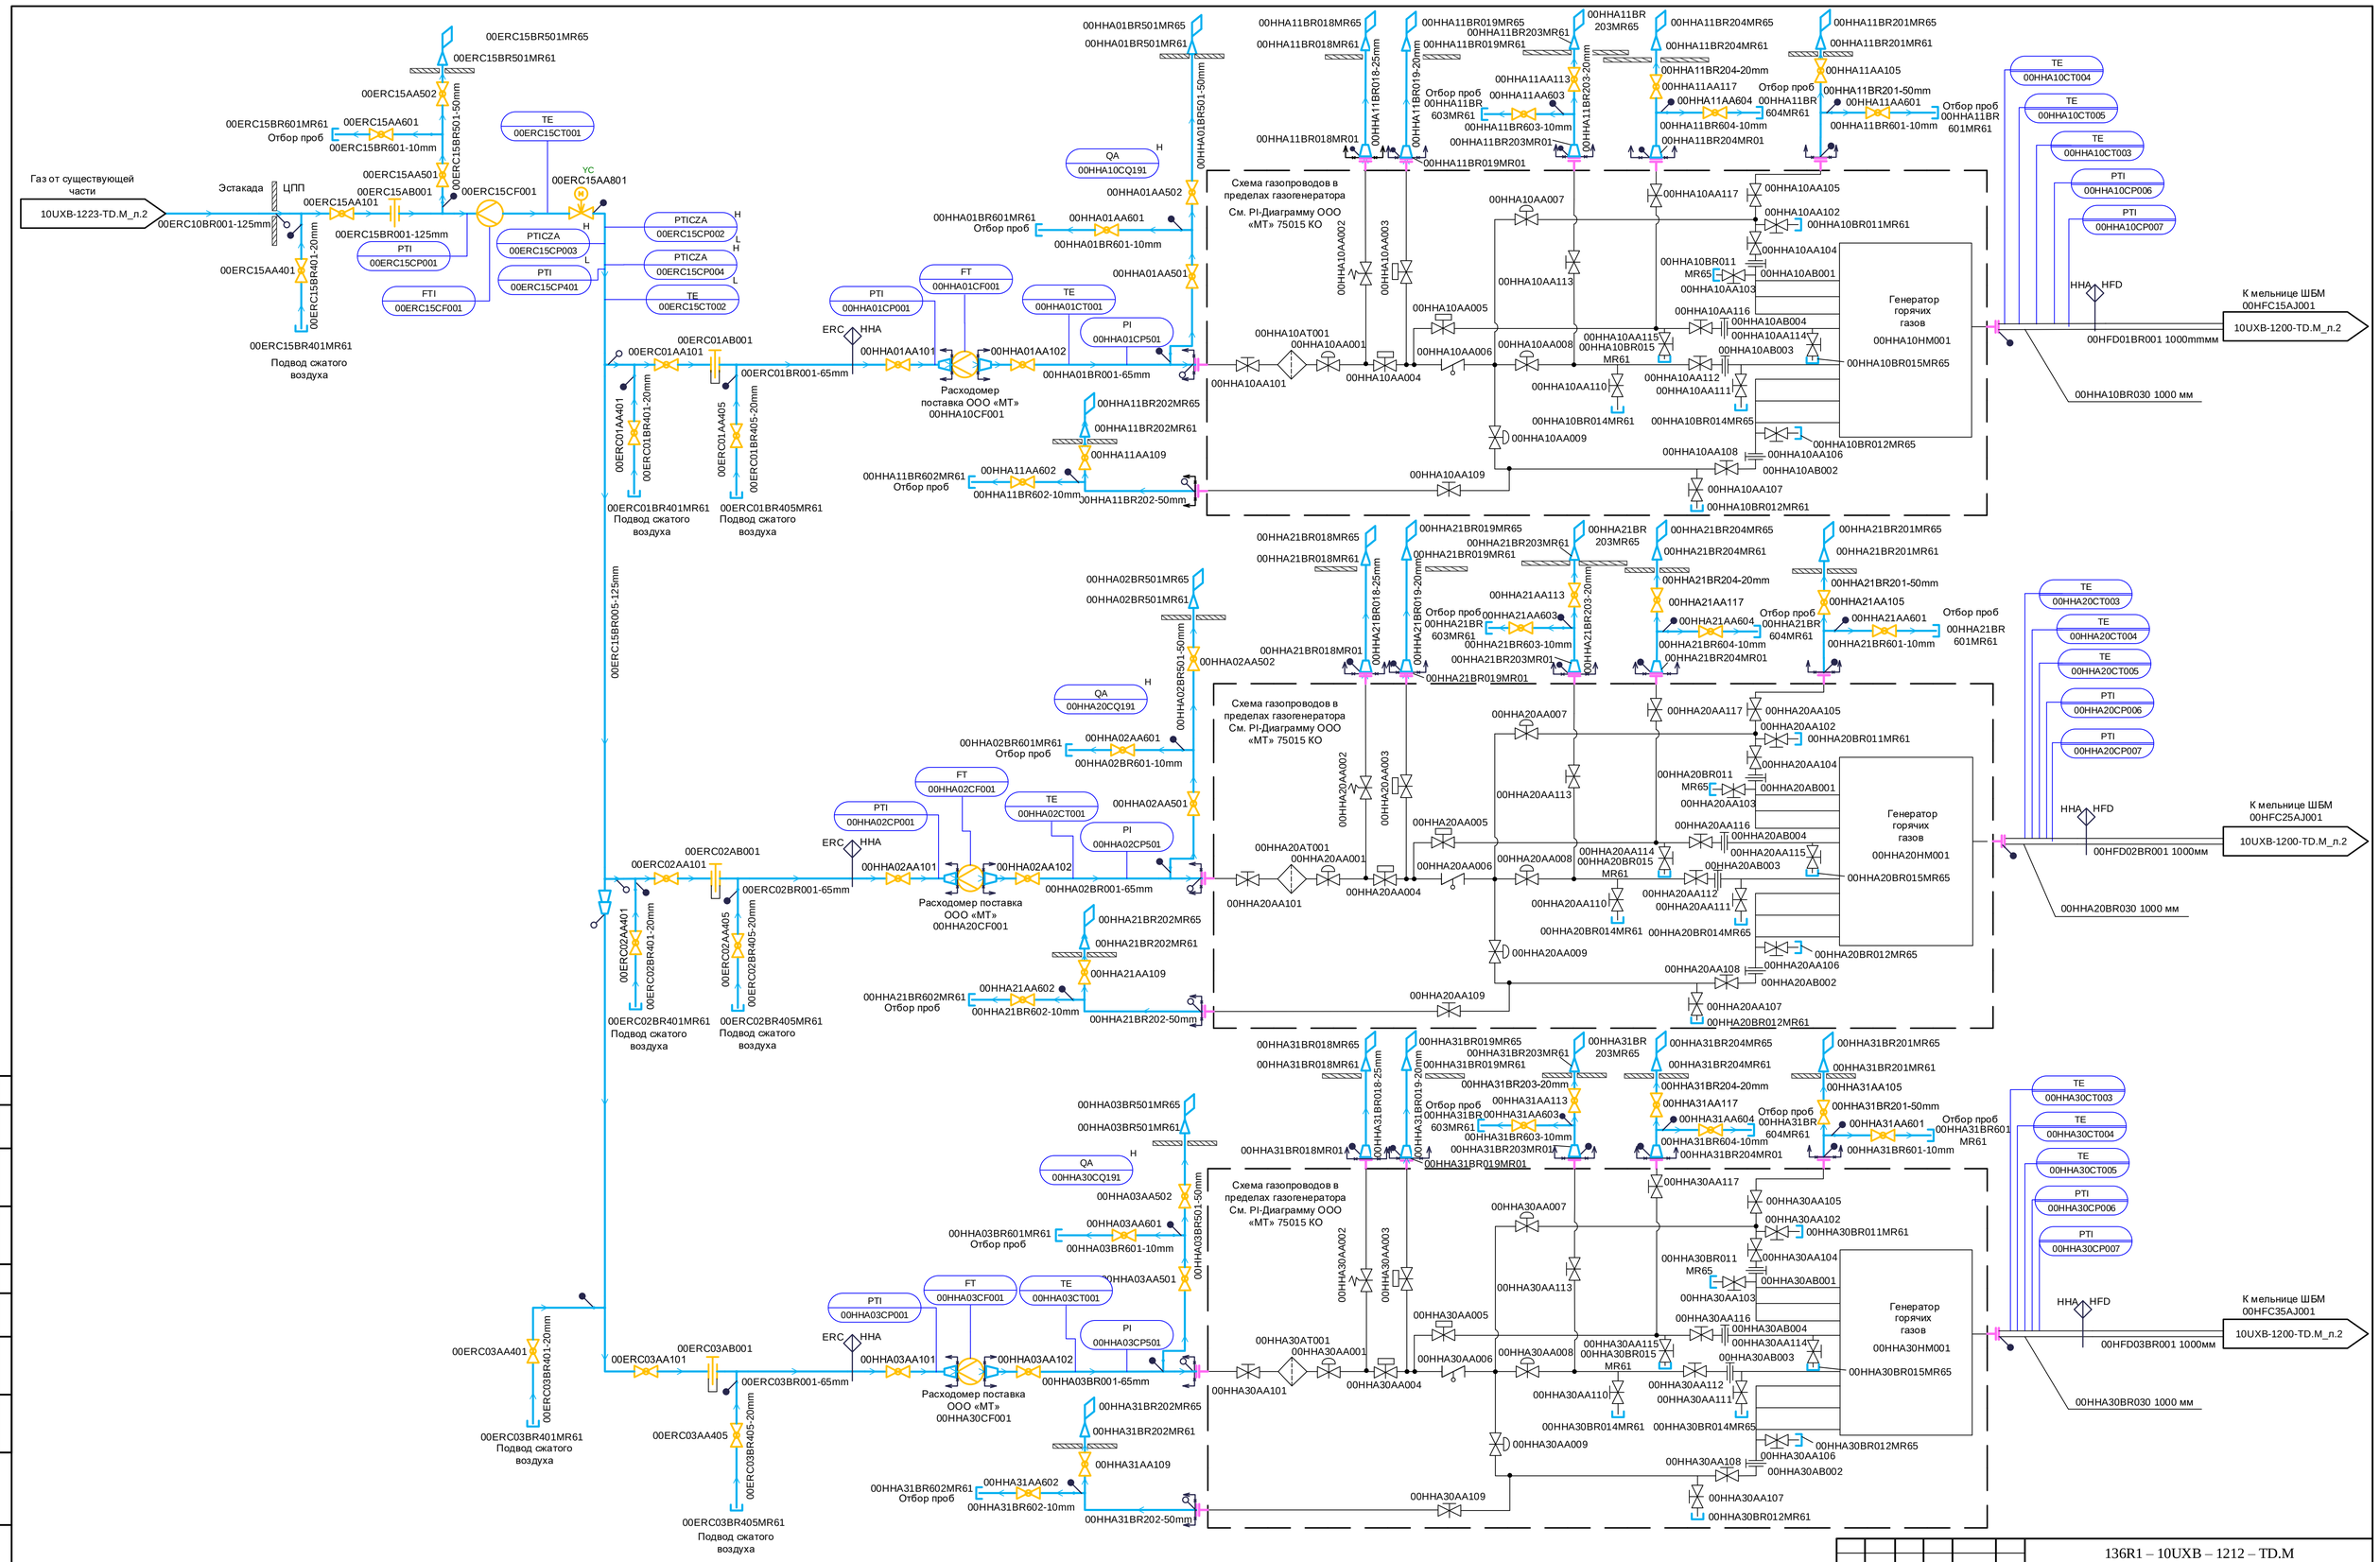

Примечание

Регулирующий клапан 00ERC15AA801 поддерживает давление после себя с заданием 0.08 МПа

4	-	Зам	1566-22			
Изм.	Кол.уч	Лист	№ док.	Подп.	Дата	
Разработал		Калинкина				
Проверил		Пак				
Н. контр.		Астраханцев				

136R1 – 10UXB – 1212 – TD.M

Реконструкция установленных энергетических котлоагрегатов ТГМЕ-464 Нижнекамской ТЭЦ для сжигания нефтяного кокса в виде пыли с установки замедленного коксования ОАО «ТАНЕКО»

Объединенное здание ЦПП P&I – диаграмма трубопроводов газового топлива в ЦПП

Стадия	Лист	Листов
Р	2	

PI-диаграмма трубопроводов подачи газа на ЦПП. Система ERC

АКЦИОНЕРНОЕ ОБЩЕСТВО ИНСТИТУТ ТЕПЛОЭЛЕКТРОПРОЕКТ Г. МОСКВА

Согласовано ОАСУ Соболева

Взам. инв. № | Подпись и дата | Инв. № подл.

Формат А1