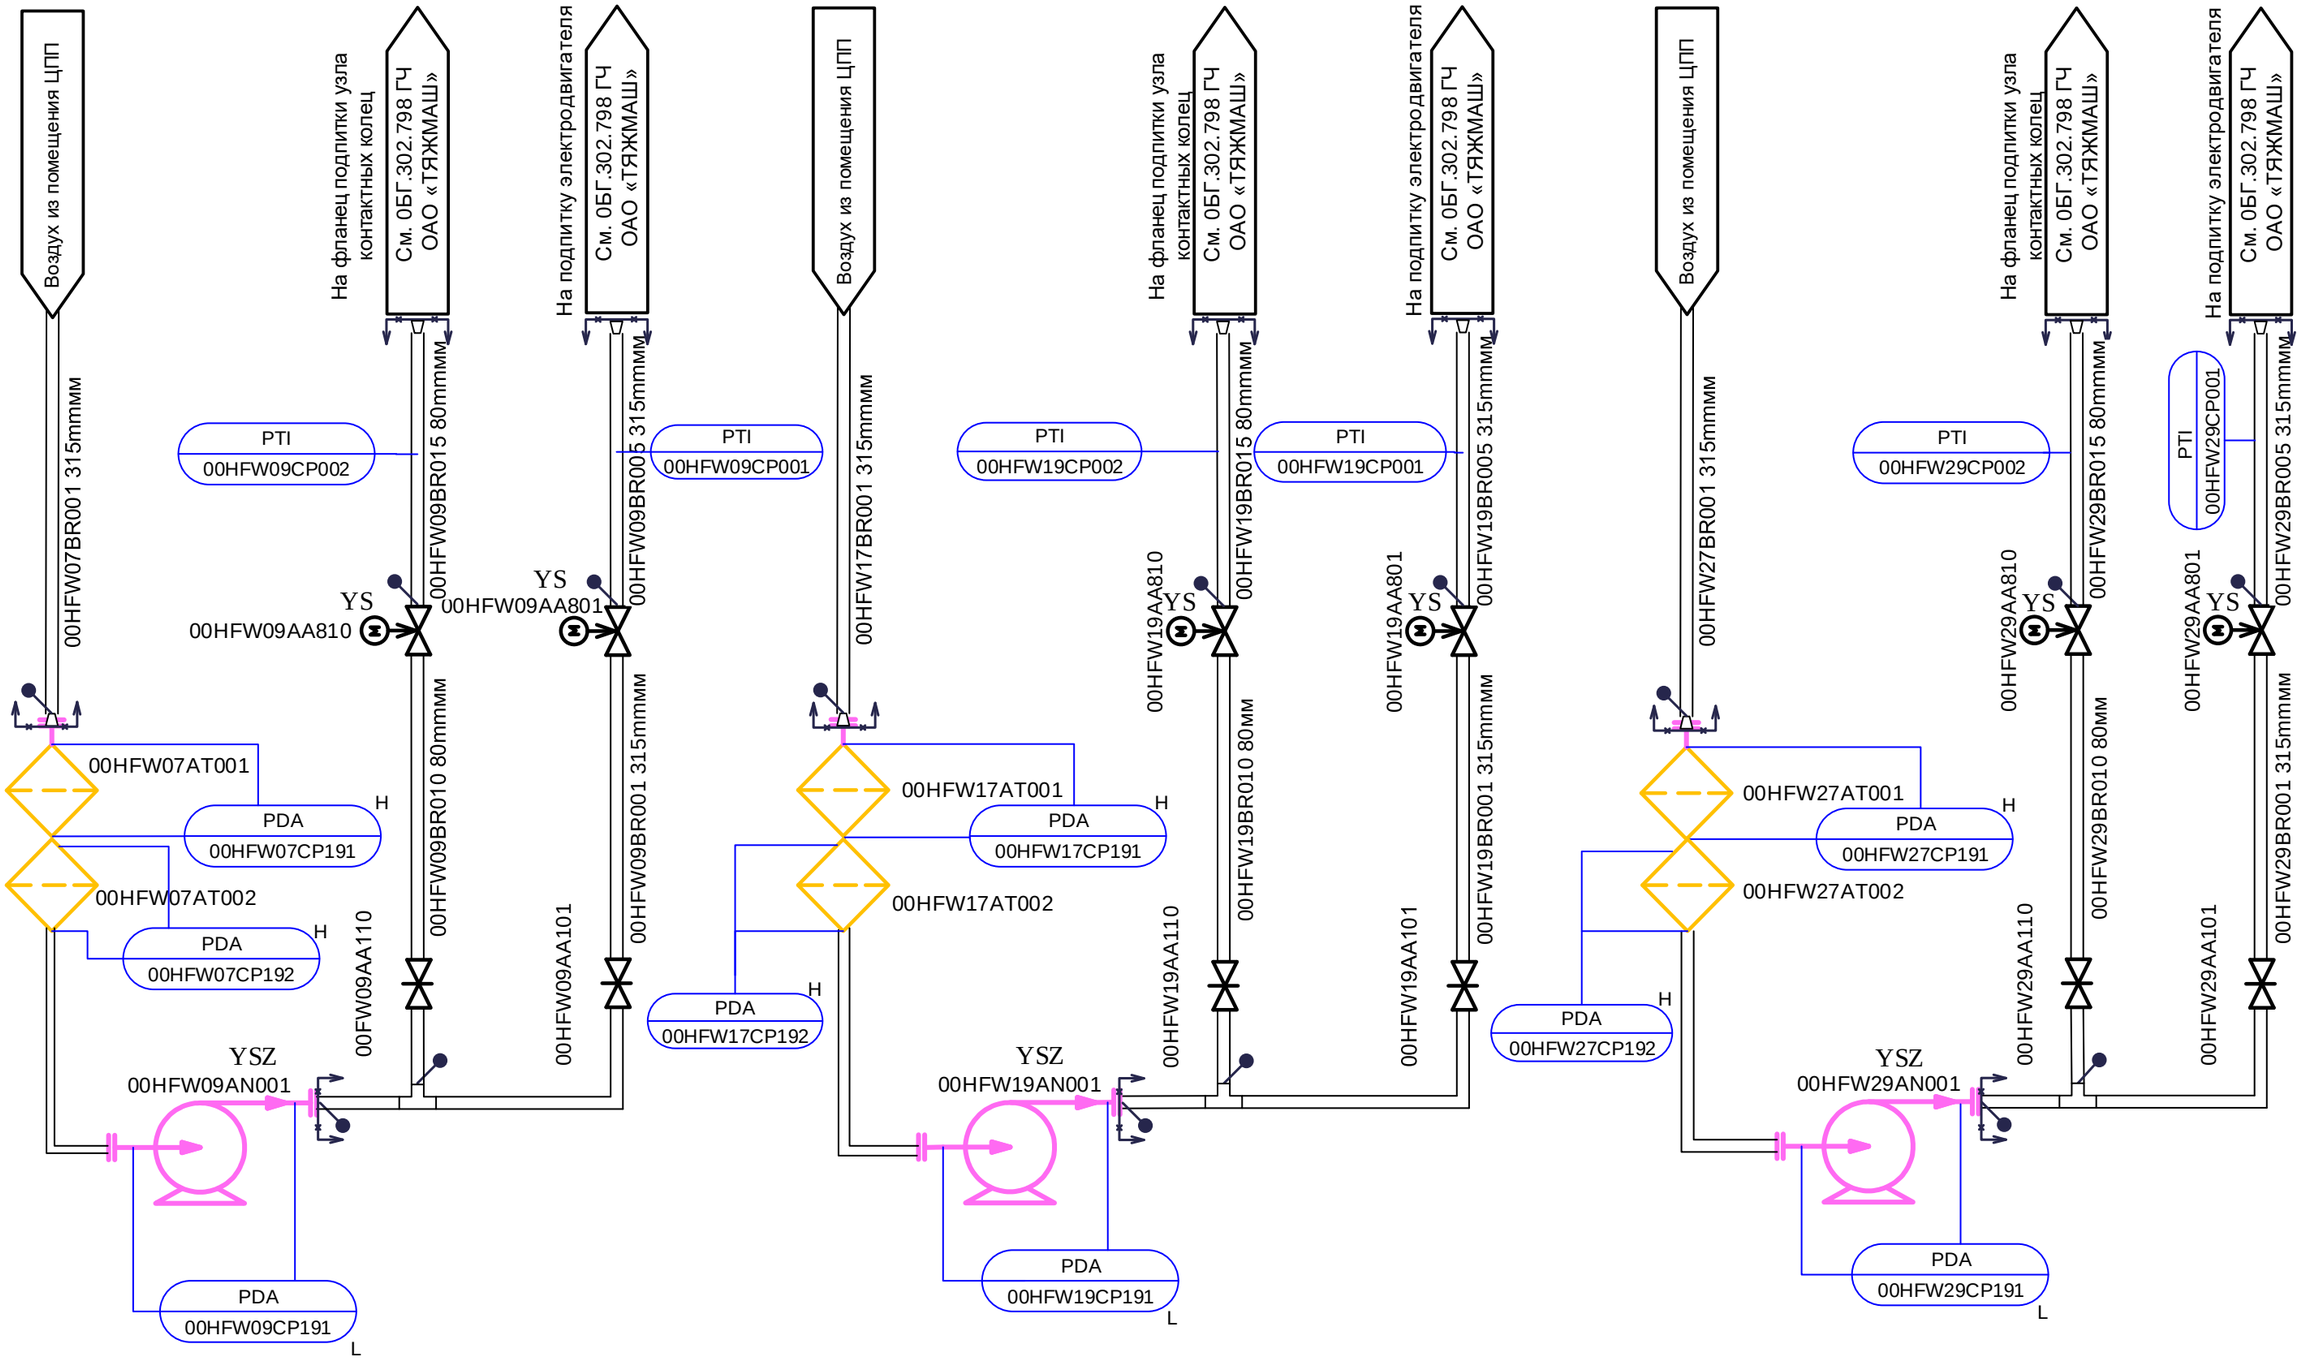

Согласовано

Взам. инв. №

Подпись и дата

Инв. № подл.

Изм.	Кол.уч	Лист	№ док.	Подп.	Дата
2	-	Зам	151-19		

Разработал	Пак Л.	
Проверил	Пак С.	
Н. контр.	Астраханцев	

136R1 – 10UXB – 1213 – TD.M

Реконструкция установленных энергетических котлоагрегатов ТГМЕ-464 Нижнекамской ТЭЦ для сжигания нефтяного кокса в виде пыли с установки замедленного коксования ОАО «ТАНЕКО»

Объединенное задание ЦПП P&I – диаграмма трубопроводов подвода воздуха системы подпитки двигателя мельницы.

Стадия	Лист	Листов
Р	2	

P&I-диаграмма трубопроводов подвода воздуха системы подпитки двигателя мельницы. Система HFW

АКЦИОНЕРНОЕ ОБЩЕСТВО ИНСТИТУТ ТЕПЛОЭЛЕКТРОПРОЕКТ Г. МОСКВА

Формат А3