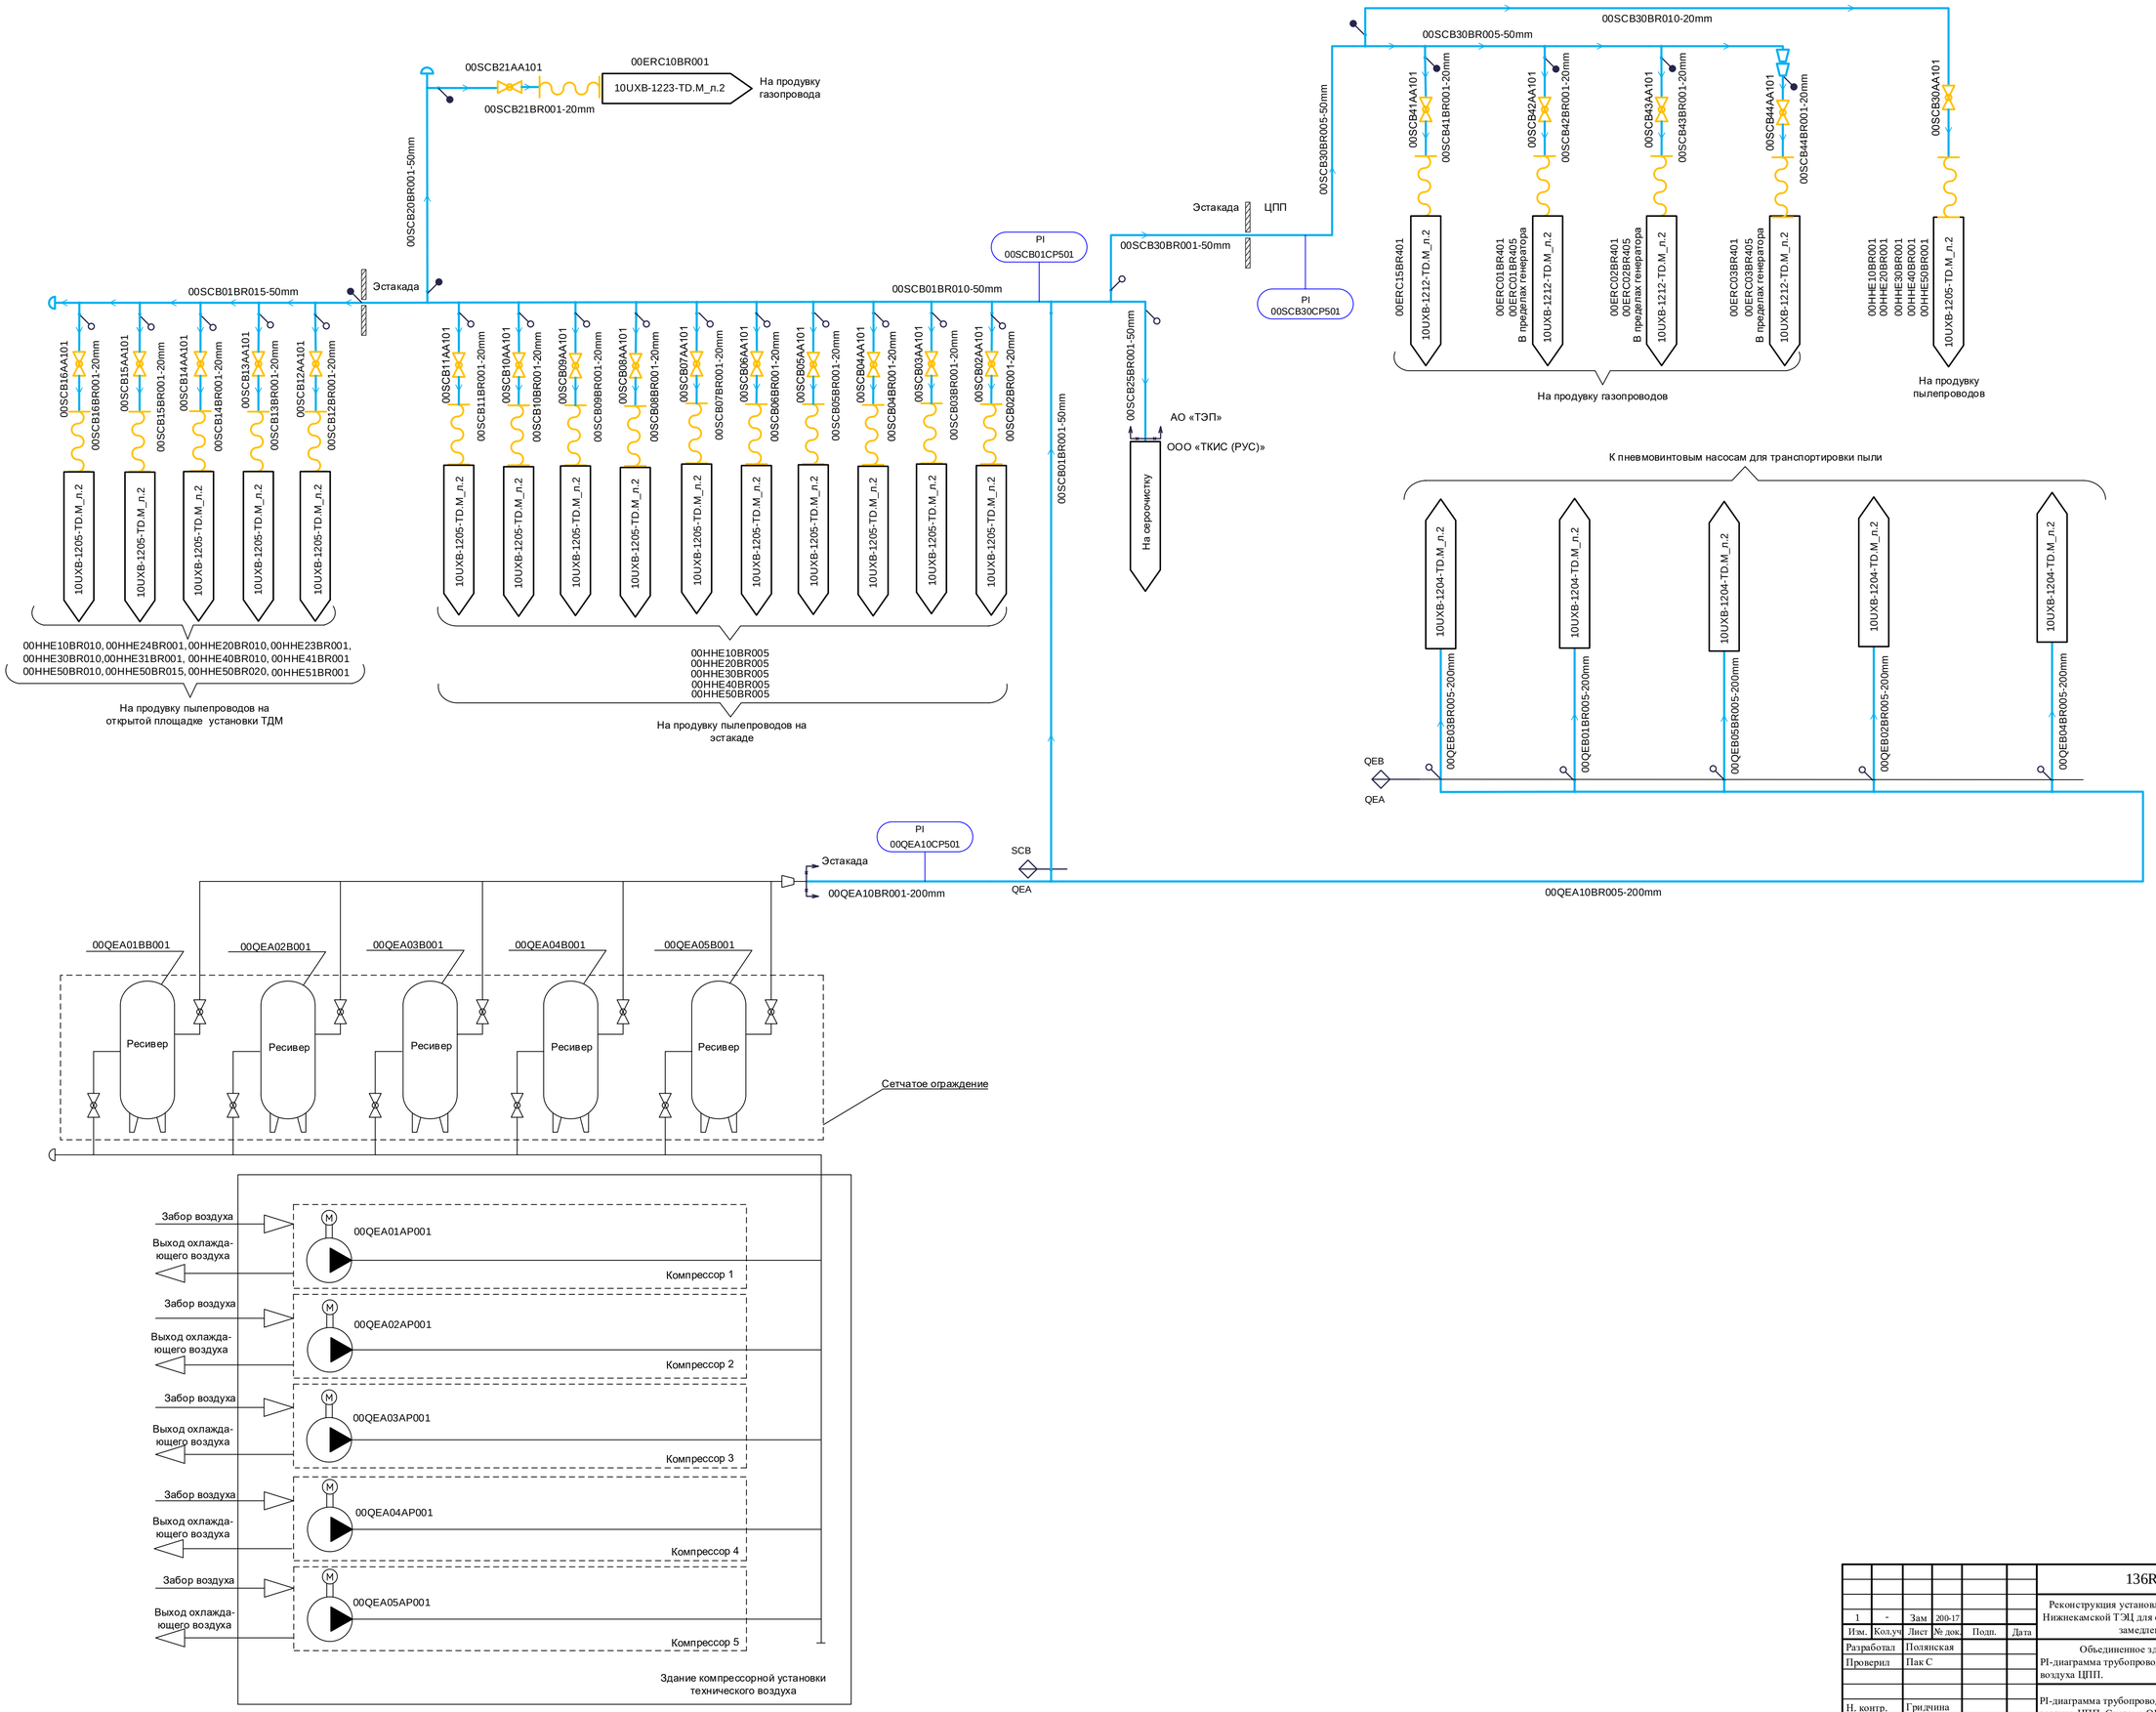

1	-	Зам	200-17			
Изм.	Кол.уч	Лист	№ док.	Подп.	Дата	

136R1 – 10UXB-1218-TD.M

Реконструкция установленных энергетических котлоагрегатов ТГМЕ-464 Нижнекамской ТЭЦ для сжигания нефтяного кокса в виде пыли с установки замедленного коксования ОАО "ТАНЕКО"

Разработал	Полянская	
Проверил	Пак С	
Н. контр.	Гридчина	

Объединенное здание ЦПП

PI-диаграмма трубопроводов технического воздуха ЦПП.

PI-диаграмма трубопроводов технического воздуха ЦПП. Система QEA, QEB, SCB

Стадия	Лист	Листов
Р	2	

АКЦИОНЕРНОЕ ОБЩЕСТВО ИНСТИТУТ ТЕПЛОЭЛЕКТРОПРОЕКТ г. МОСКВА

Согласовано

ОАСУ Соболева

Взам. инв. №

Подпись и дата

Инв. № подл.

Формат А1