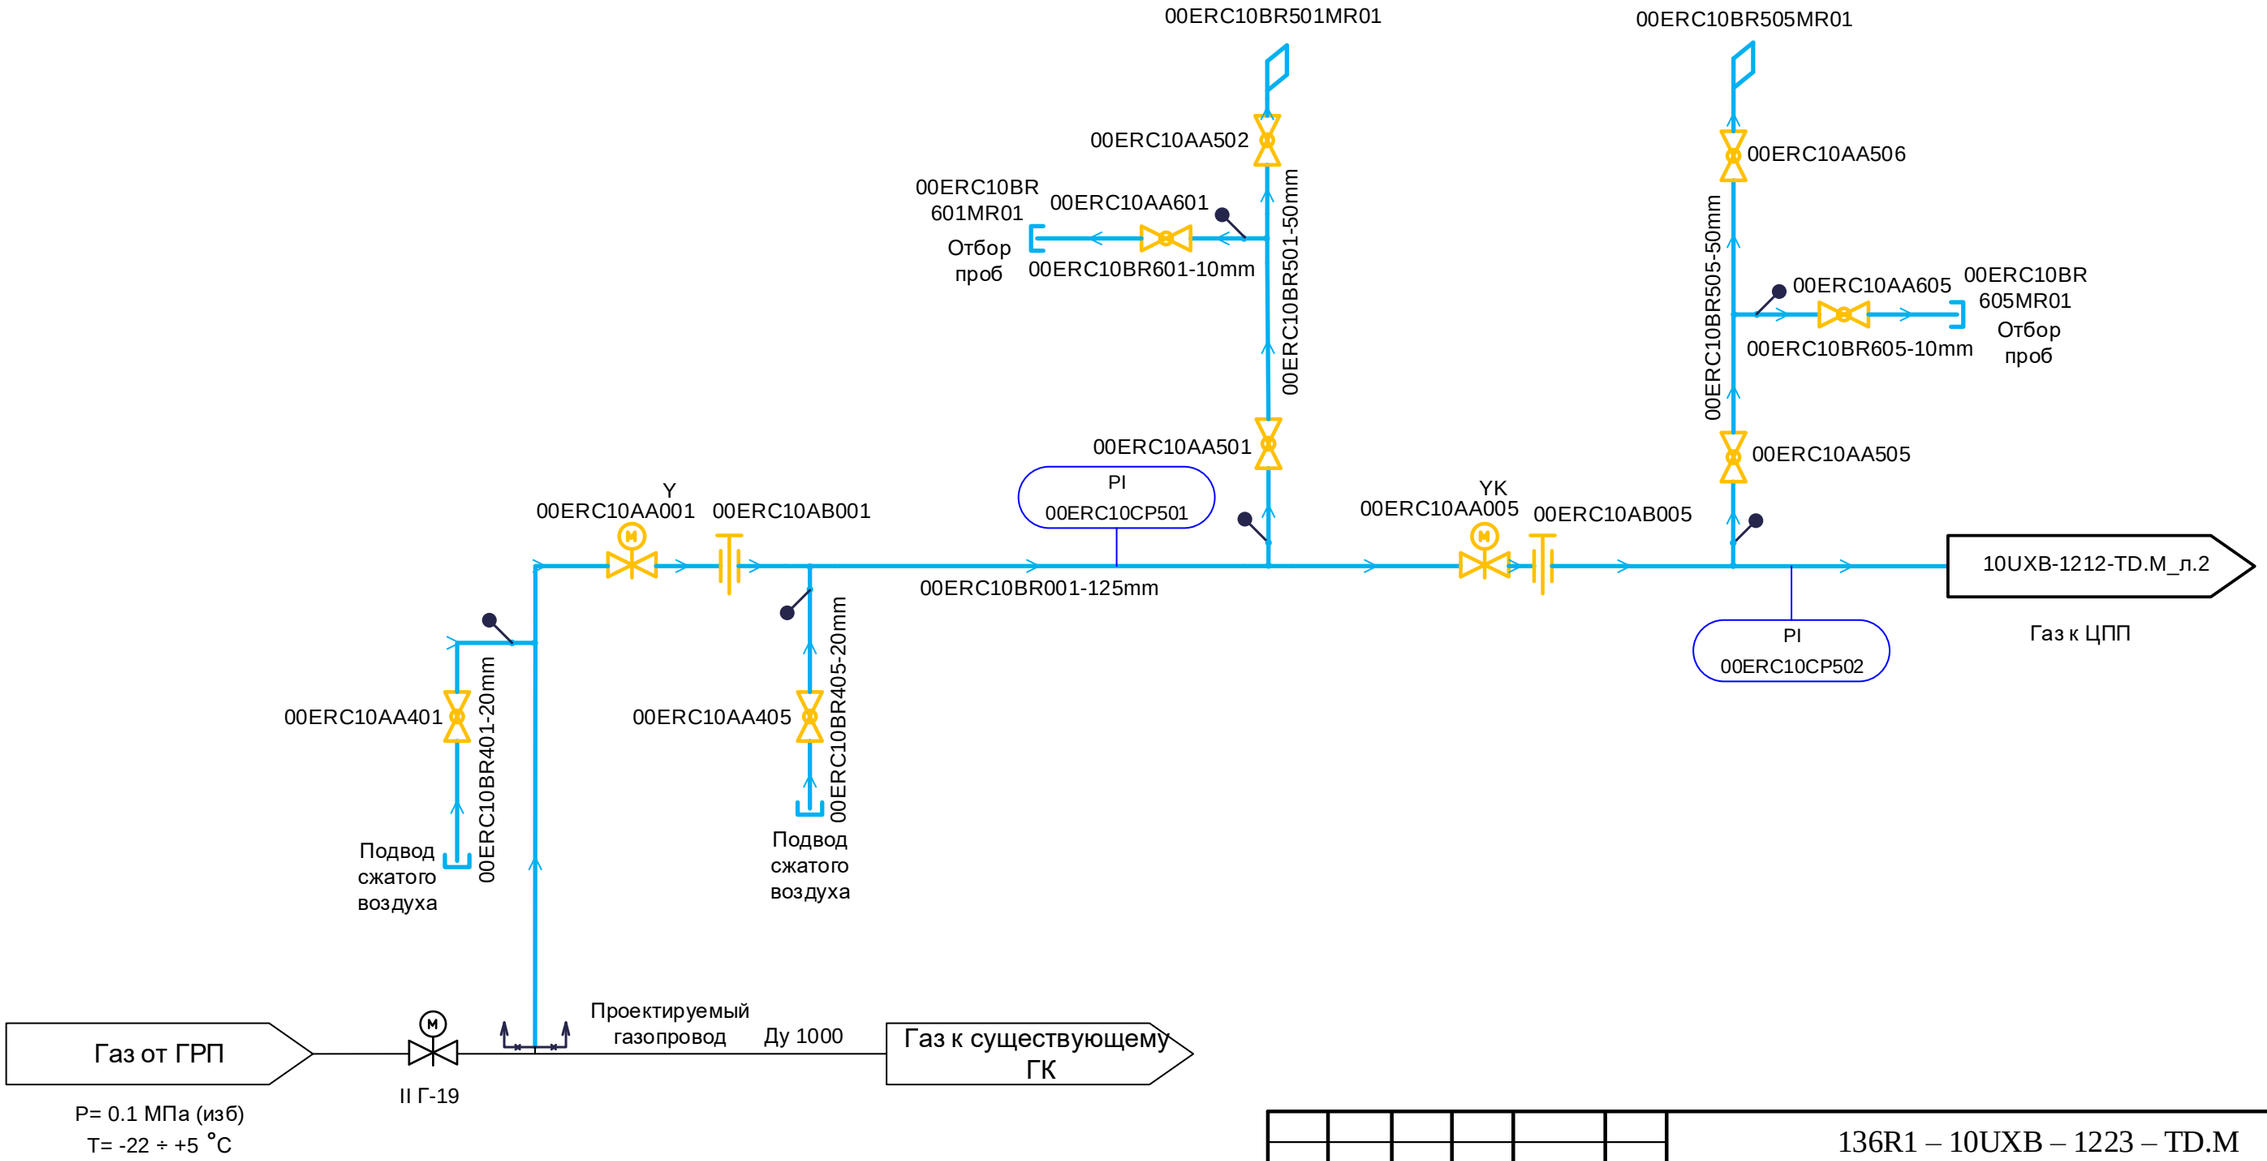

Согласовано

Взам. инв. №

Подпись и дата

Инв. № подл.

1	-	Зам	191-17			
Изм.	Кол.уч	Лист	№ док.	Подп.	Дата	
Разработал		Кудрявцев				
Проверил		Пак С.				
Н. контр.		Астраханцев				

136R1 – 10UXB – 1223 – TD.M

Реконструкция установленных энергетических котлоагрегатов ТГМЕ-464 Нижнекамской ТЭЦ для сжигания нефтяного кокса в виде пыли с установки замедленного коксования ОАО «ТАНЕКО»

Объединенное здание ЦПП P&I – диаграмма трубопроводов подачи газового топлива от существующей части на ЦПП

Стадия	Лист	Листов
Р	2	

PI-диаграмма трубопроводов подачи газа от существующей части. Система ERC

АКЦИОНЕРНОЕ ОБЩЕСТВО ИНСТИТУТ ТЕПЛОЭЛЕКТРОПРОЕКТ Г. МОСКВА

Формат А3