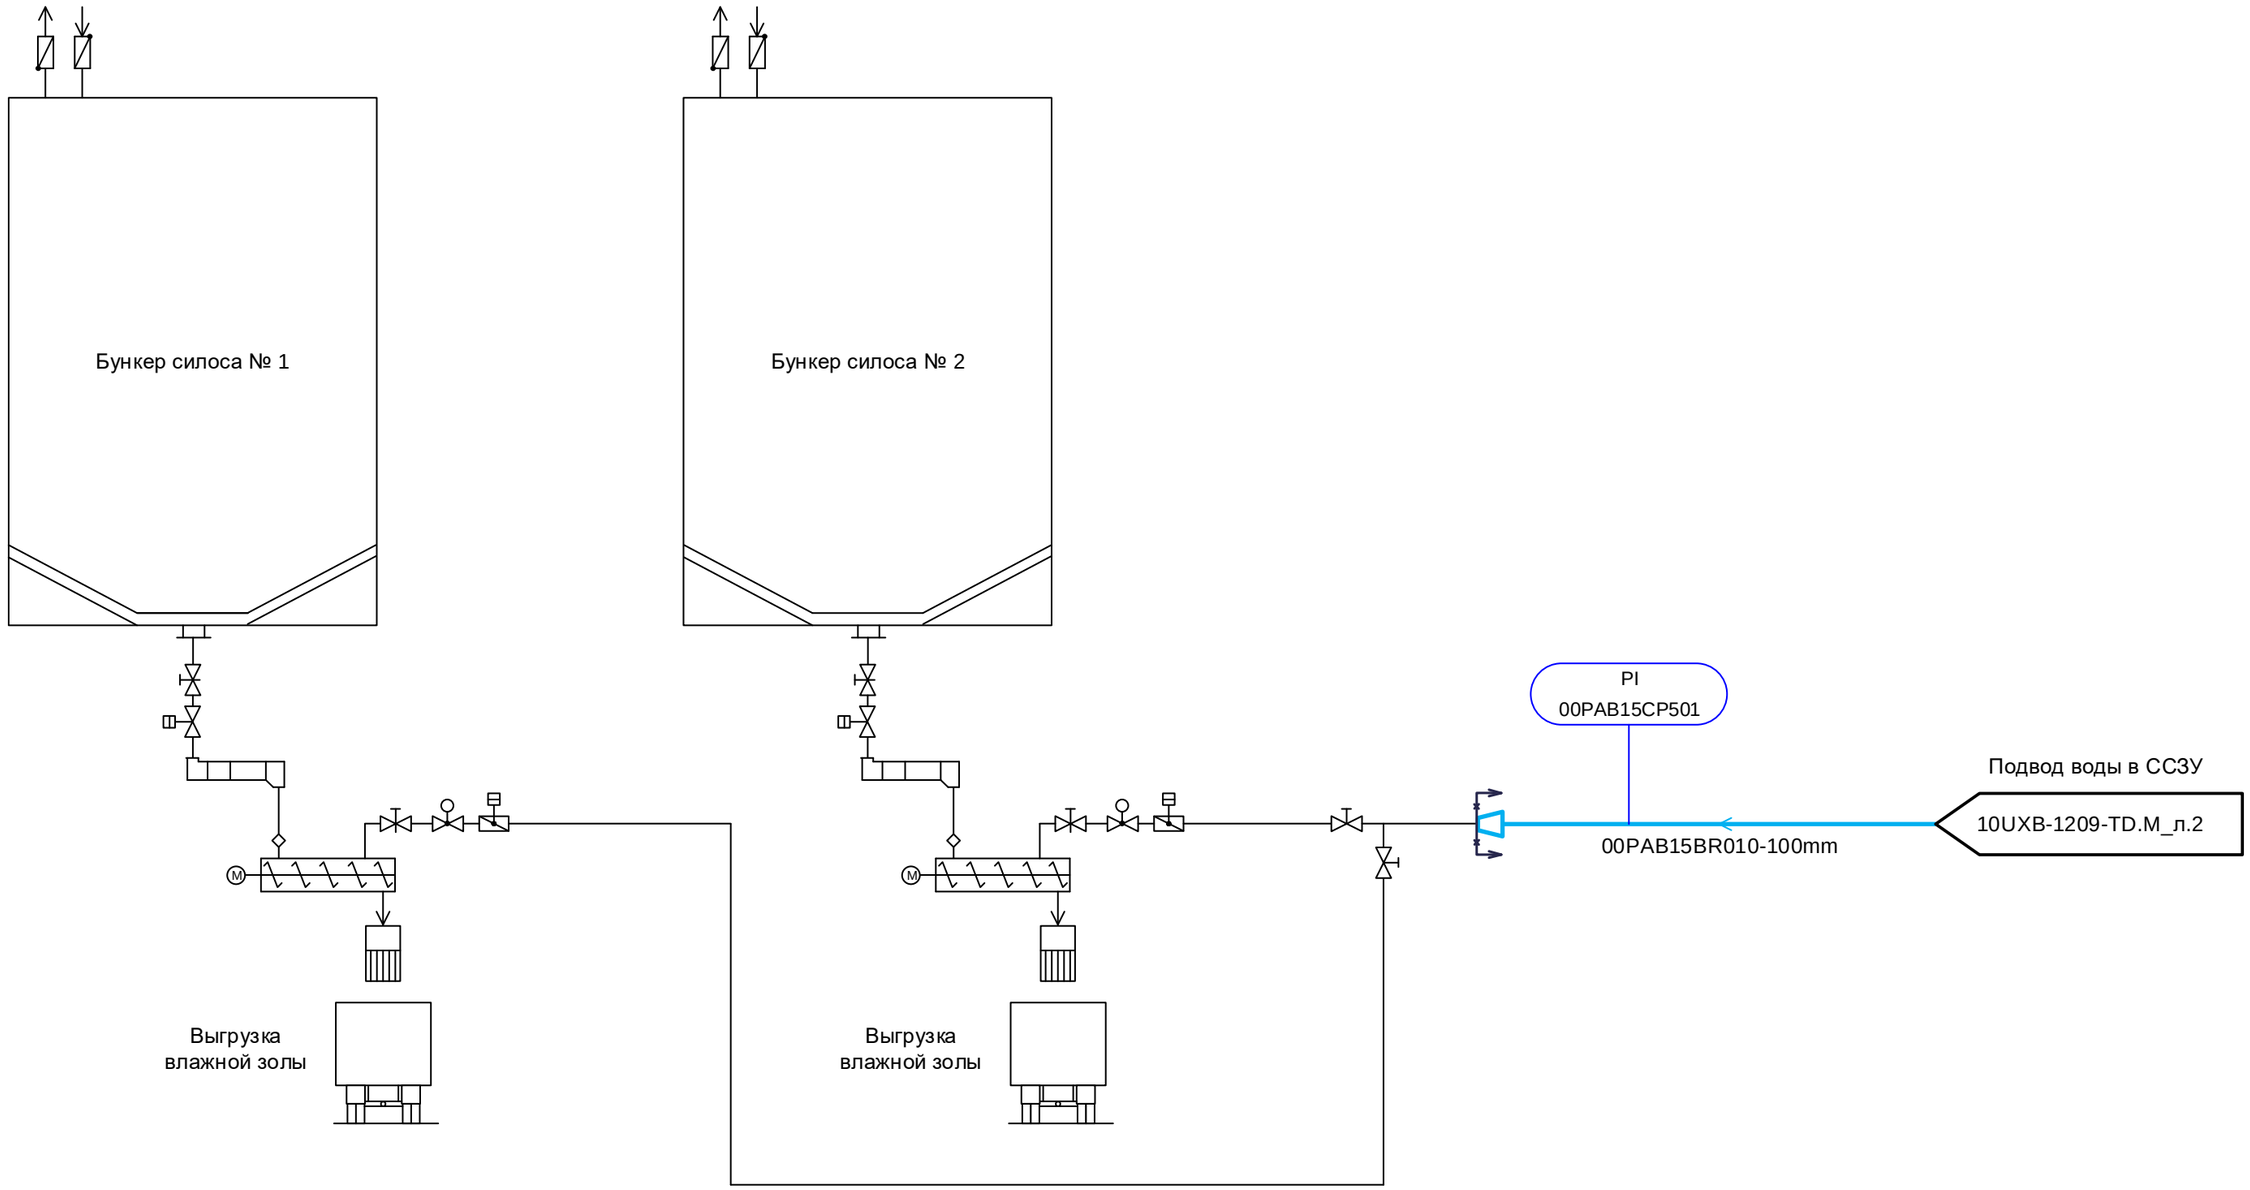

Согласовано

Разюпин

ОАСУ

Взам. инв. №

Подпись и дата

Инв. № подл.

Изм.	Кол.уч	Лист	№ док.	Подп.	Дата
Разработал		Пак Л.			
Проверил		Пак С.			
Н. контр.		Астраханцев			

136R1 – 10UXB – 1224 – TD.M

Реконструкция установленных энергетических котлоагрегатов ТГМЕ-464 Нижнекамской ТЭЦ для сжигания нефтяного кокса в виде пыли с установки замедленного коксования ОАО «ТАНЕКО»

Объединенное здание ЦПП. P&I – диаграмма трубопроводов охлаждающей воды на вспомогательные механизмы ССЗУ

Стадия	Лист	Листов
Р	2	

PI-Диаграмма трубопроводов охлаждающей воды на вспомогательные механизмы ССЗУ. Система РАВ.

АКЦИОНЕРНОЕ ОБЩЕСТВО ИНСТИТУТ ТЕПЛОЭЛЕКТРОПРОЕКТ Г. МОСКВА

Формат А3