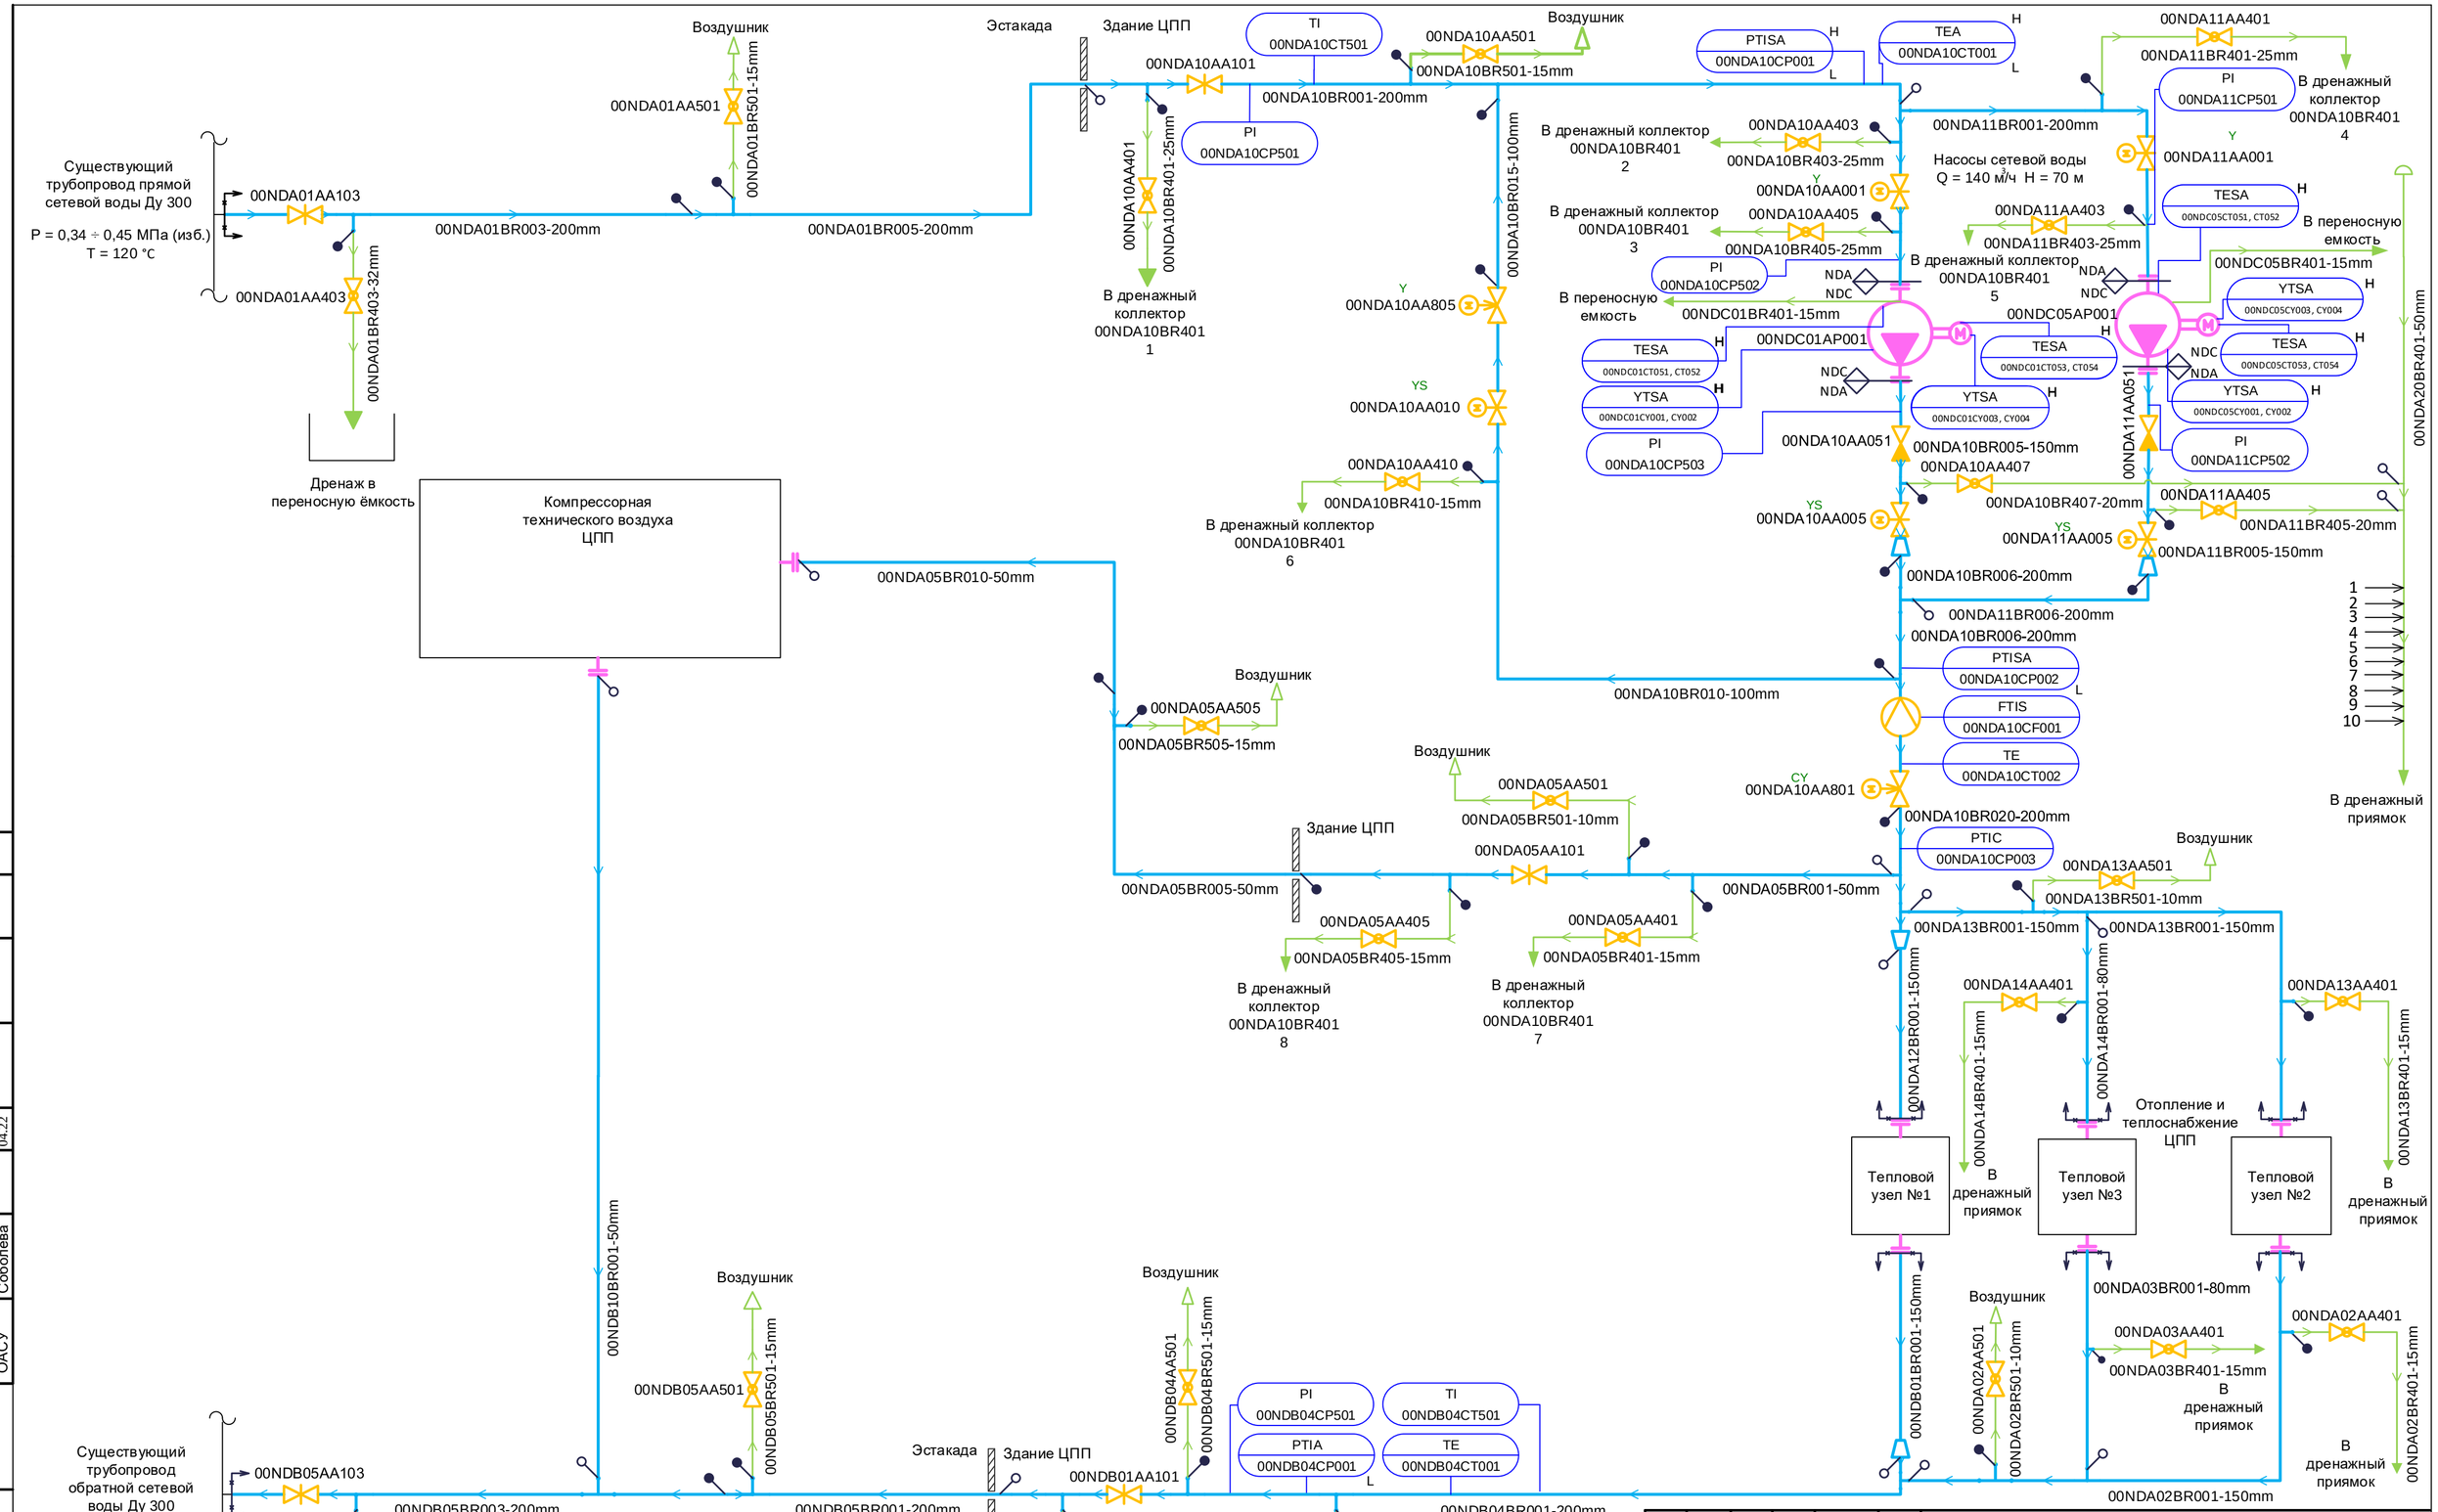

3	-	Зам.	354-22		04.22	
Изм.	Кол.уч	Лист	№ док.	Подп.	Дата	
Разработал		Калинкина			04.22	
Проверил		Пак			04.22	
Н. контр.		Астраханцев			04.22	

136R1 – 10UXB – 1226 – TD.M

Реконструкция установленных энергетических котлоагрегатов ТГМЕ-464 Нижнекамской ТЭЦ для сжигания нефтяного кокса в виде пыли с установки замедленного коксования ОАО «ТАНЕКО»

Объединенное здание ЦПП. P&I-диаграмма трубопроводов сетевой воды

Стадия	Лист	Листов
Р	2	

P&I-диаграмма трубопроводов сетевой воды. Система NDA, NDB, NDC

ОТКРЫТОЕ АКЦИОНЕРНОЕ ОБЩЕСТВО ИНСТИТУТ ТЕПЛОЭЛЕКТРОПРОЕКТ МОСКВА

Согласовано

ОАСУ Соболева 04.22

Взам. инв. №

Подпись и дата

Инв. № подл.

Формат А2