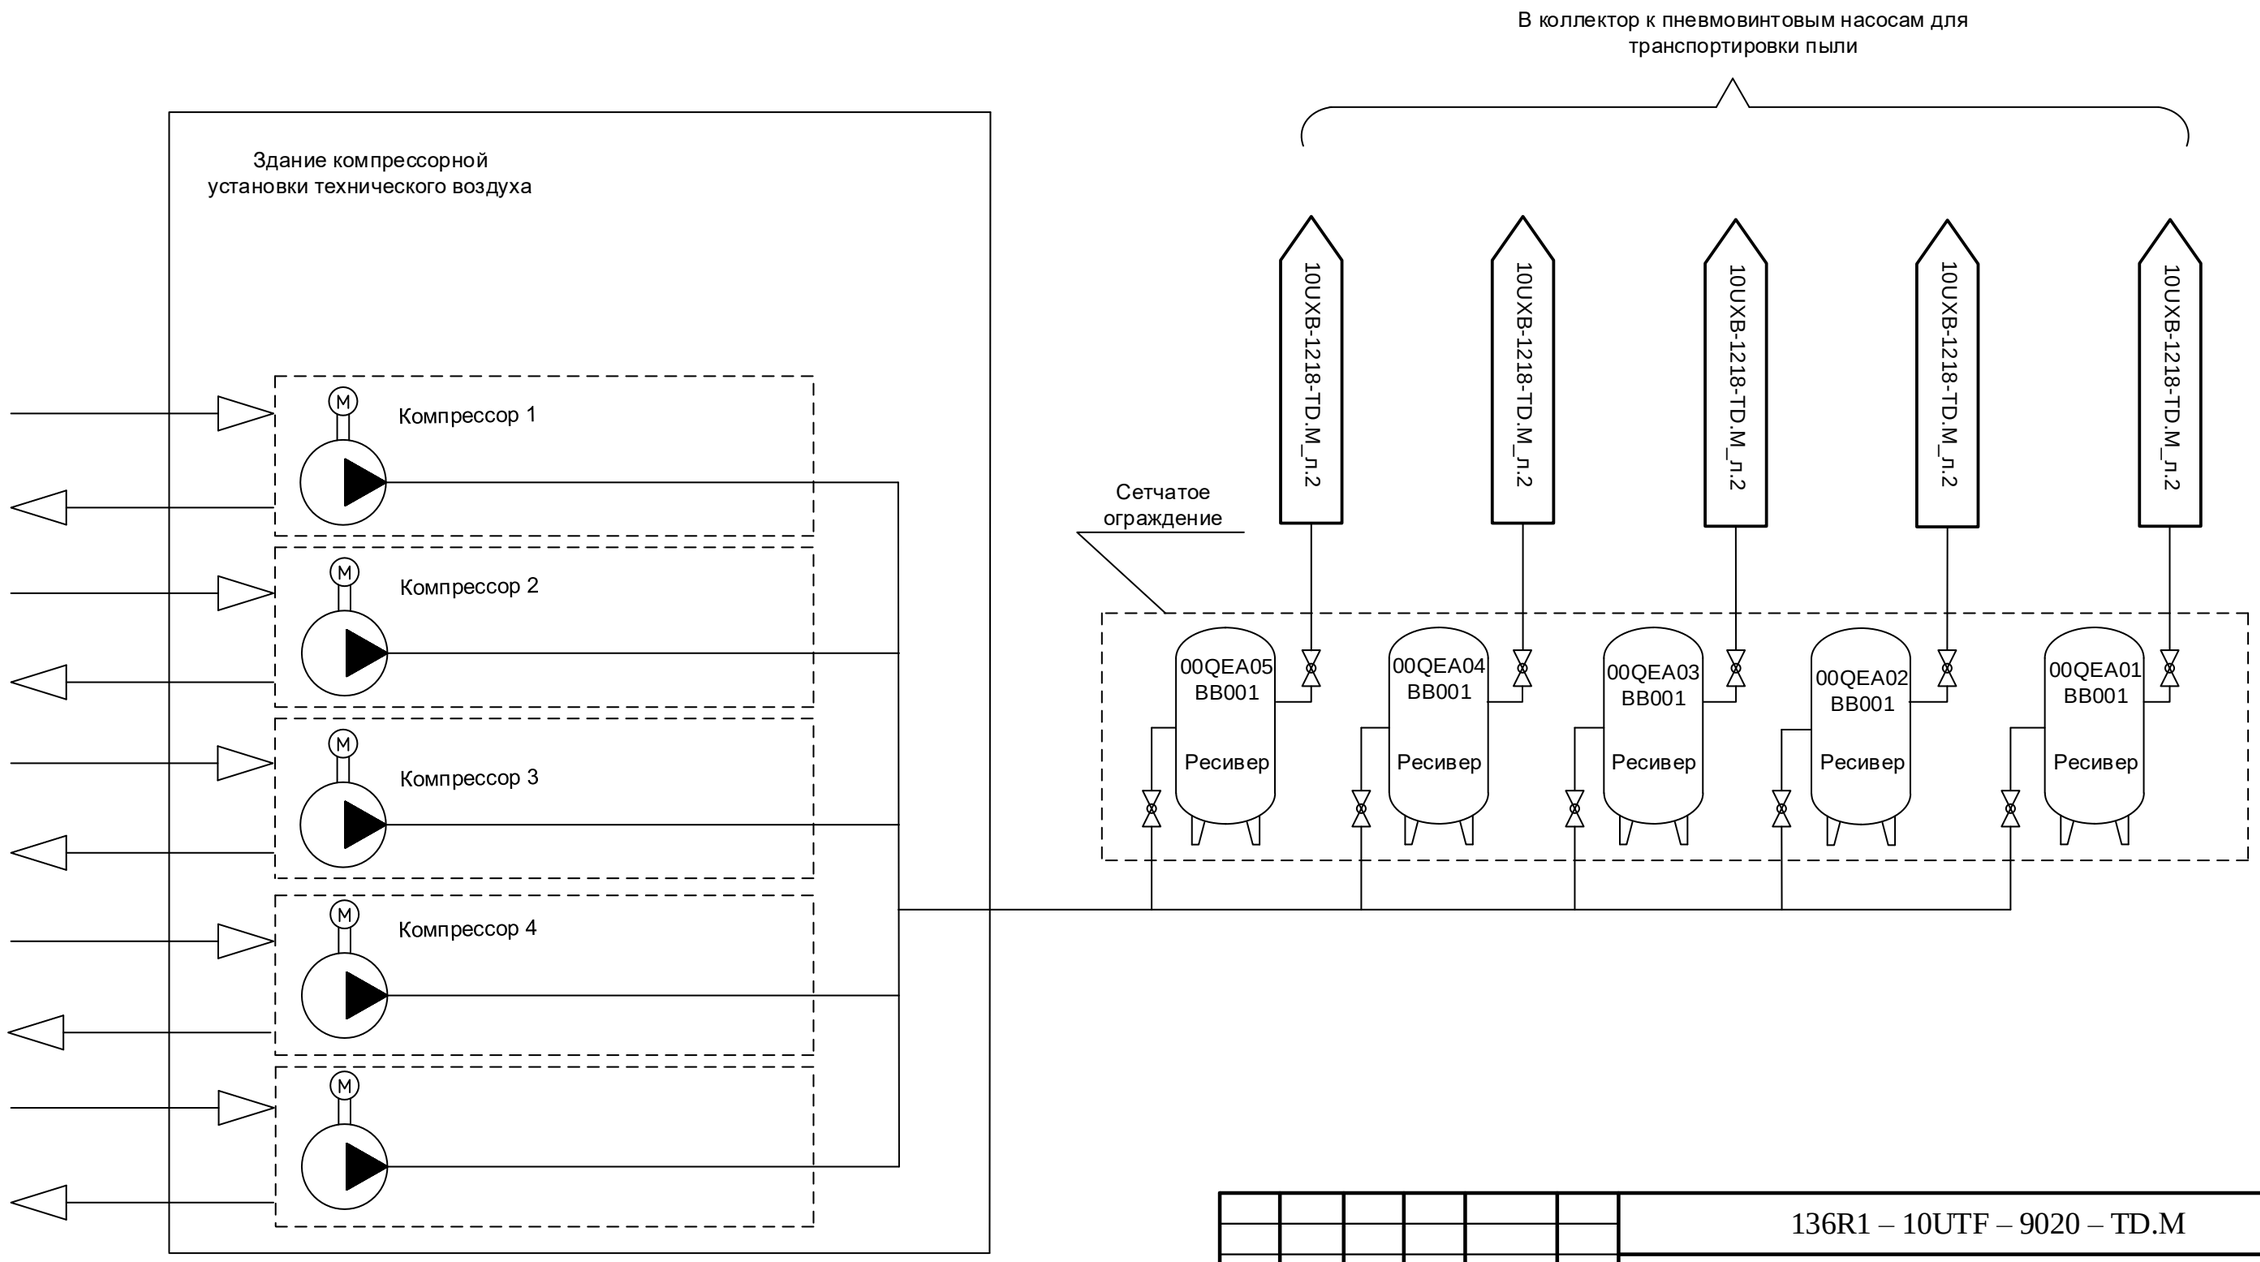

Согласовано

ОАСУ

Взам. инв. №

Подпись и дата

Инв. № подл.

Изм.	Кол.уч	Лист	№ док.	Подп.	Дата
Разработал		Полянская			
Проверил		Пак			
Н. контр.		Астраханцев			

136R1 – 10UTF – 9020 – TD.M

Реконструкция установленных энергетических котлоагрегатов ТГМЕ-464 Нижнекамской ТЭЦ для сжигания нефтяного кокса в виде пыли с установки замедленного коксования ОАО “ТАНЕКО”

Компрессорная технического воздуха (ЦПП). Технологические трубопроводы. PI-диаграмма.

Стадия	Лист	Листов
Р	2	

PI-диаграмма трубопроводов технического воздуха. Система QEA.

АКЦИОНЕРНОЕ ОБЩЕСТВО ИНСТИТУТ ТЕПЛОЭЛЕКТРОПРОЕКТ Г. МОСКВА

Формат А3