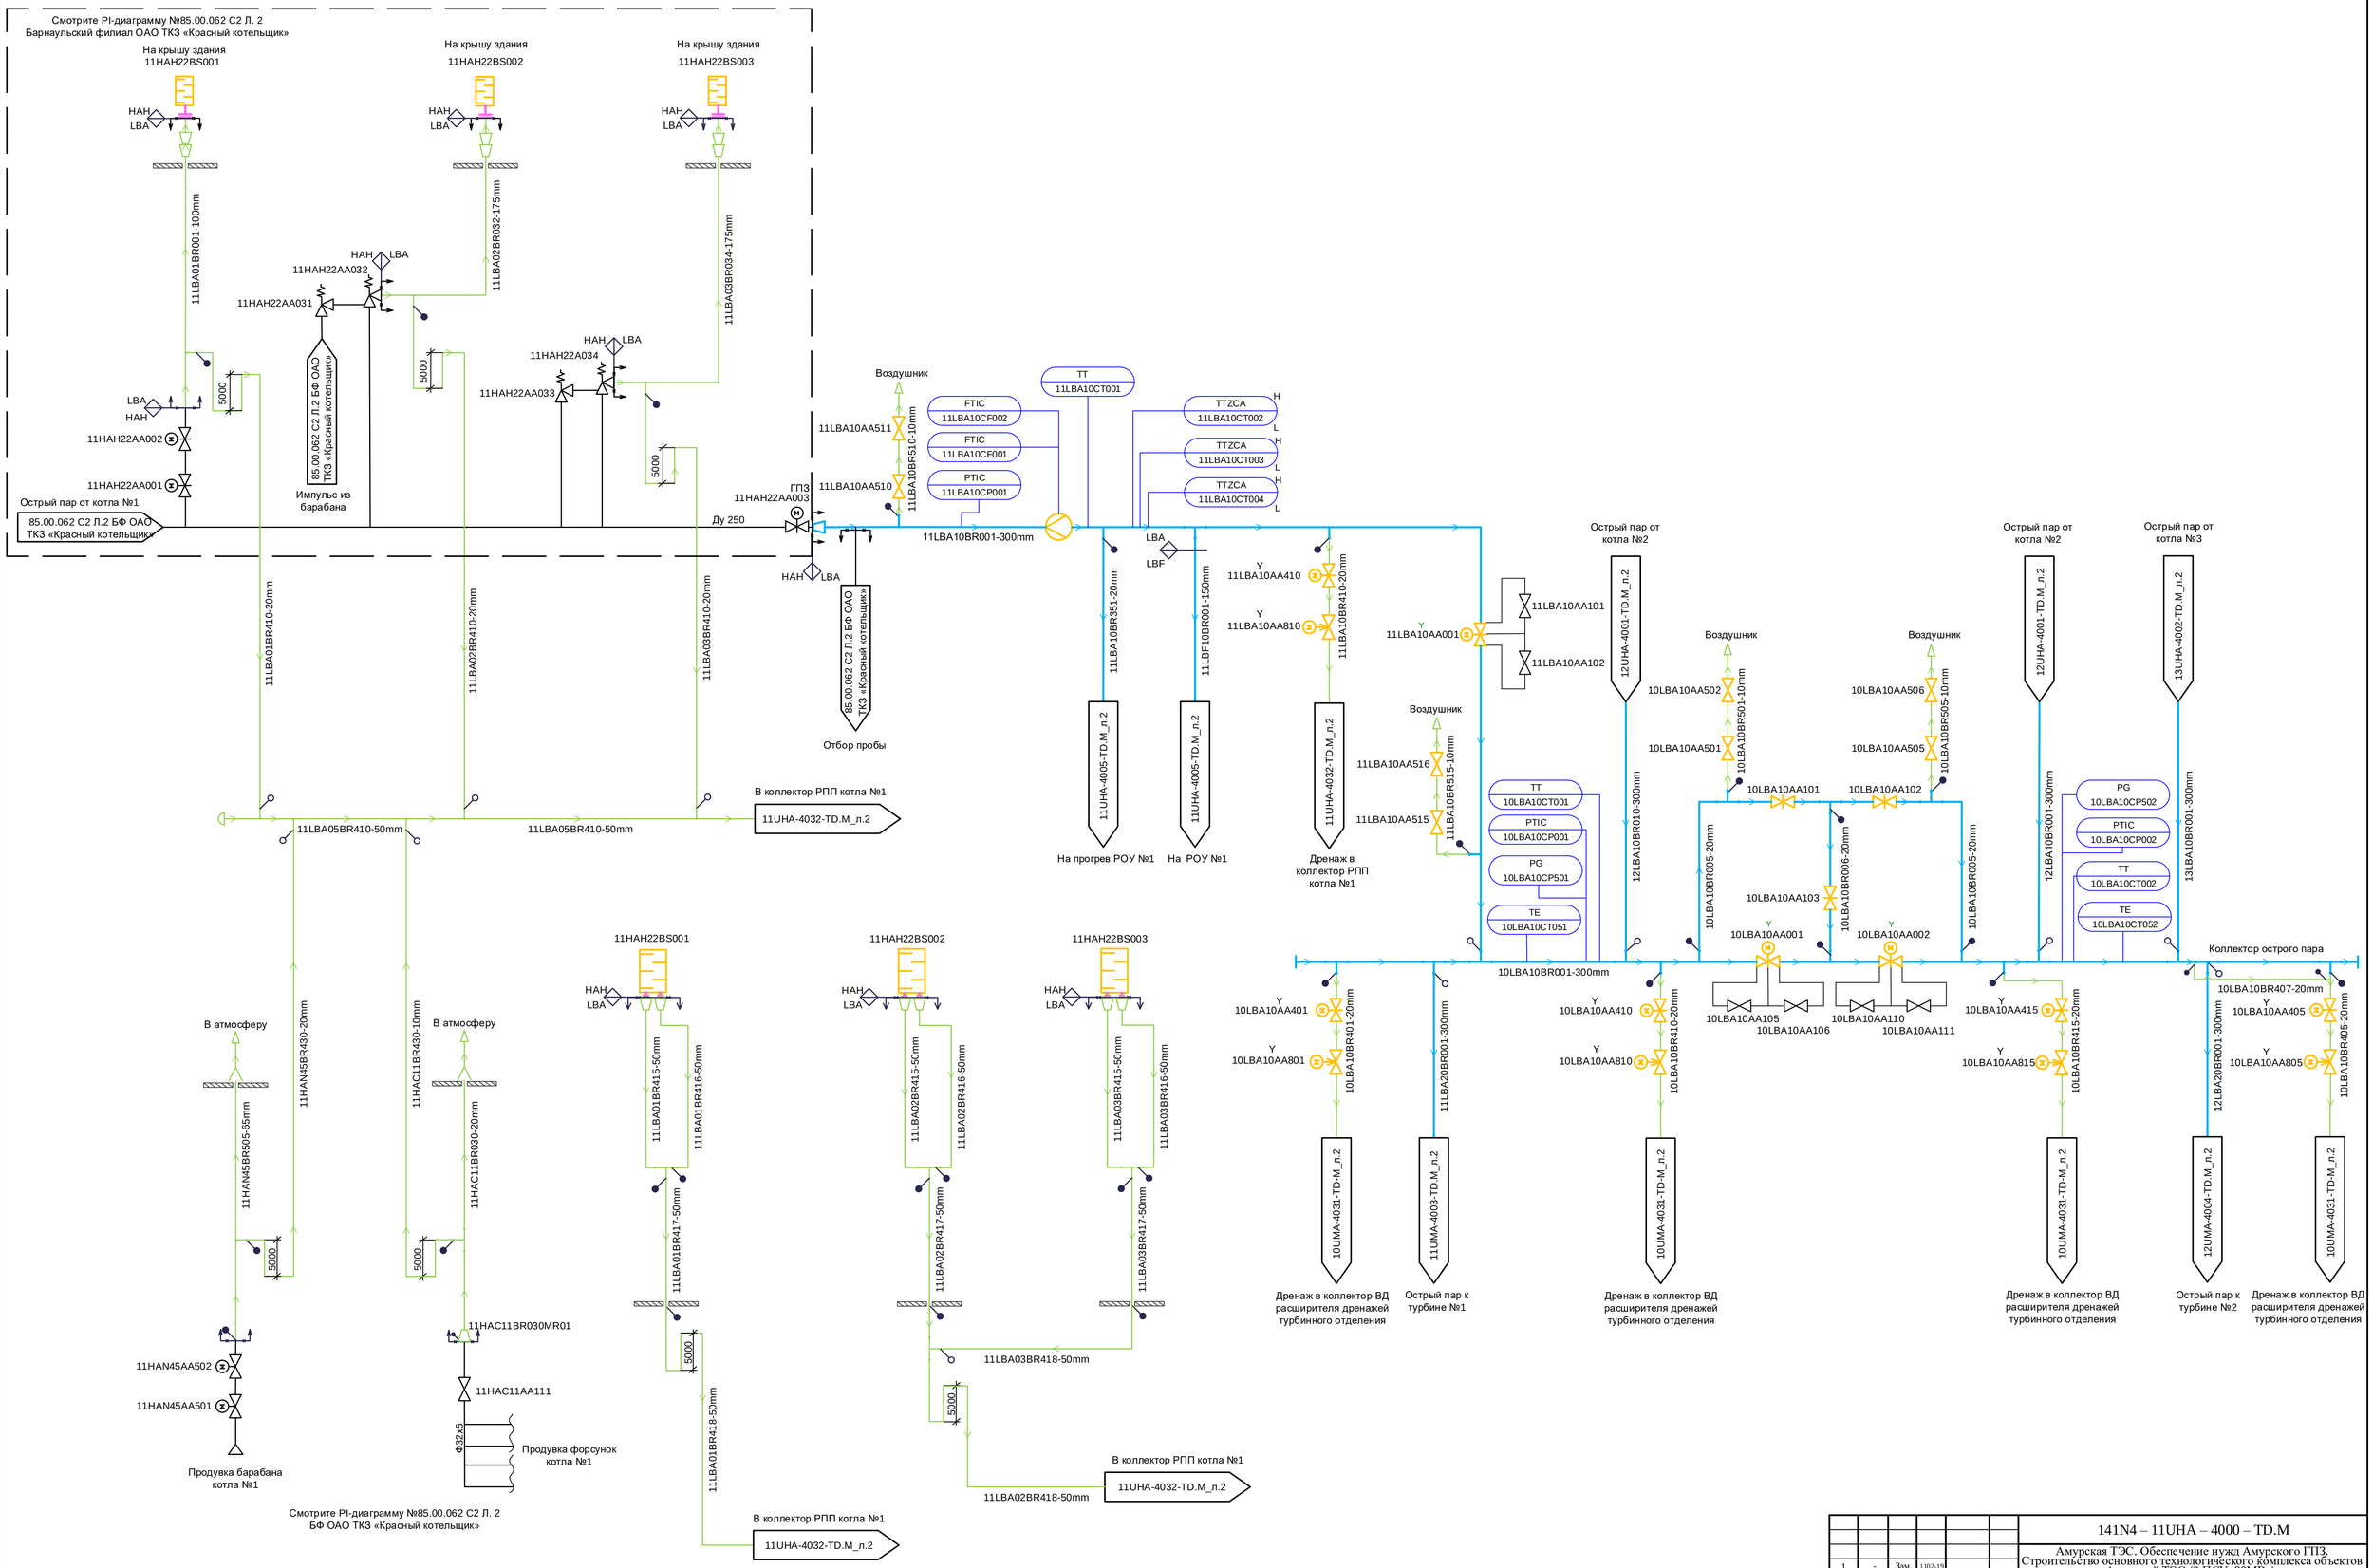

1	-	Зам.	1102-19			
Изм.	Кол.уч	Лист	№ док.	Подп.	Дата	
Разработал		Калиникина				
Проверил		Майорова				
Н. контр.		Грядчина				

141N4 – 11UHA – 4000 – TD.M

Амурская ТЭС. Обеспечение нужд Амурского ГПЗ. Строительство основного технологического комплекса объектов Амурской ТЭС (2 ПСУх80МВт). Этап 1."Амурская ТЭС (ПСУ-2х80 МВт)"

Котельное отделение. Паровой котел №1. PI-диаграмма трубопроводов острого пара от котла №1 к коллектору острого пара

Стадия	Лист	Листов
Р	2	

PI-диаграмма трубопроводов острого пара от котла №1 к коллектору острого пара. Система LBA

АКЦИОНЕРНОЕ ОБЩЕСТВО ИНСТИТУТ ТЕПЛОЭЛЕКТРОПРОЕКТ Г. МОСКВА

Согласовано

ОАСУ Соболева

Взам. инв. №

Подпись и дата

Инв. № подл.

Формат А1