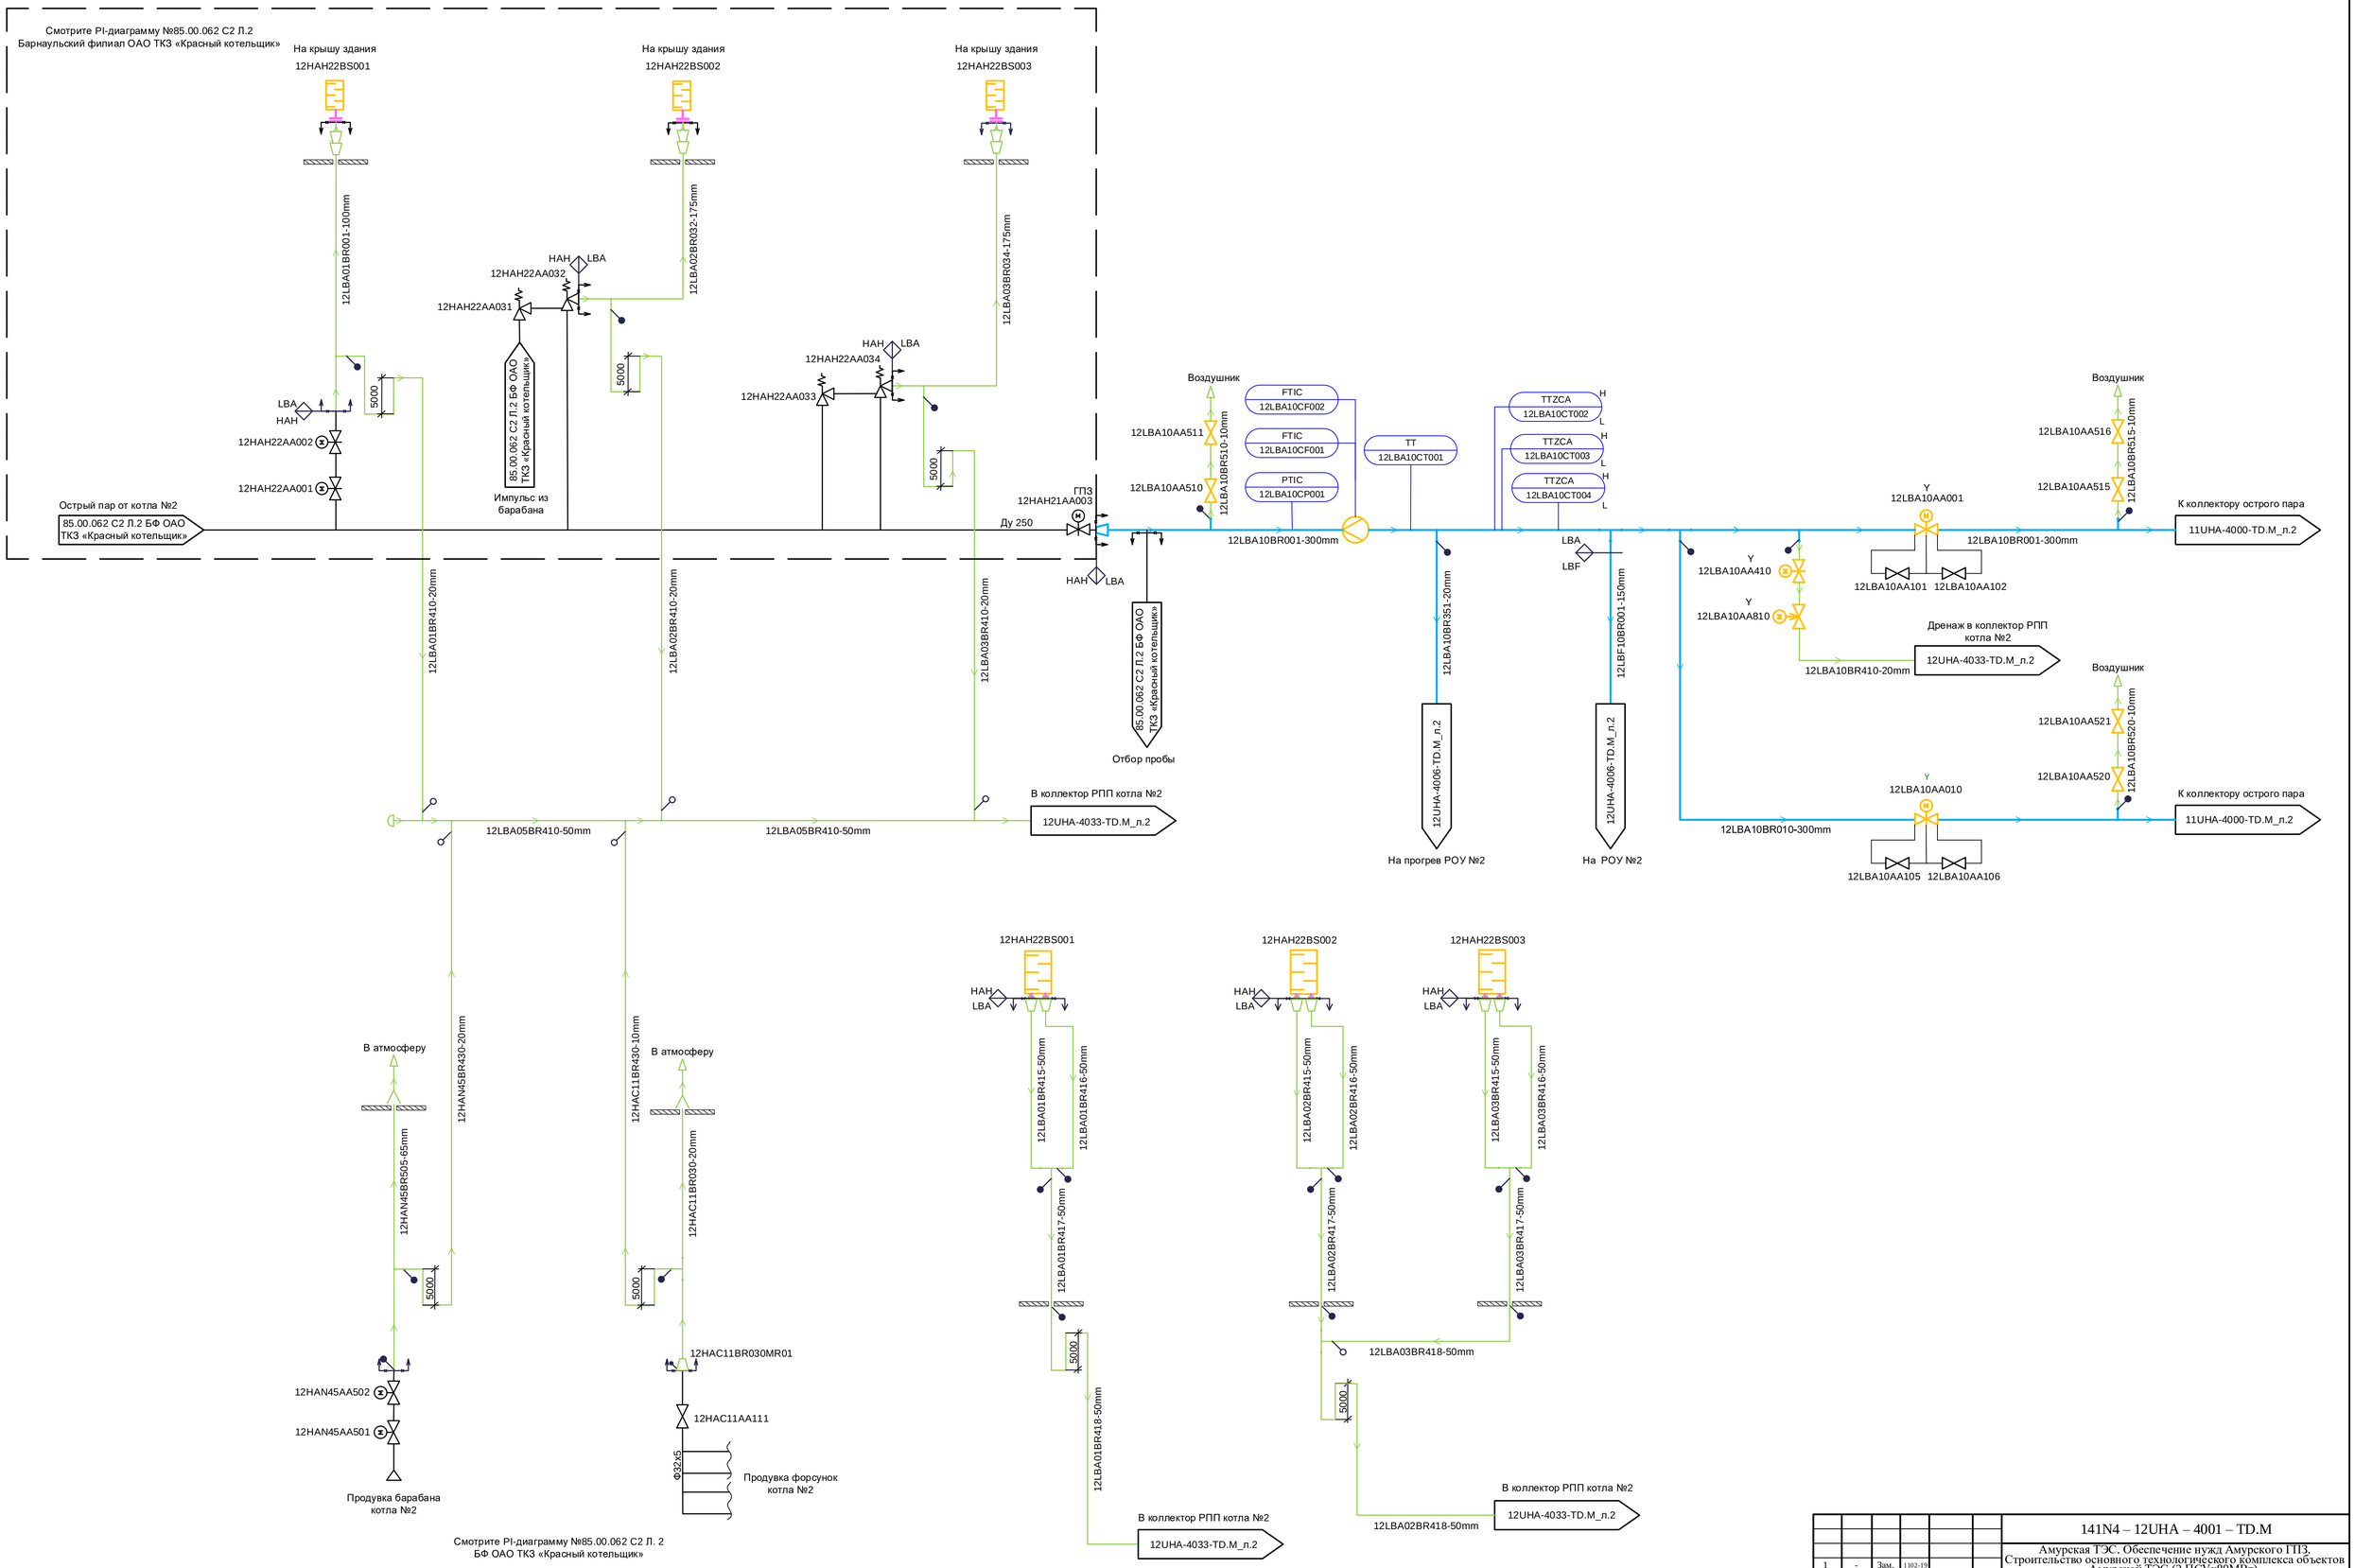

1	-	Зам.	1102-19			
Изм.	Кол.уч	Лист	№ док.	Подп.	Дата	
Разработал		Калинкина				
Проверил		Майорова				
Н. контр.		Грядчина				

141N4 – 12UHA – 4001 – TD.M

Амурская ТЭС. Обеспечение нужд Амурского ГПЗ. Строительство основного технологического комплекса объектов Амурской ТЭС (2 ПСУх80МВт). Этап 1."Амурская ТЭС (ПСУ-2х80 МВт)"

Котельное отделение. Паровой котел №2. PI-диаграмма трубопроводов острого пара от котла №2 к коллектору острого пара

Стадия	Лист	Листов
Р	2	

PI-диаграмма трубопроводов острого пара от котла №2 к коллектору острого пара. Система LBA

АКЦИОНЕРНОЕ ОБЩЕСТВО ИНСТИТУТ ТЕПЛОЭЛЕКТРОПРОЕКТ г. МОСКВА

Согласовано

ОАСУ Соболева

Взам. инв. №

Подпись и дата

Инв. № подл.

Формат А1