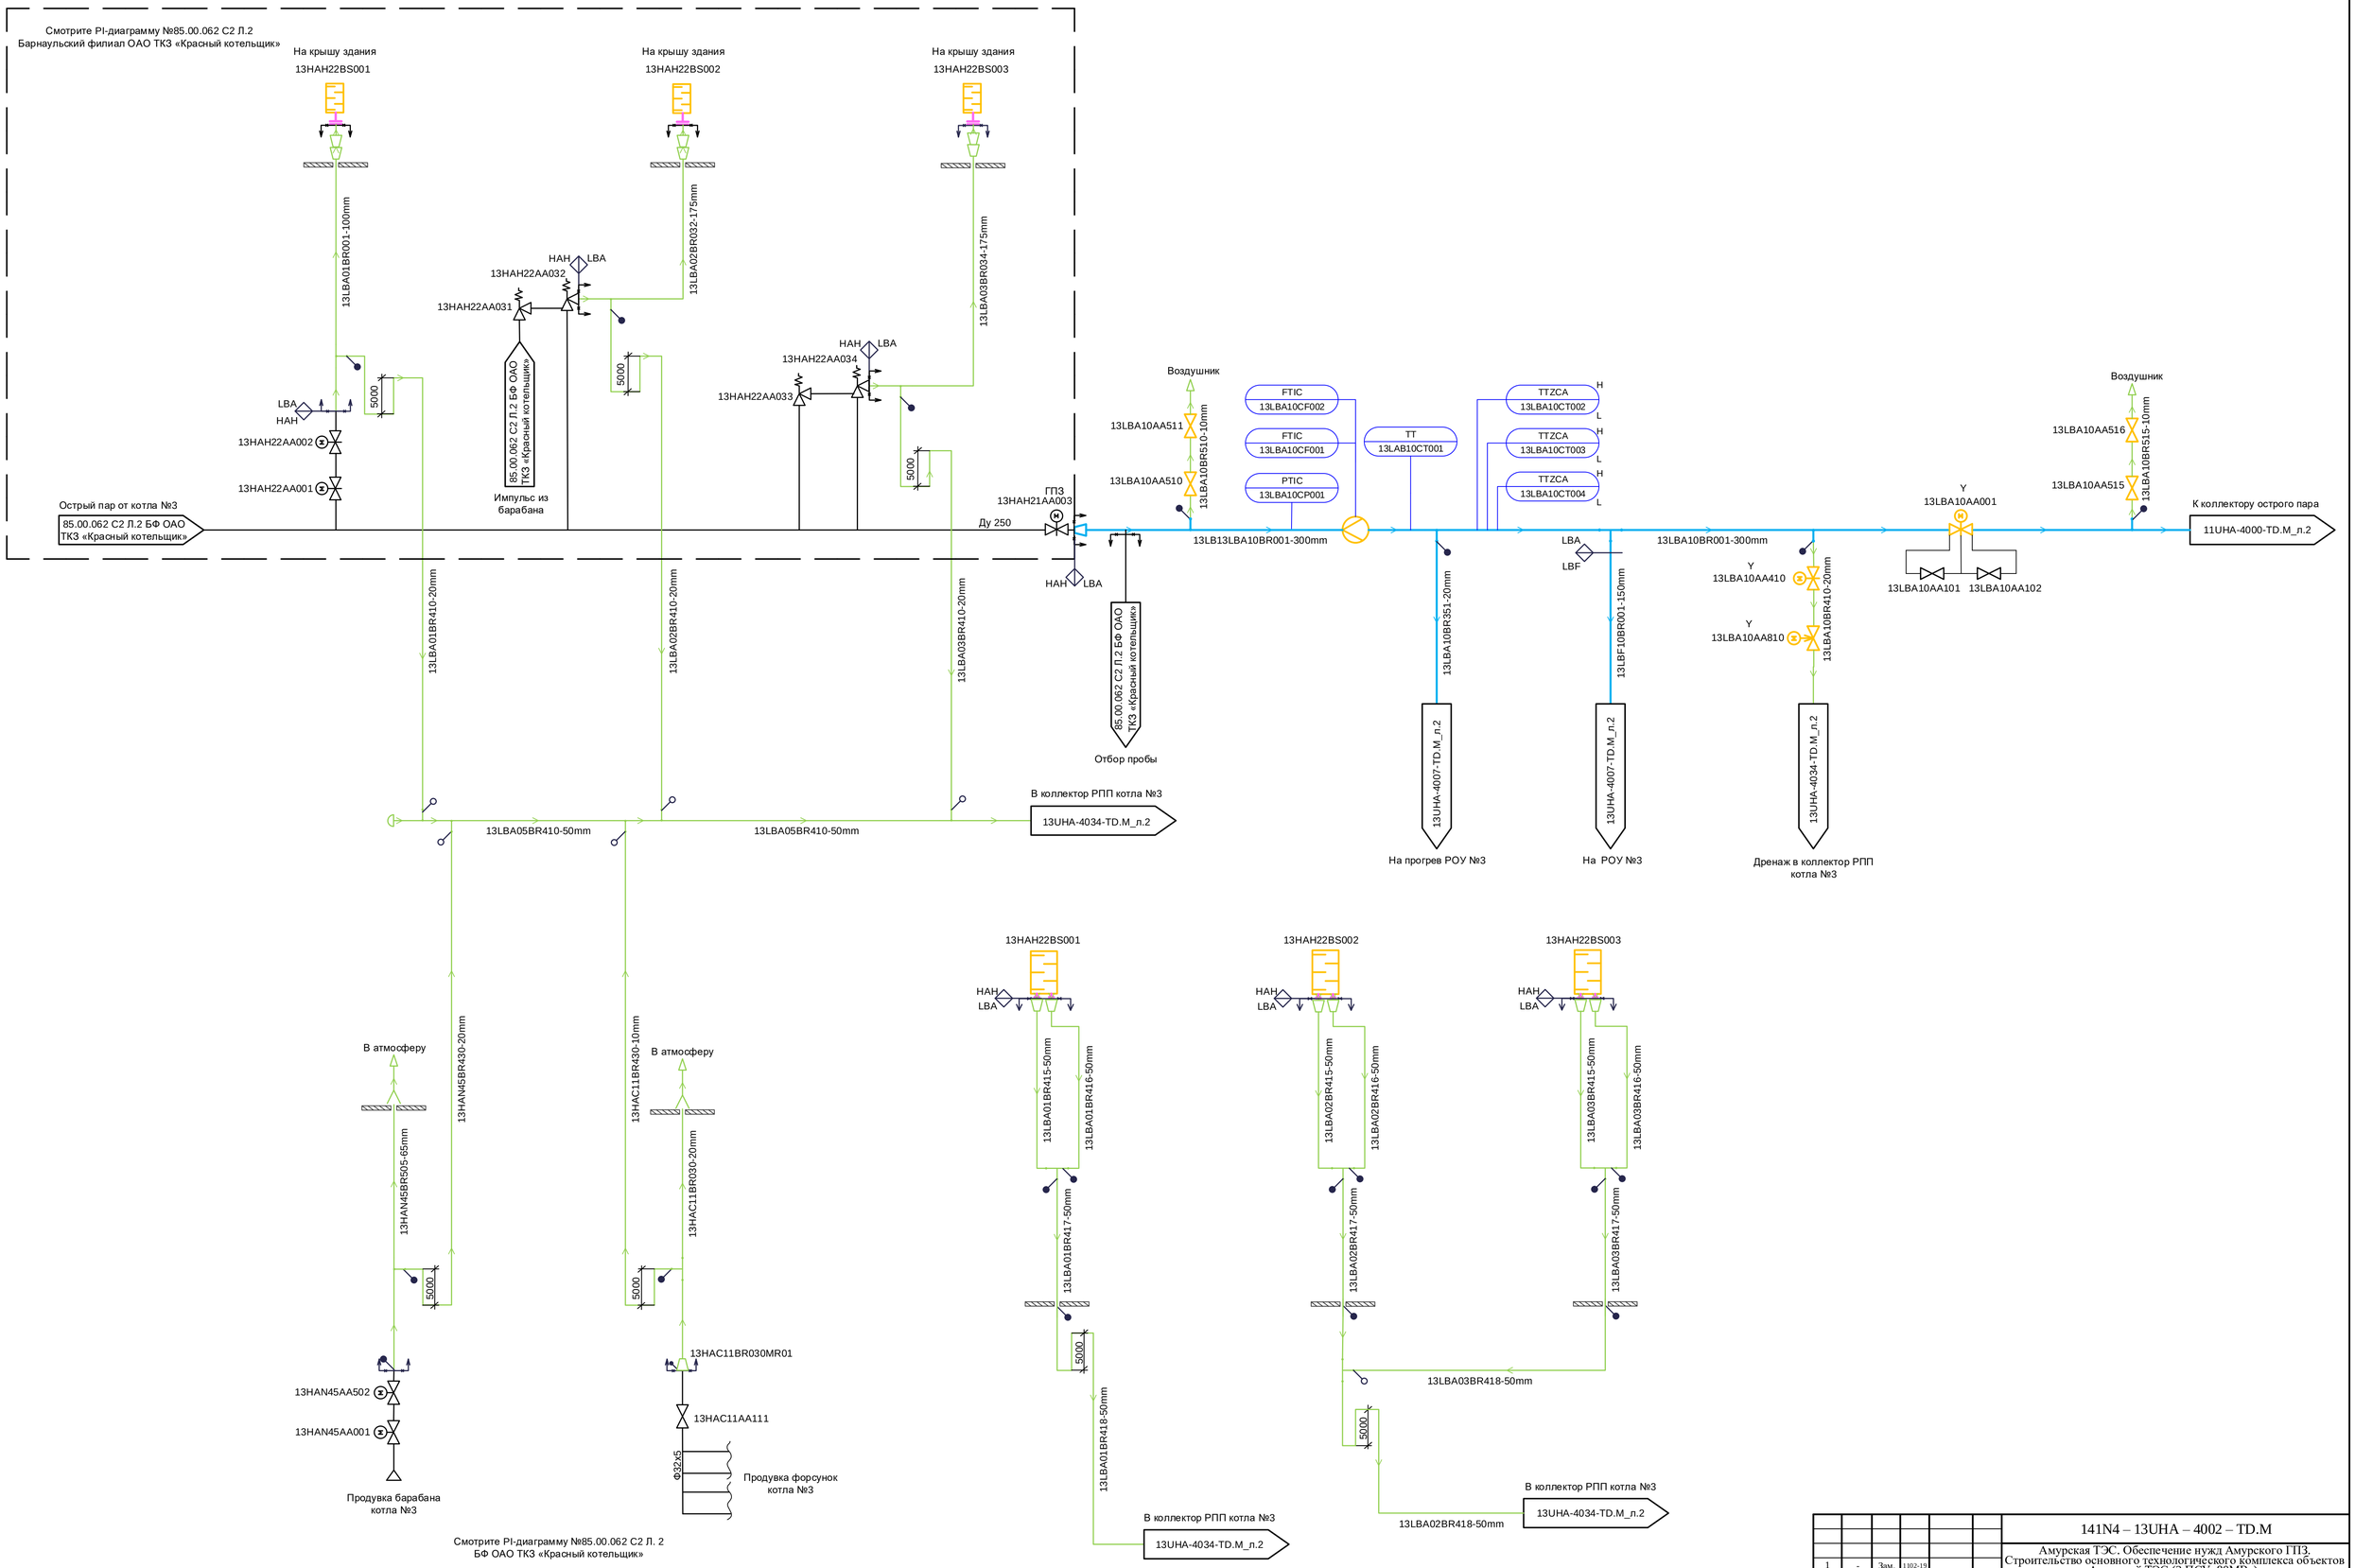

1	-	Зам.	1102-19			
Изм.	Кол.уч	Лист	№ док.	Подп.	Дата	

141N4 – 13UHA – 4002 – TD.M

Амурская ТЭС. Обеспечение нужд Амурского ГПЗ. Строительство основного технологического комплекса объектов Амурской ТЭС (2 ПСУ х80МВт). Этап 1. "Амурская ТЭС (ПСУ -2х80 МВт)"

Разработал	Калинкина		
Проверил	Майорова		
Н. контр.	Гридчина		

Котельное отделение. Паровой котел №3. PI-диаграмма трубопроводов острого пара от котла №3 к коллектору острого пара

Стадия	Лист	Листов
Р	2	

PI-диаграмма трубопроводов острого пара от котла №3 к коллектору острого пара. Система LBA

АКЦИОНЕРНОЕ ОБЩЕСТВО ИНСТИТУТ ТЕПЛОЭЛЕКТРОПРОЕКТ г. МОСКВА

Согласовано

ОАСУ	Соболева	

Взам. инв. №

Подпись и дата

Инв. № подл.

Формат А1