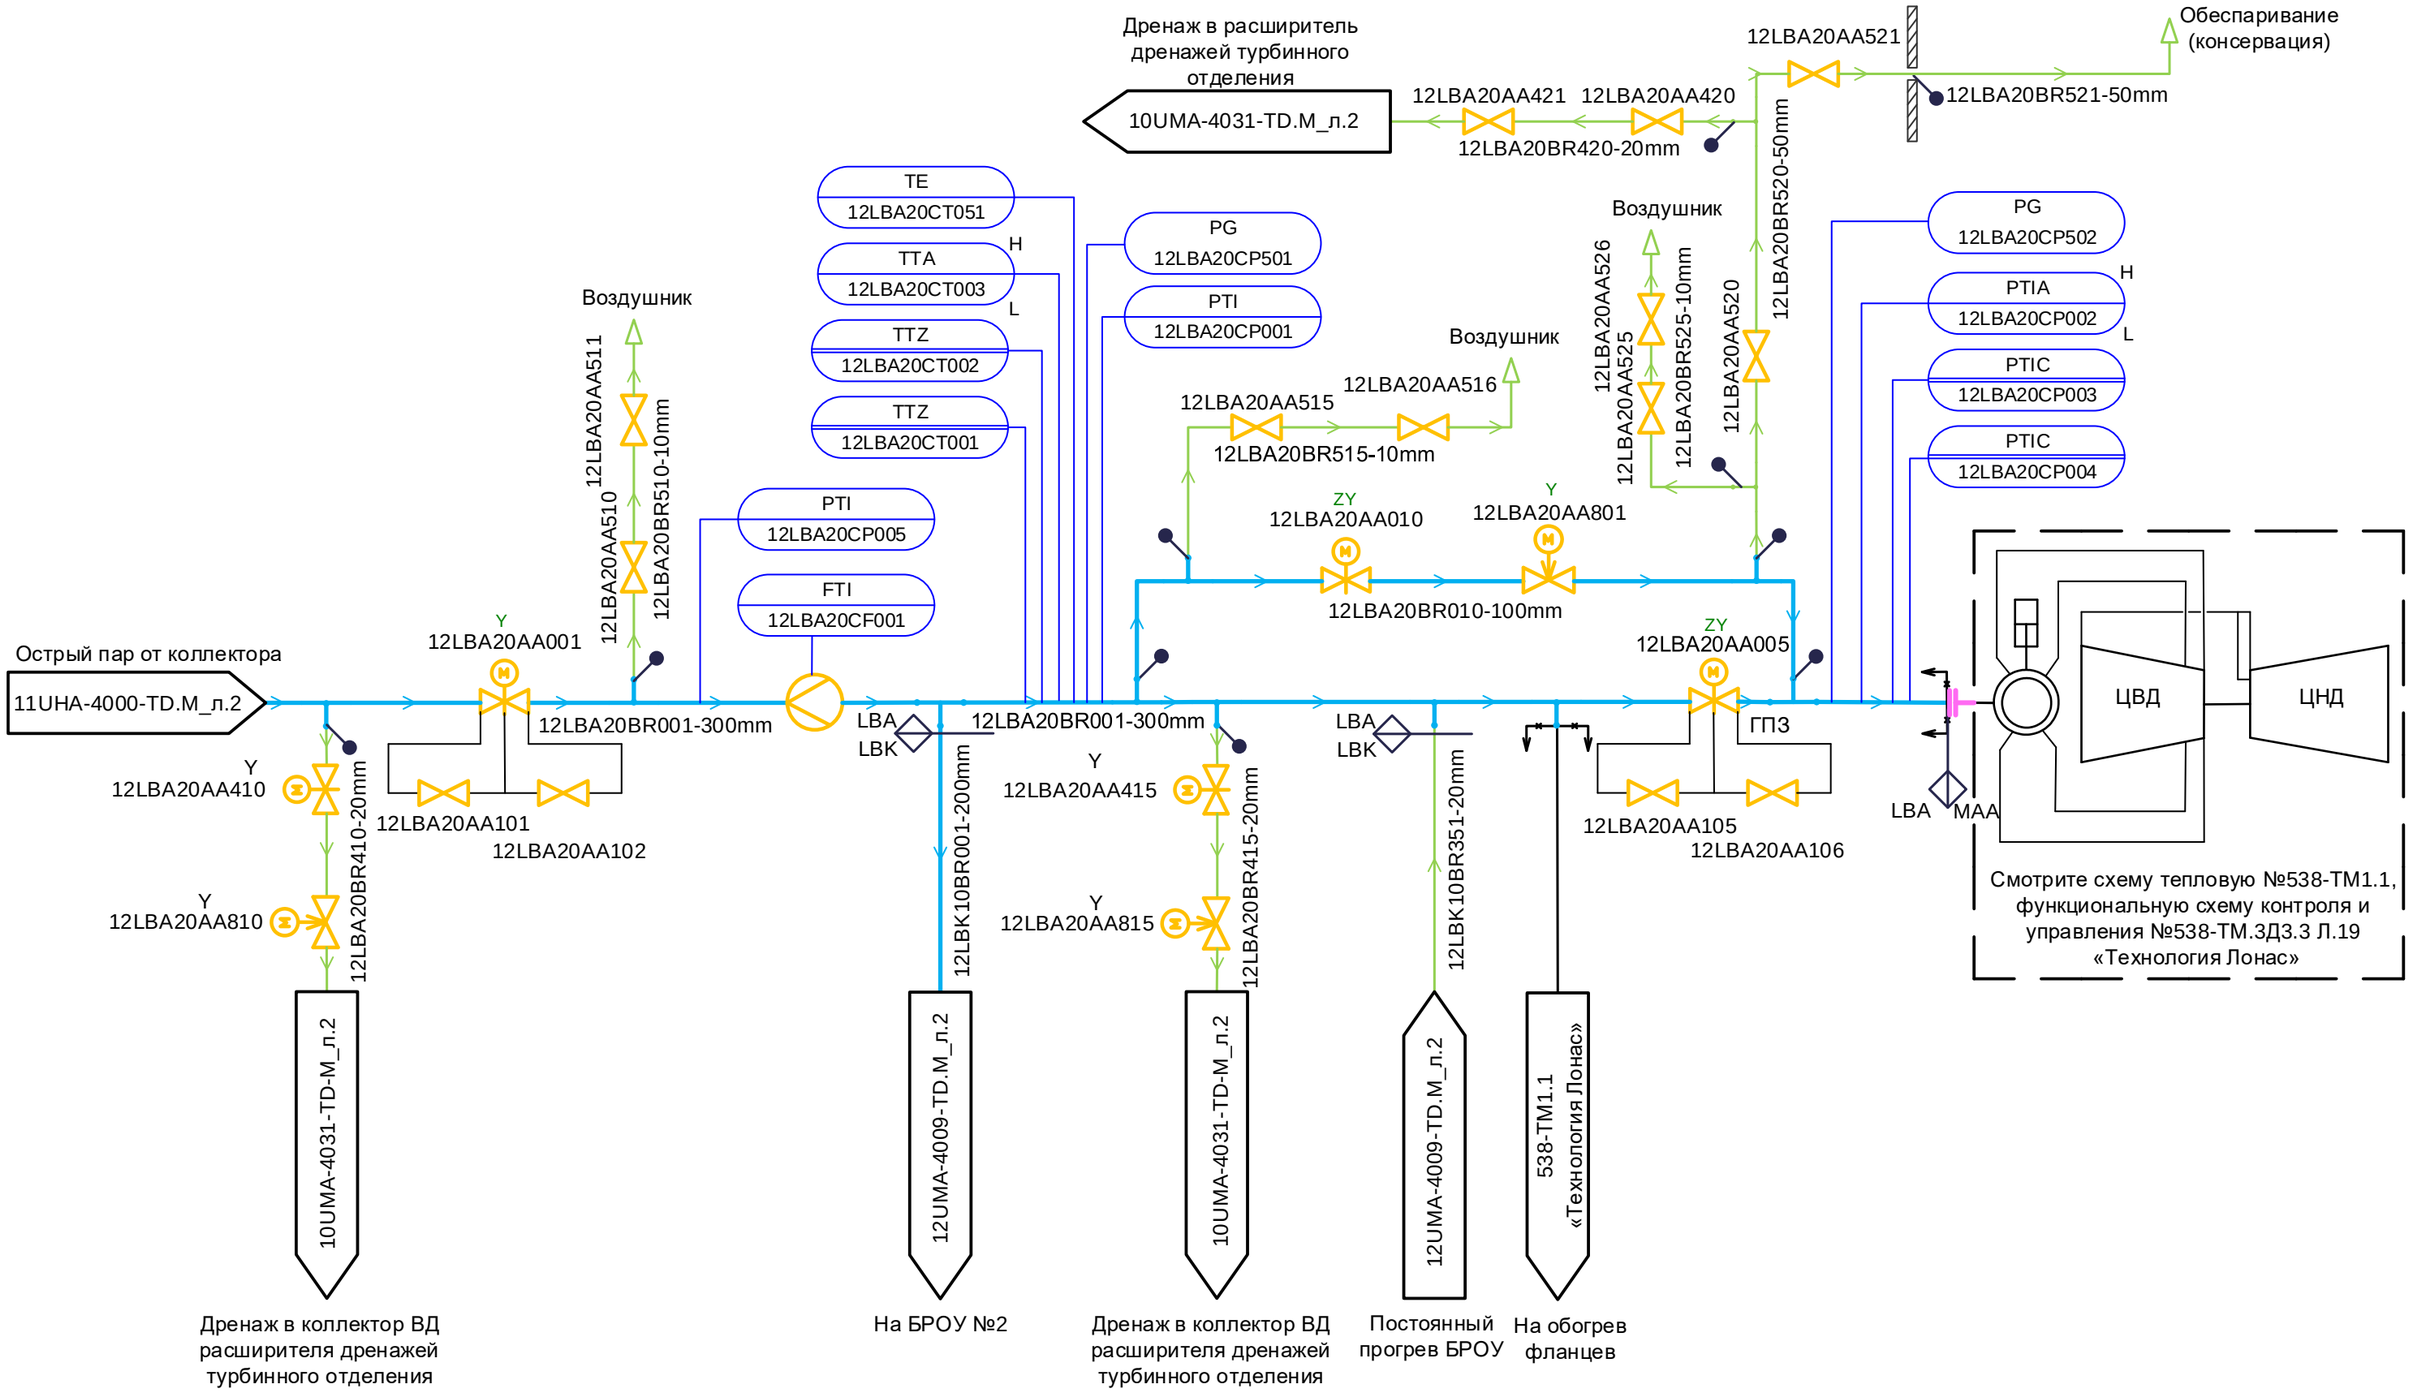

Согласовано

Соболева

ОАСУ

Взам. инв. №

Подпись и дата

Инв. № подл.

1	-	Зам	1102-19			
Изм.	Кол.уч	Лист	№ док.	Подп.	Дата	
Разработал		Калинкина				
Проверил		Майорова				
Н. контр.		Гридчина				

141N4 – 12UMA – 4004 – TD.M

Амурская ТЭС. Обеспечение нужд Амурского ГПЗ. Строительство основного технологического комплекса объектов Амурской ТЭС (2 ПСУ х80МВт). Этап 1."Амурская ТЭС (ПСУ-2х80 МВт)"

Паротурбинное отделение. Паротурбинная установка №2
PI-диаграмма трубопроводов острого пара от коллектора к турбине №2

Стадия	Лист	Листов
Р	2	

PI-диаграмма трубопроводов острого пара от коллектора к турбине №2
Система LBA

АКЦИОНЕРНОЕ ОБЩЕСТВО ИНСТИТУТ ТЕПЛОЭЛЕКТРОПРОЕКТ Г. МОСКВА

Формат А3