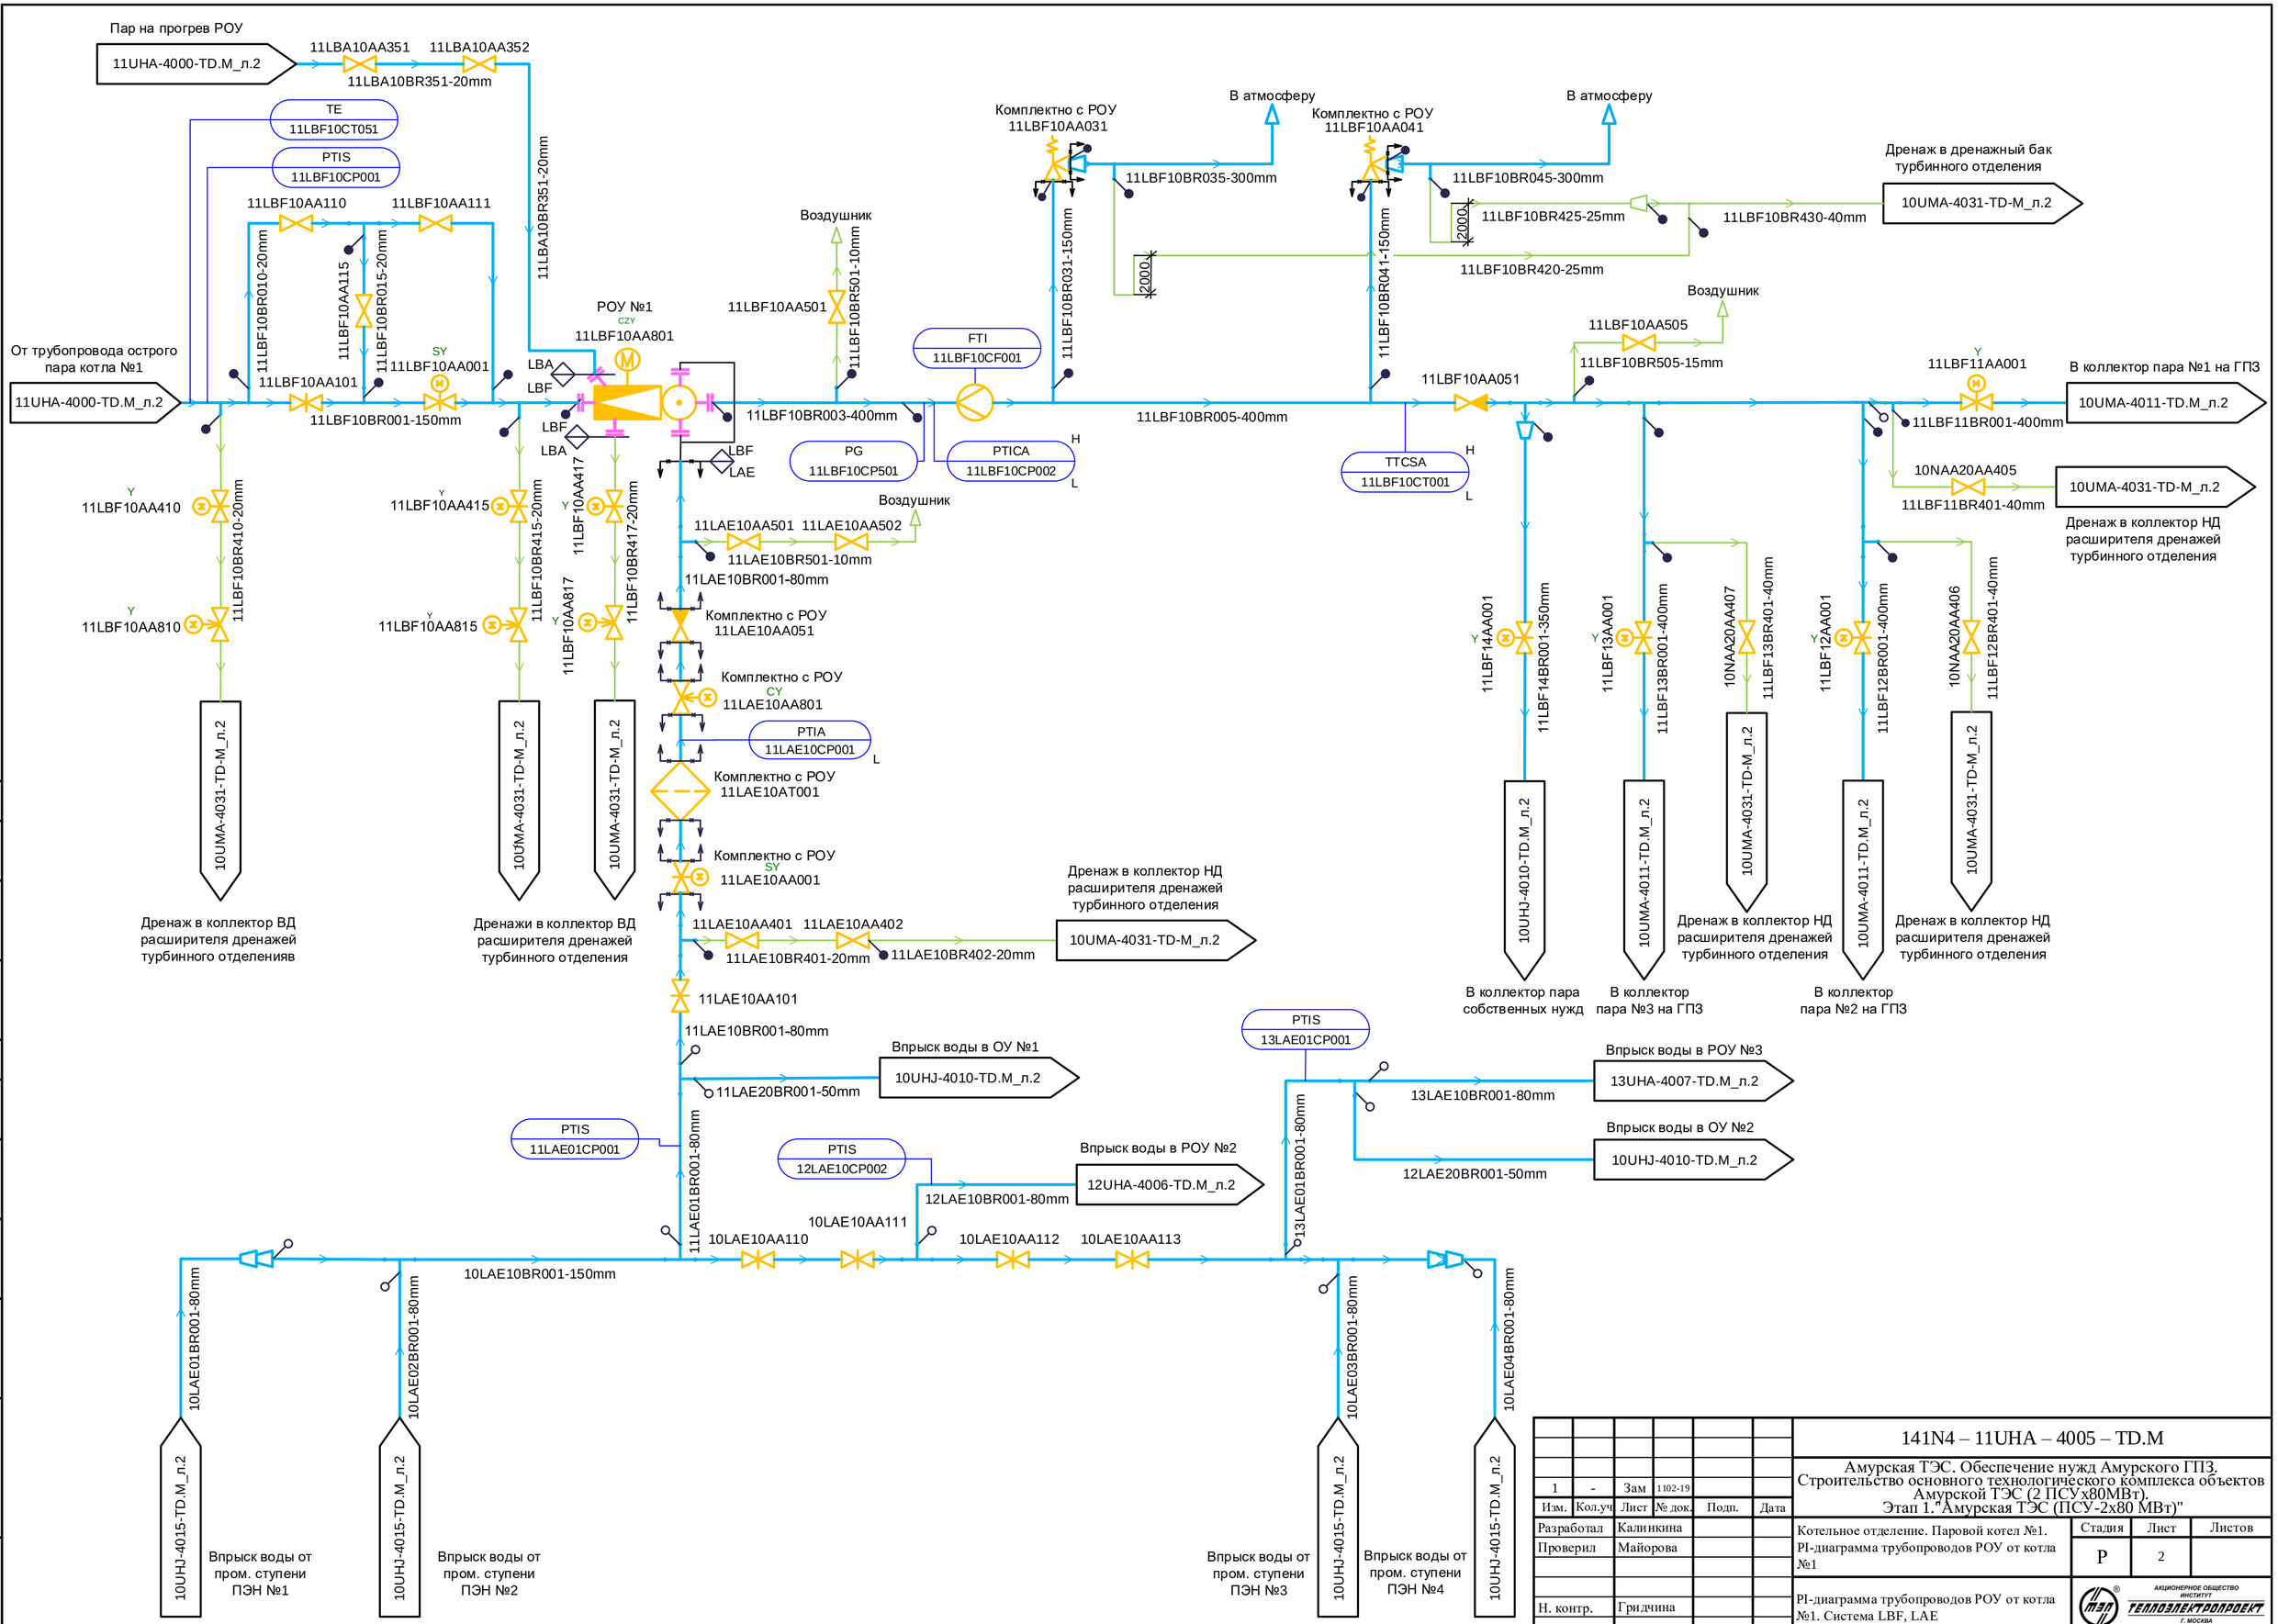

Изм.	Кол.уч	Лист	№ док.	Подп.	Дата
1	-	Зам	1102-19		

141N4 – 11UHA – 4005 – TD.M

Амурская ТЭС. Обеспечение нужд Амурского ГПЗ. Строительство основного технологического комплекса объектов Амурской ТЭС (2 ПСУ х80МВт). Этап 1."Амурская ТЭС (ПСУ-2х80 МВт)"

Разработал	Калинкина	
Проверил	Майорова	
Н. контр.	Гридчина	

Котельное отделение. Паровой котел №1. PI-диаграмма трубопроводов РОУ от котла №1

Стадия	Лист	Листов
Р	2	

PI-диаграмма трубопроводов РОУ от котла №1. Система LBF, LAE

АКЦИОНЕРНОЕ ОБЩЕСТВО ИНСТИТУТ ТЕПЛОЭЛЕКТРОПРОЕКТ Г. МОСКВА

Согласовано

ОАСУ Соболева

Взам. инв. №

Подпись и дата

Инв. № подл.

Формат А2