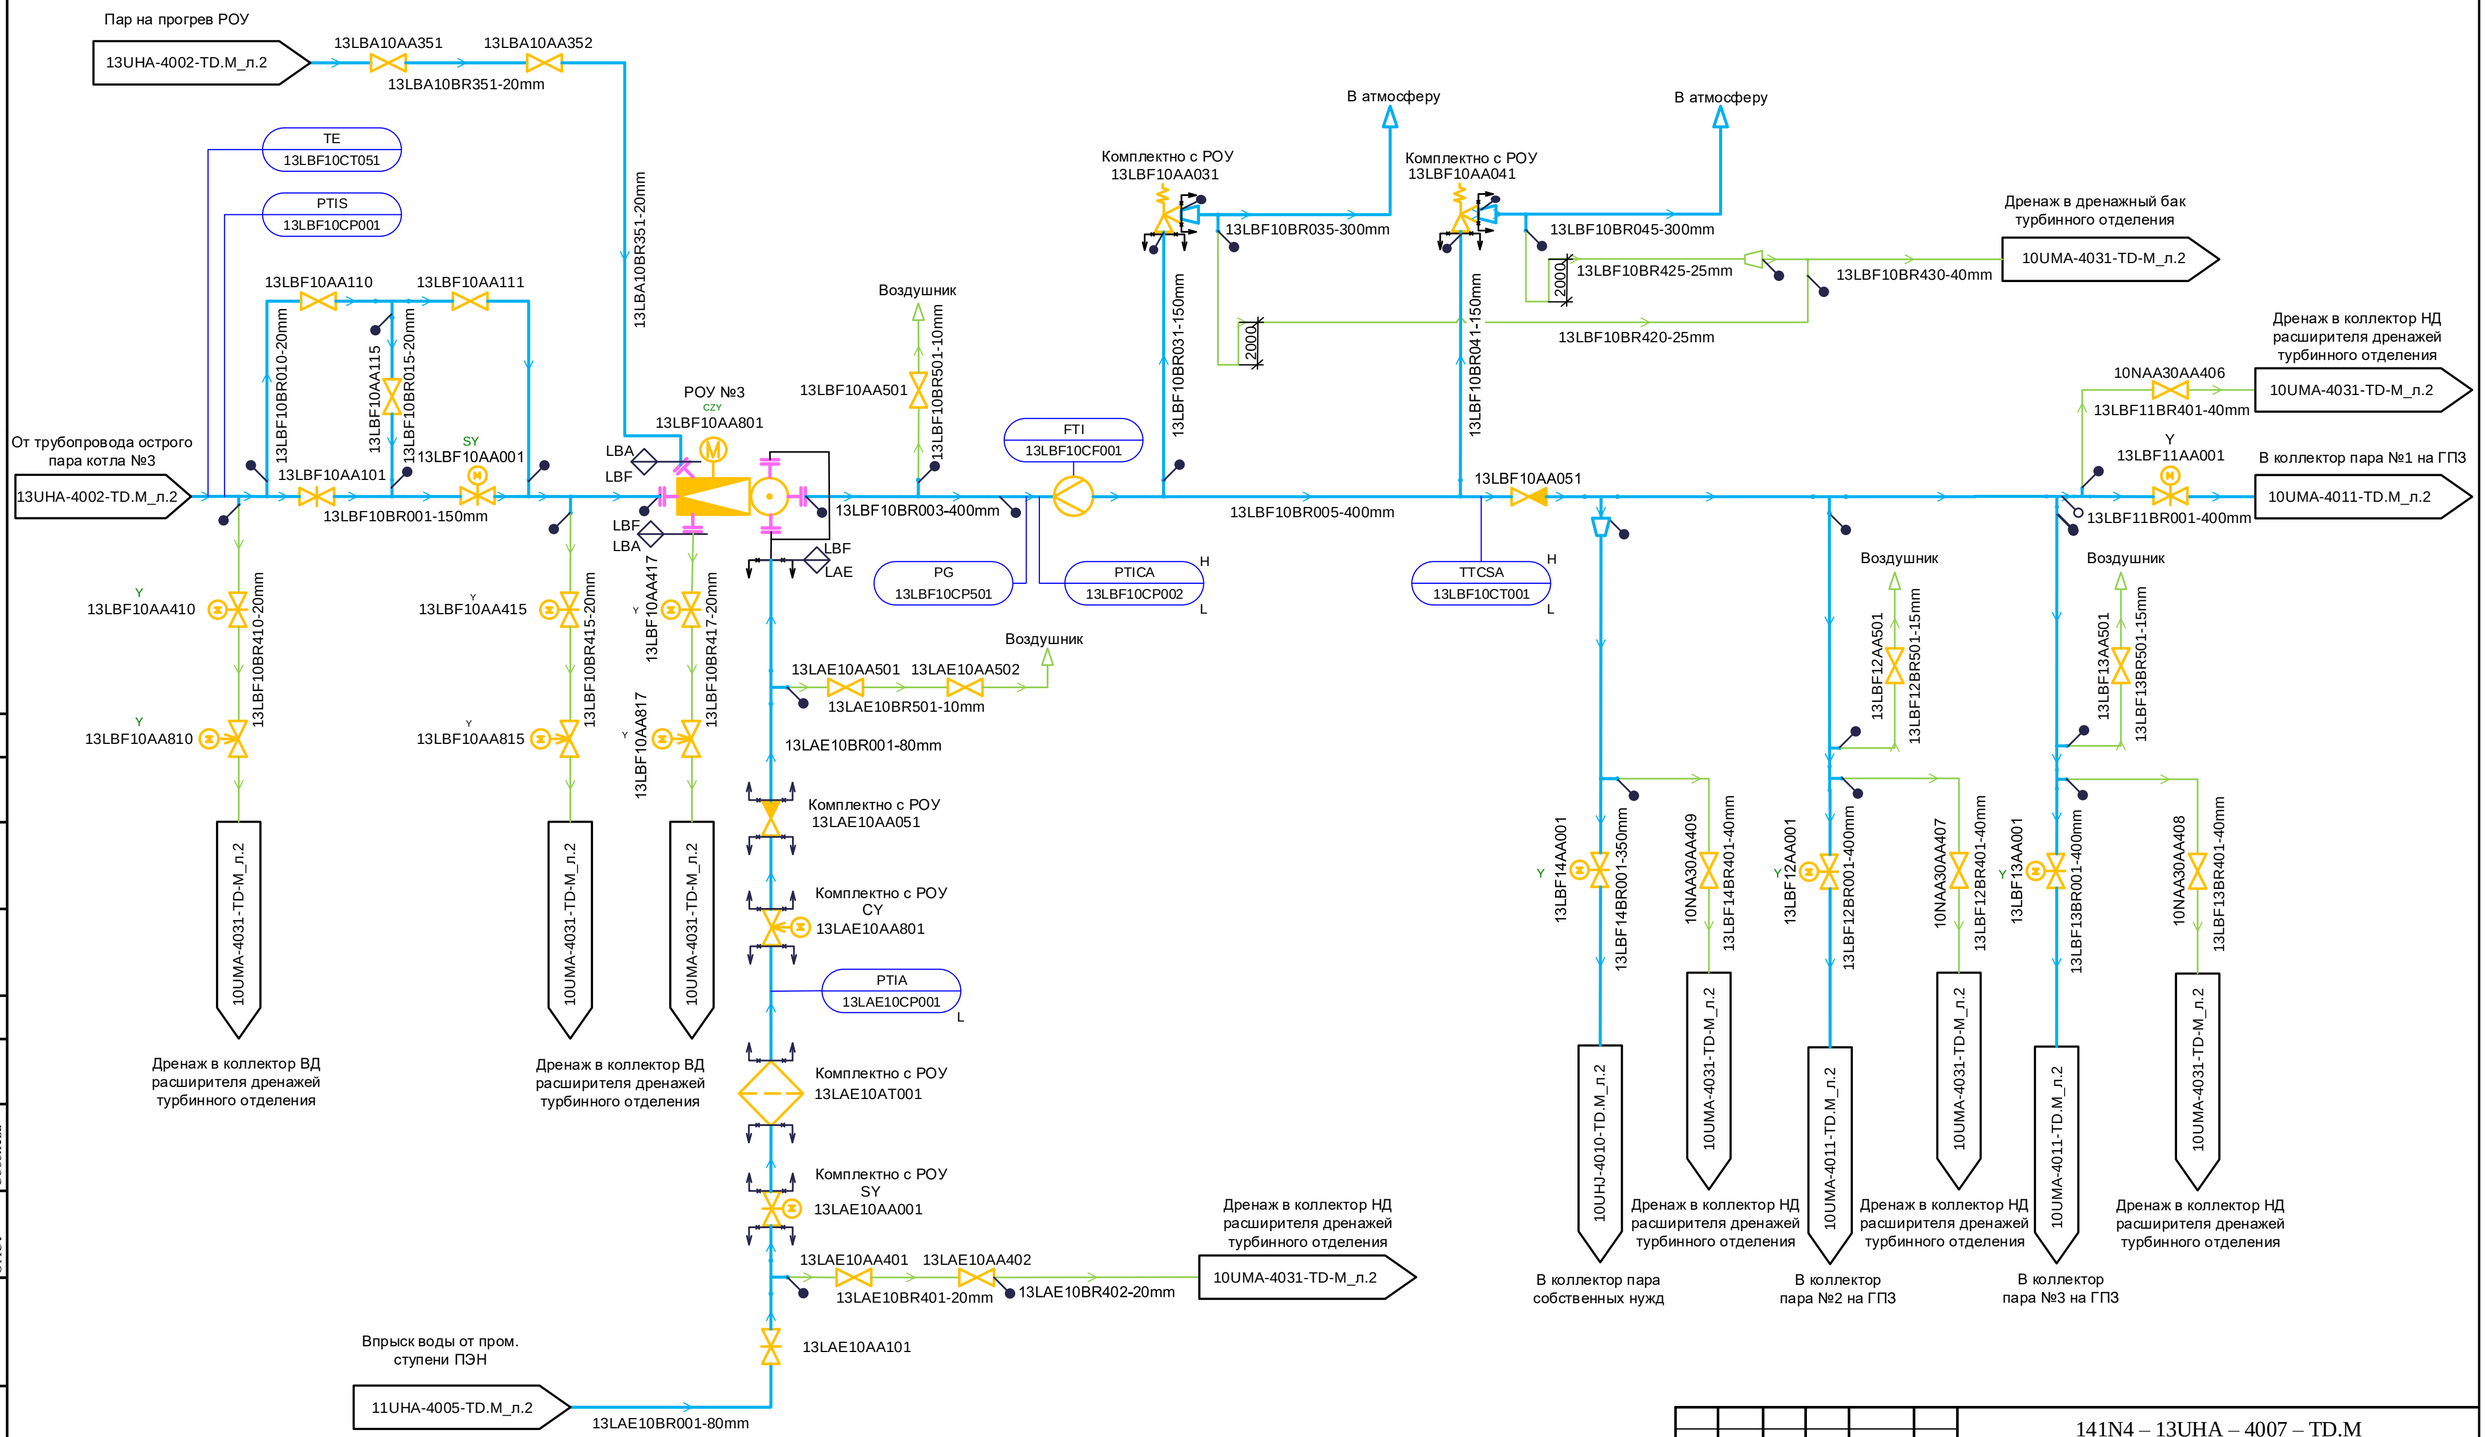

1	-	Зам.	1102-19			
Изм.	Кол.уч	Лист	№ док.	Подп.	Дата	
Разработал		Калинкина				
Проверил		Майорова				
Н. контр.		Гридчина				

141N4 – 13UHA – 4007 – TD.M

Амурская ТЭС. Обеспечение нужд Амурского ГПЗ. Строительство основного технологического комплекса объектов Амурской ТЭС (2 ПСУ х80МВт). Этап 1."Амурская ТЭС (ПСУ-2х80 МВт)"

Котельное отделение. Паровой котел №3
PI-диаграмма трубопроводов РОУ от котла №3

Стадия	Лист	Листов
Р	2	

PI-диаграмма трубопроводов РОУ от котла №3. Система LBF, LAE

АКЦИОНЕРНОЕ ОБЩЕСТВО ИНСТИТУТ ТЕПЛОЭЛЕКТРОПРОЕКТ г. МОСКВА

Согласовано
ОАСУ Соболева

Взам. инв. №
Подпись и дата
Инв. № подл.

Формат А2