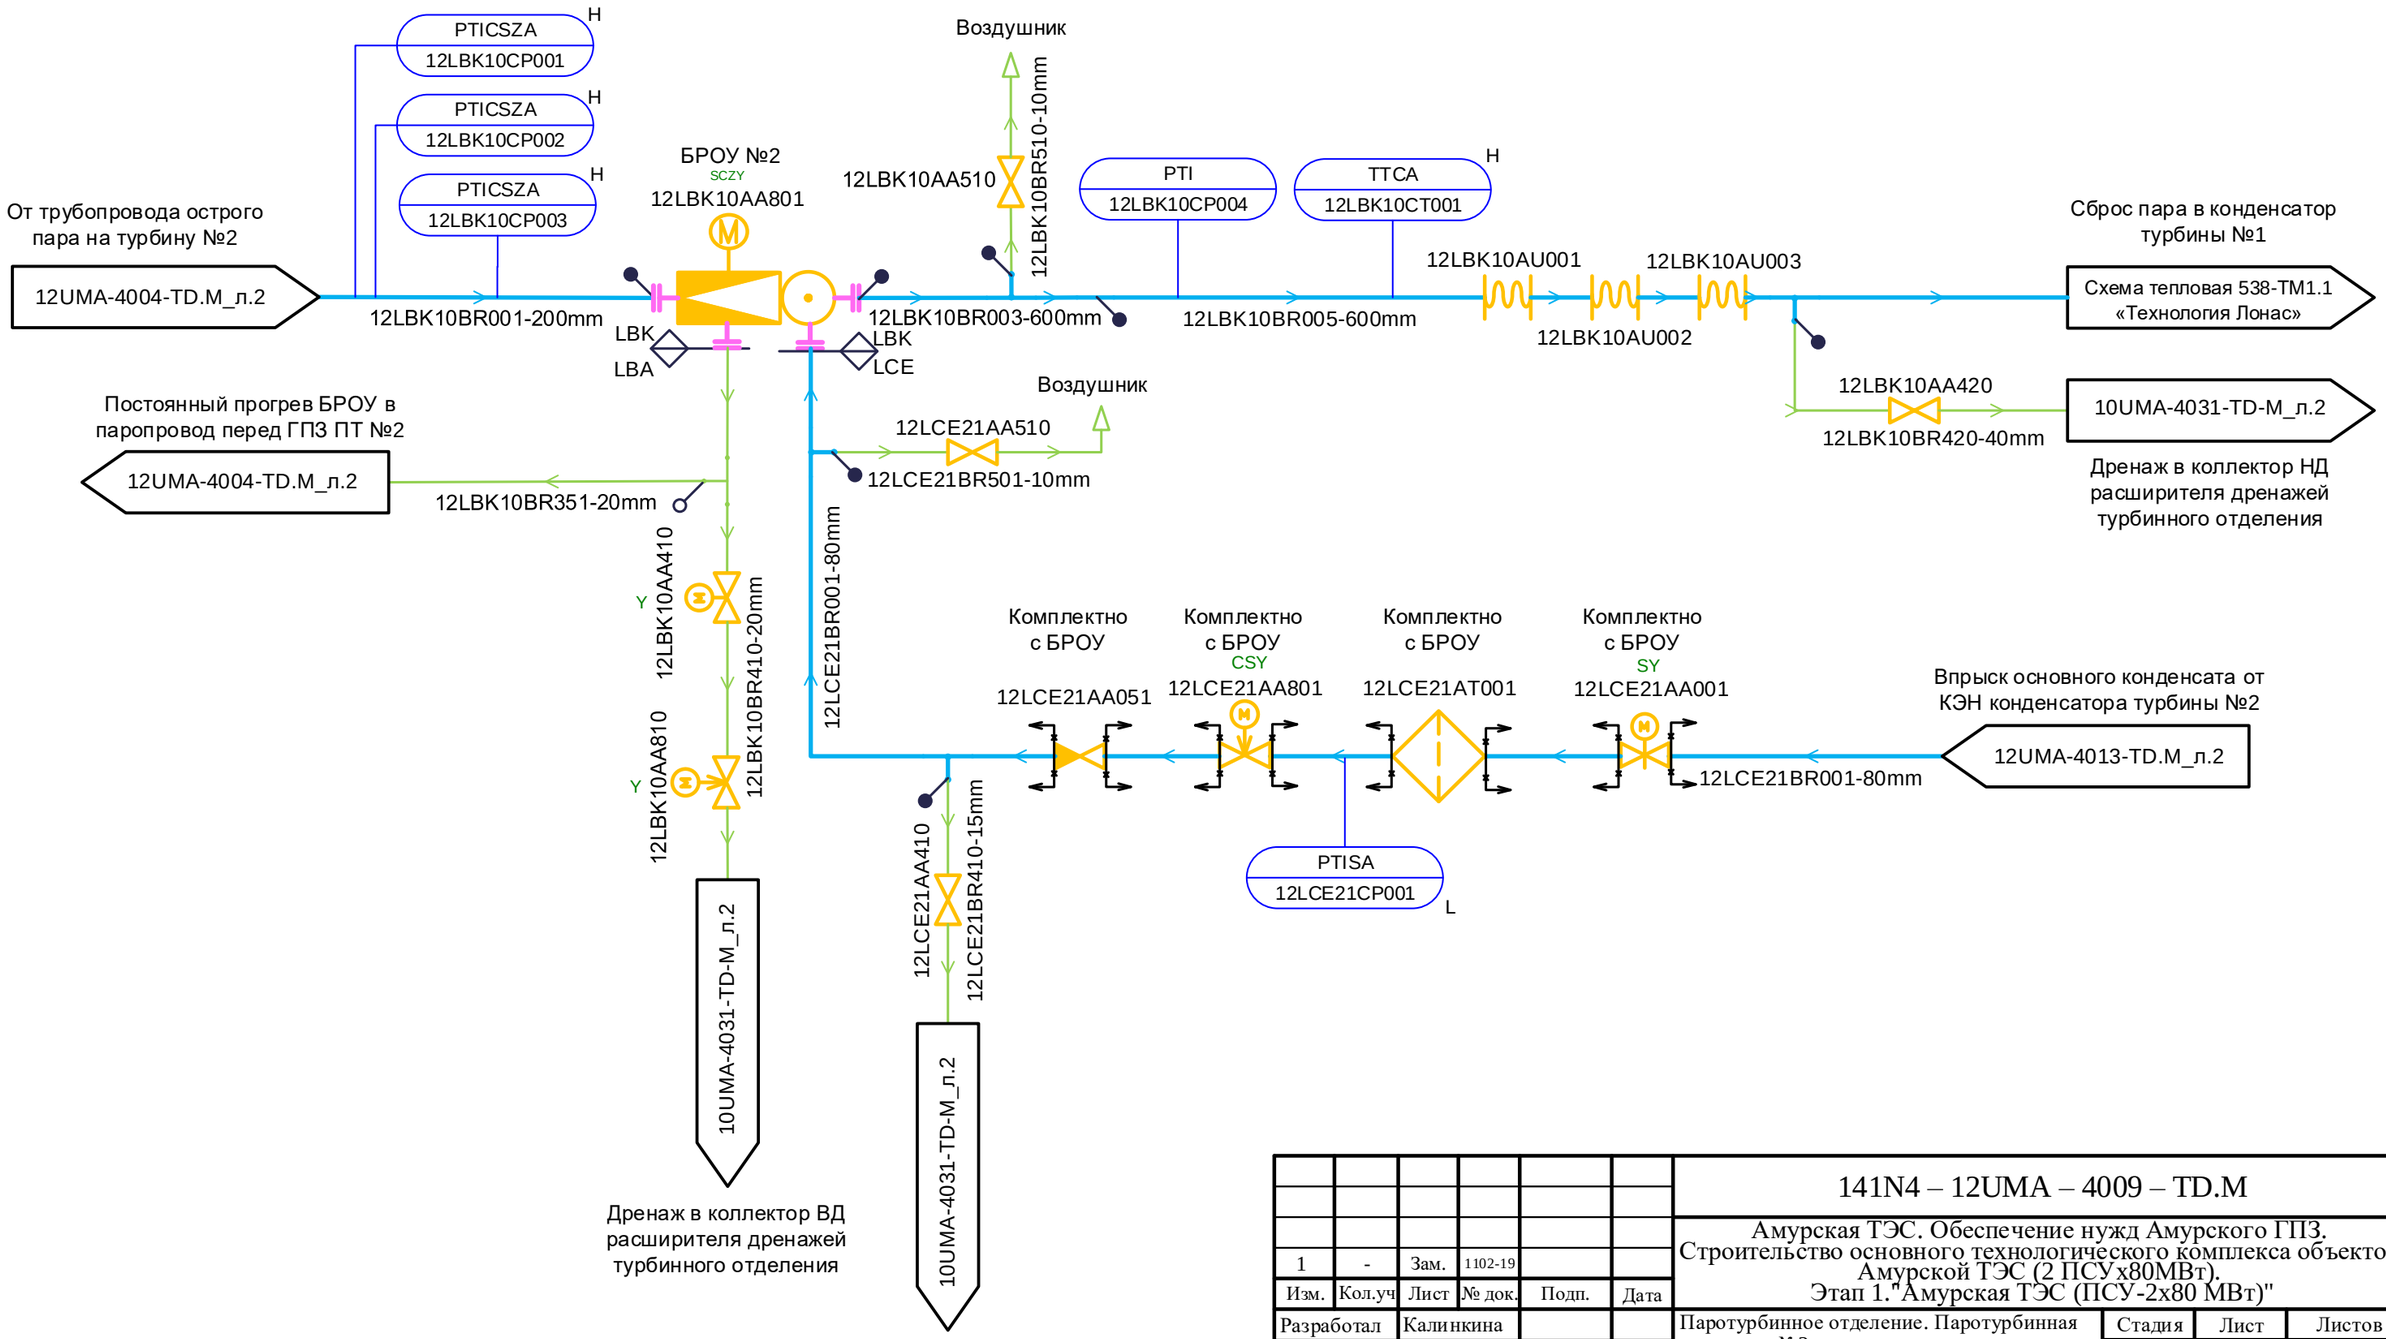

						141N4 – 12UMA – 4009 – TD.M		
1	-	Зам.	1102-19			Амурская ТЭС. Обеспечение нужд Амурского ГПЗ. Строительство основного технологического комплекса объектов Амурской ТЭС (2 ПСУх80МВт). Этап 1."Амурская ТЭС (ПСУ-2х80 МВт)"		
Изм.	Кол.уч	Лист	№ док.	Подп.	Дата			
Разработал		Калинкина				Паротурбинное отделение. Паротурбинная установка №2. PI-диаграмма трубопроводов БРОУ в конденсатор турбины №2	Стадия	Лист	Листов
Проверил		Майорова					Р	2	
Н. контр.		Гридчина				PI-диаграмма трубопроводов БРОУ в конденсатор турбины №2. Система LBK, LCE	АКЦИОНЕРНОЕ ОБЩЕСТВО ИНСТИТУТ ТЕПЛОЭЛЕКТРОПРОЕКТ Г. МОСКВА		

Согласовано
Соболева
ОАСУ
Взам. инв. №
Подпись и дата
Инв. № подл.

Формат А3