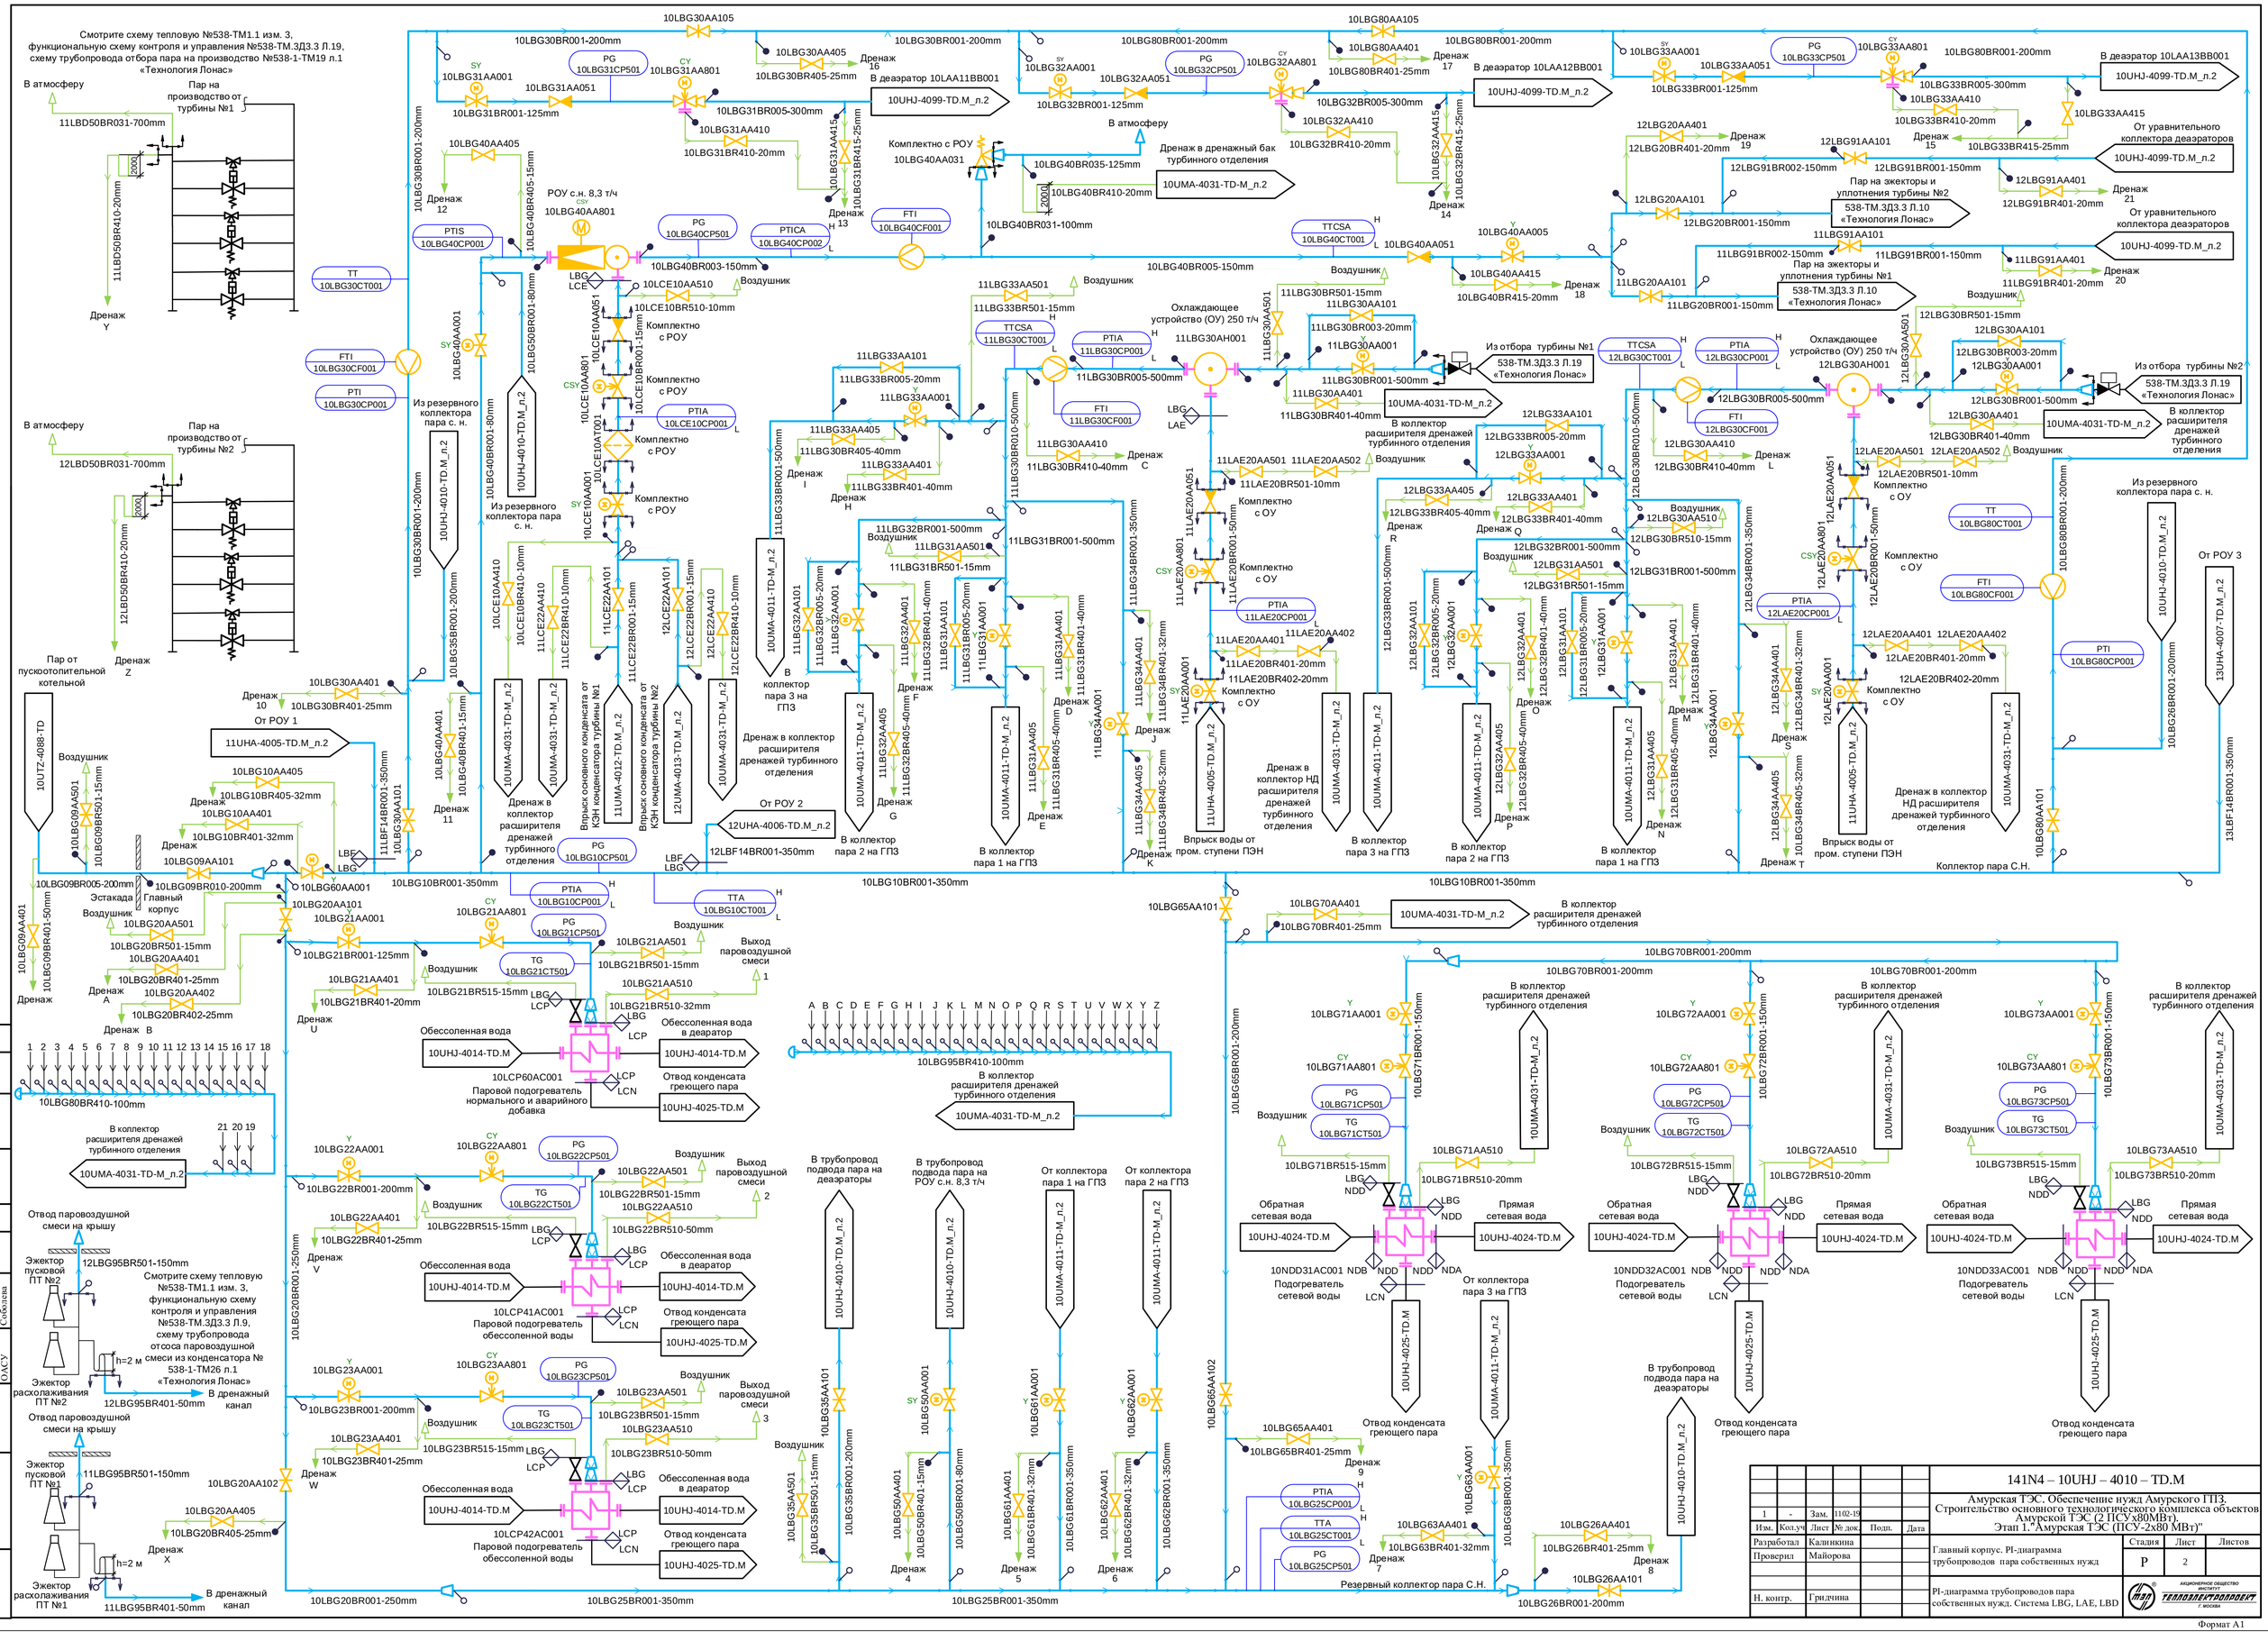
Смотрите схему тепловую №538-ТМ1.1 изм. 3, функциональную схему контроля и управления №538-ТМ.ЗД3.3 Л.19, схему трубопровода отбора пара на производство №538-1-ТМ19 л.1 «Технология Лонас»
В атмосферу
Пар на производство от турбины №1
Пар на производство от турбины №2
Пар от пускоотопительной котельной
Коллектор пара С.Н.
Резервный коллектор пара С.Н.
Главный корпус
Эстакада
Смотрите схему тепловую №538-ТМ1.1 изм. 3, функциональную схему контроля и управления №538-ТМ.ЗД3.3 Л.19, схему трубопровода отсоса паровоздушной смеси из конденсатора № 538-1-ТМ26 л.1 «Технология Лонас»
Отвод паровоздушной смеси на крышу
В дренажный канал
Обессоленная вода
Паровой подогреватель нормального и аварийного добавка
Паровой подогреватель обессоленной воды
Подогреватель сетевой воды
Обратная сетевая вода
Прямая сетевая вода
Отвод конденсата греющего пара
Выход паровоздушной смеси
Впрыск воды от пром. ступени ПЭН
Впрыск основного конденсата от КЭН конденсатора турбины №1
Впрыск основного конденсата от КЭН конденсатора турбины №2
Дренаж в коллектор расширителя дренажей турбинного отделения
Дренаж в коллектор НД расширителя дренажей турбинного отделения
Дренаж в дренажный бак турбинного отделения
В деаэратор 10LAA11BB001
В деаэратор 10LAA12BB001
В деаэратор 10LAA13BB001
Из отбора турбины №1
Из отбора турбины №2
Из резервного коллектора пара с. н.
От РОУ 1
От РОУ 2
От РОУ 3
РОУ с.н. 8,3 т/ч
Охлаждающее устройство (ОУ) 250 т/ч
Пар на эжекторы и уплотнения турбины №1
Пар на эжекторы и уплотнения турбины №2
От уравнительного коллектора деаэраторов
Воздушник
Комплектно с ОУ
Комплектно с РОУ
Эжектор пусковой ПТ №1
Эжектор пусковой ПТ №2
Эжектор расхолаживания ПТ №1
Эжектор расхолаживания ПТ №2
Дренаж
Дренаж 10
Дренаж 11
Дренаж 12
Дренаж 13
Дренаж 14
Дренаж 15
Дренаж 16
Дренаж 17
Дренаж 18
Дренаж 19
Дренаж 20
Дренаж 21
Дренаж 4
Дренаж 5
Дренаж 6
Дренаж 7
Дренаж 8
Дренаж 9
Дренаж A
Дренаж B
Дренаж C
Дренаж D
Дренаж E
Дренаж F
Дренаж G
Дренаж H
Дренаж I
Дренаж J
Дренаж K
Дренаж L
Дренаж M
Дренаж N
Дренаж O
Дренаж P
Дренаж Q
Дренаж R
Дренаж T
Дренаж U
Дренаж V
Дренаж W
Дренаж X
Дренаж Y
Дренаж Z
141N4 – 10UHJ – 4010 – TD.M
Амурская ТЭС. Обеспечение нужд Амурского ГПЗ. Строительство основного технологического комплекса объектов Амурской ТЭС (2 ПСУ х80МВт). Этап 1."Амурская ТЭС (ПСУ-2х80 МВт)"
Главный корпус. PI-диаграмма трубопроводов пара собственных нужд
PI-диаграмма трубопроводов пара собственных нужд. Система LBG, LAE, LBD
Разработал Калинкина
Проверил Майорова
Н. контр. Грядчина
Стадия P
Лист 2
Листов
АКЦИОНЕРНОЕ ОБЩЕСТВО ИНСТИТУТ ТЕПЛОЭЛЕКТРОПРОЕКТ Г. МОСКВА
Согласовано
ОАСУ Соболева
Взам. инв. №
Подпись и дата
Инв. № подл.
Формат А1