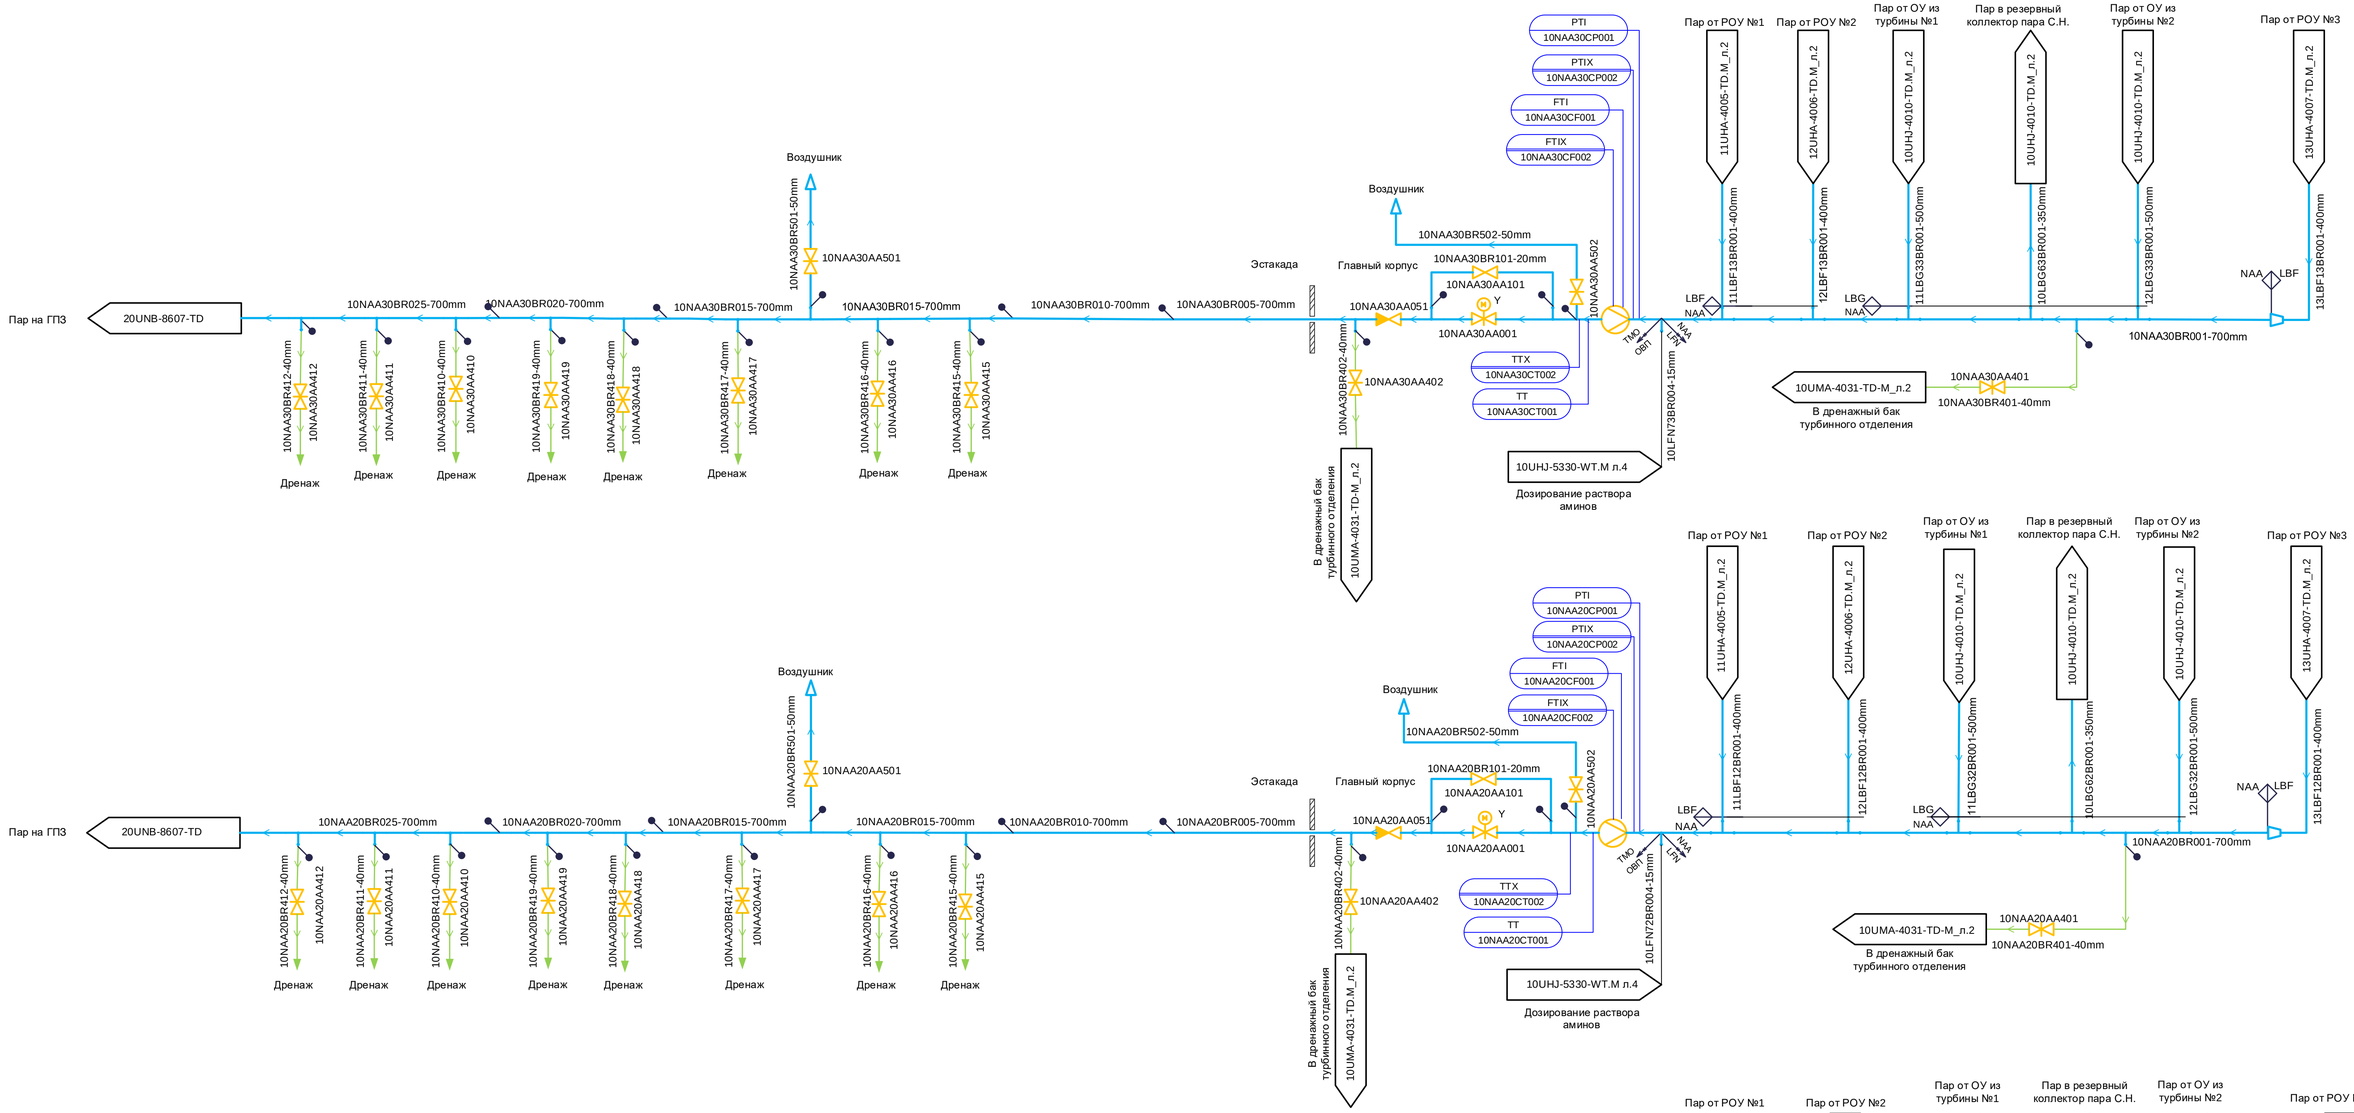


| | | | | | | |
|---|---|---|---|---|---|---|
| 1 | - | Зам | 1102-19 | | | |
| Изм. | Кол.уч | Лист | № док. | Подп. | Дата | |
| Разработал | | Полянская | | | | |
| Проверил | | Калинкина | | | | |
| Зам.нач.отд | | Майорова | | | | |
| Н. контр. | | Грядчина | | | | |

141N4 – 10UHJ – 4011 – TD.M

Амурская ТЭС. Обеспечение нужд Амурского ГПЗ.
Строительство основного технологического комплекса объектов Амурской ТЭС (2ПСУх80 МВт). Этап 1. "Амурская ТЭС (2х80 МВт)".

Главный корпус

PI-диаграмма трубопроводов пара на производство

PI-диаграмма трубопроводов пара на производство. Система NAA.

| Стадия | Лист | Листов |
|---|---|---|
| Р | 2 | |

АКЦИОНЕРНОЕ ОБЩЕСТВО ИНСТИТУТ ТЕПЛОЭЛЕКТРОПРОЕКТ г. МОСКВА

Согласовано

| | |
|---|---|
| ОАСУ | Соболева |

Взам. инв. №

Подпись и дата

Инв. № подл.

Формат А1