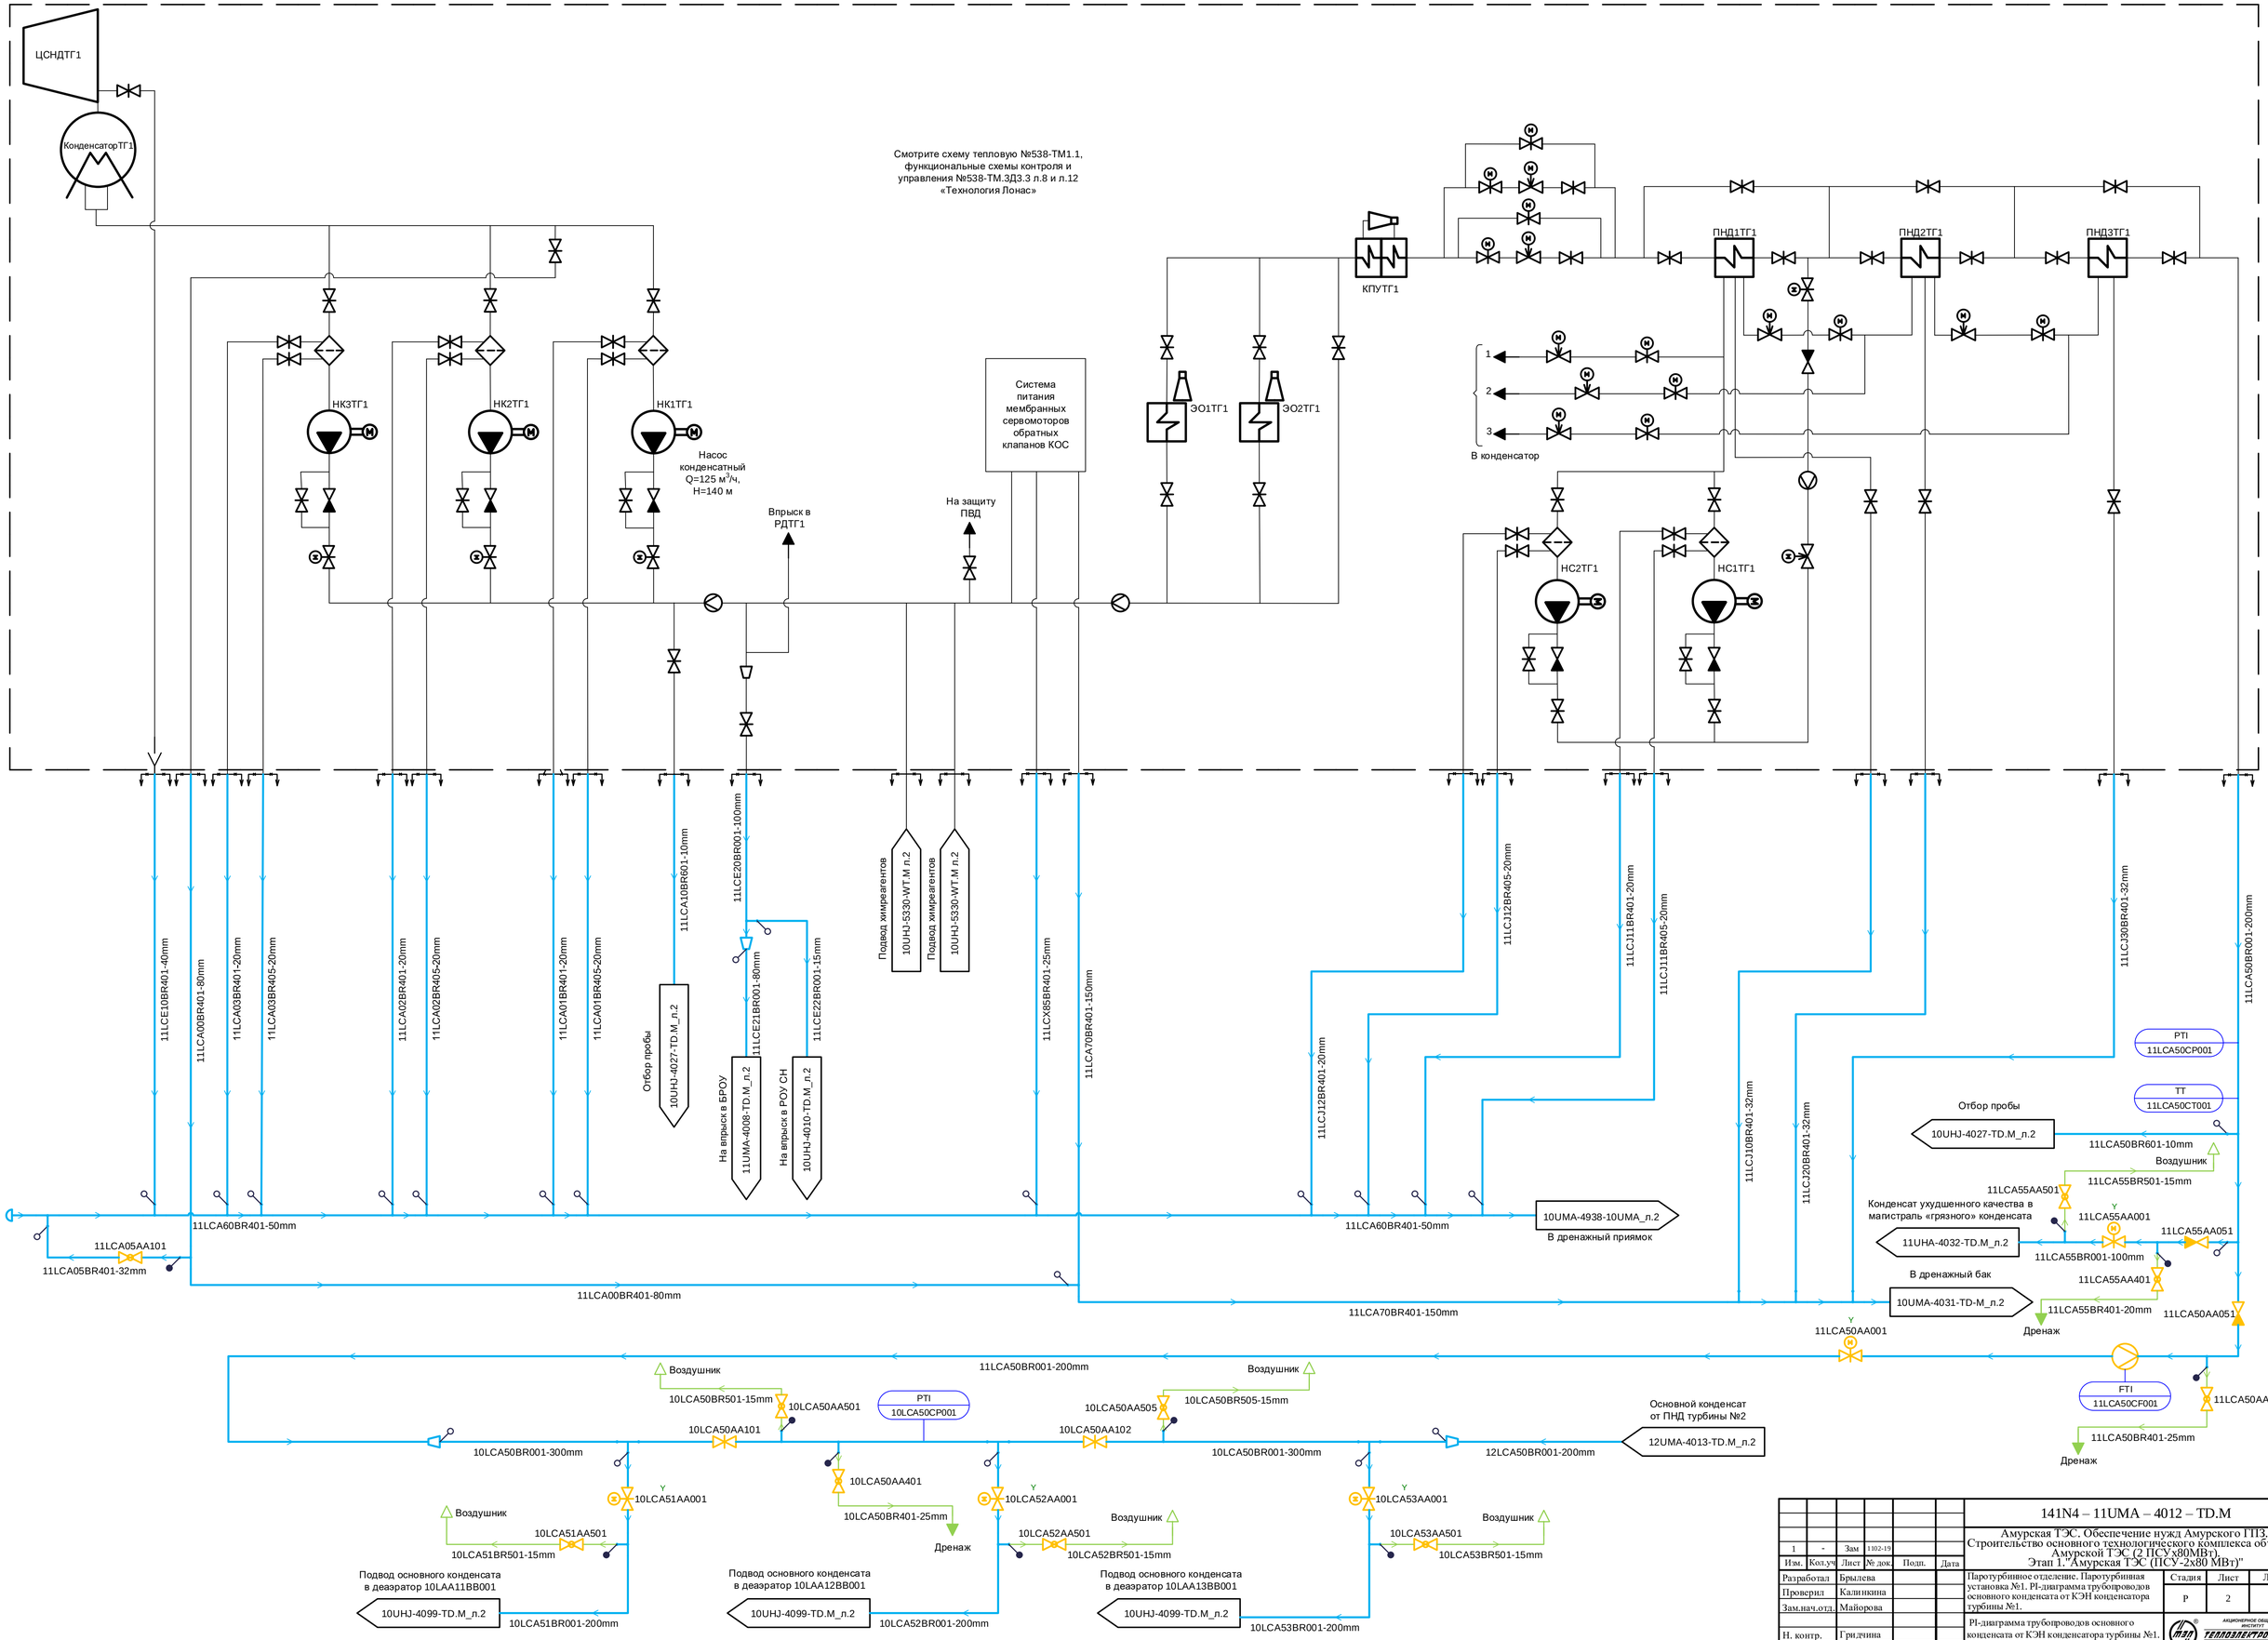

1	-	Зам	1102-19			
Изм.	Кол.уч	Лист	№ док.	Подп.	Дата	

141N4 – 11UMA – 4012 – TD.M

Амурская ТЭС. Обеспечение нужд Амурского ГПЗ. Строительство основного технологического комплекса объектов Амурской ТЭС (2 ПСУ х80МВт). Этап 1."Амурская ТЭС (ПСУ-2х80 МВт)"

Разработал	Брылева	
Проверил	Калинкина	
Зам.нач.отд.	Майорова	
Н. контр.	Грядчина	

Паротурбинное отделение. Паротурбинная установка №1. PI-диаграмма трубопроводов основного конденсата от КЭН конденсатора турбины №1.

PI-диаграмма трубопроводов основного конденсата от КЭН конденсатора турбины №1. Система LCA, LCE, LCJ, LCX.

Стадия	Лист	Листов
Р	2	

АКЦИОНЕРНОЕ ОБЩЕСТВО ИНСТИТУТ ТЕПЛОЭЛЕКТРОПРОЕКТ Г. МОСКВА

Согласовано
ОАСУ Соболева
Взам. инв. №
Подпись и дата
Инв. № подл.

Формат А1