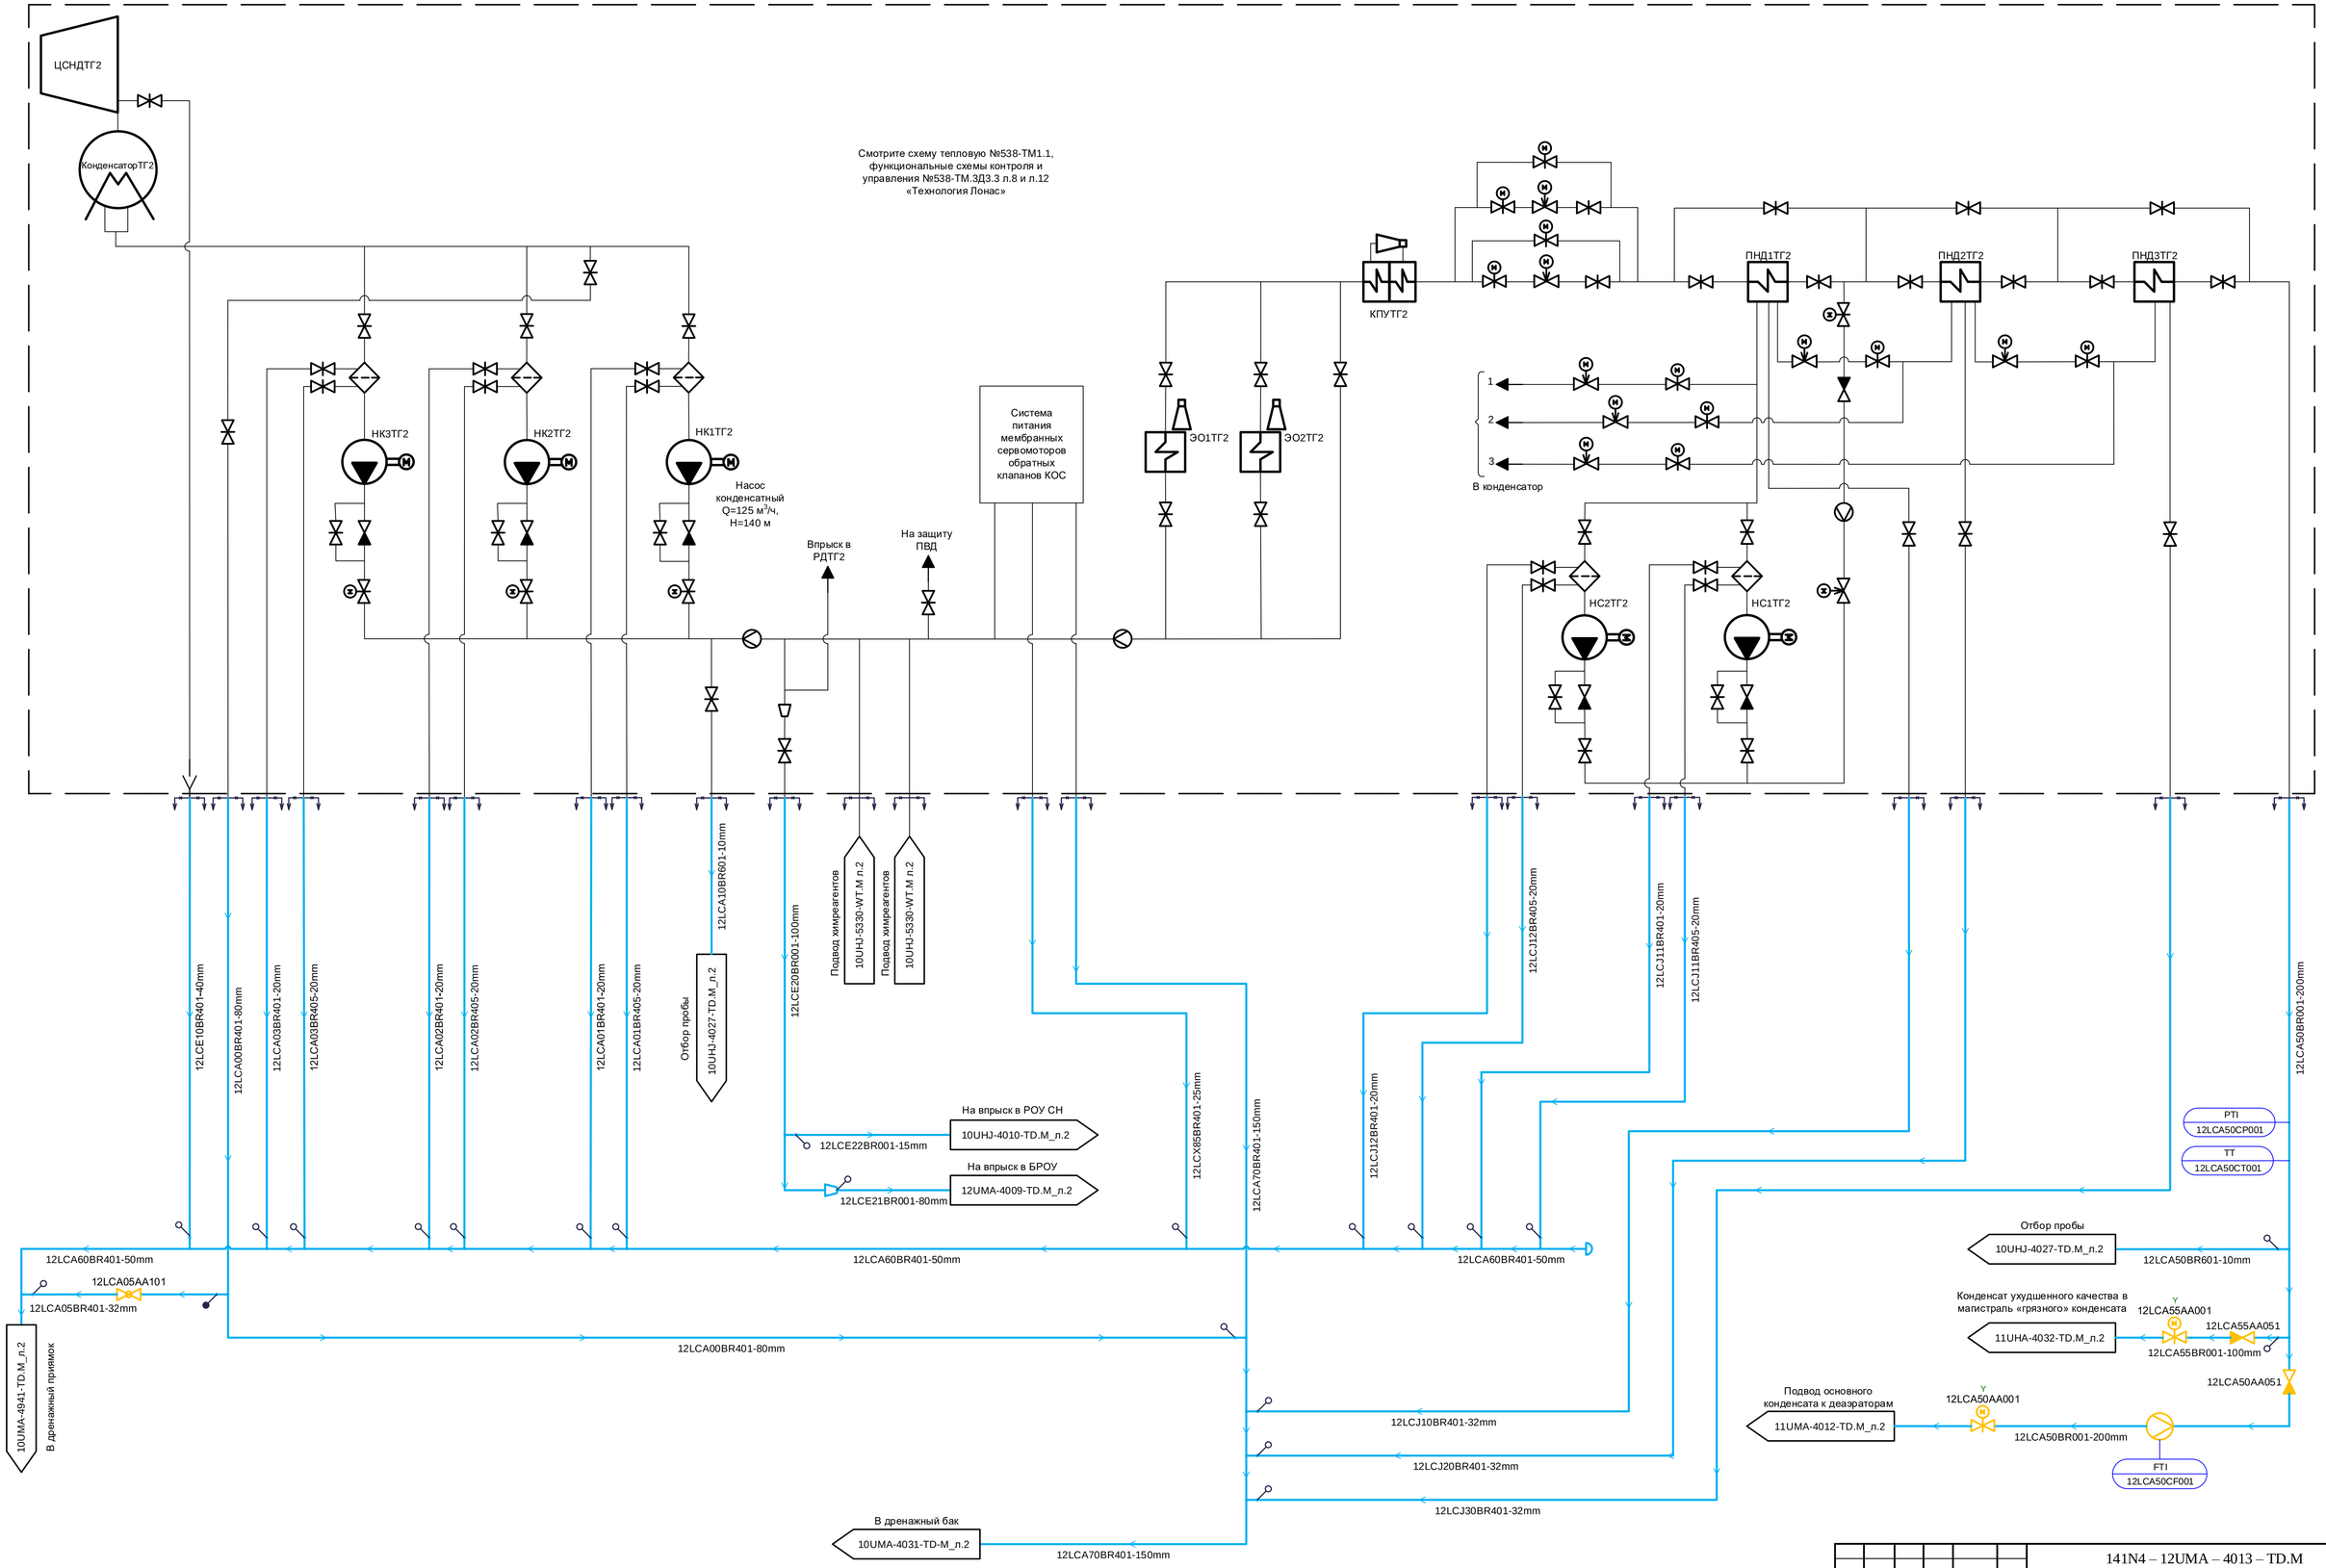

Изм.	Кол.уч	Лист	№ док.	Подп.	Дата	141N4 – 12UMA – 4013 – TD.M
						Амурская ТЭС. Обеспечение нужд Амурского ГПЗ. Строительство основного технологического комплекса объектов Амурской ТЭС (2 ПСУ х80МВт). Этап 1."Амурская ТЭС (ПСУ-2х80 МВт)"
Разработал		Брылева				Паротурбинное отделение. Паротурбинная установка №2. PI-диаграмма трубопроводов основного конденсата от КЭН конденсатора турбины №2.
Проверил		Калинкина				Стадия: Р; Лист: 2; Листов:
Зам.нач.отд.		Майорова				
Н. контр.		Гридчина				PI-диаграмма трубопроводов основного конденсата от КЭН конденсатора турбины №2. Система LCA, LCE, LCJ, LCX.

АКЦИОНЕРНОЕ ОБЩЕСТВО ИНСТИТУТ ТЕПЛОЭЛЕКТРОПРОЕКТ Г. МОСКВА

Согласовано: ОАСУ, Соболева

Взам. инв. №

Подпись и дата

Инв. № подл.

Формат А1