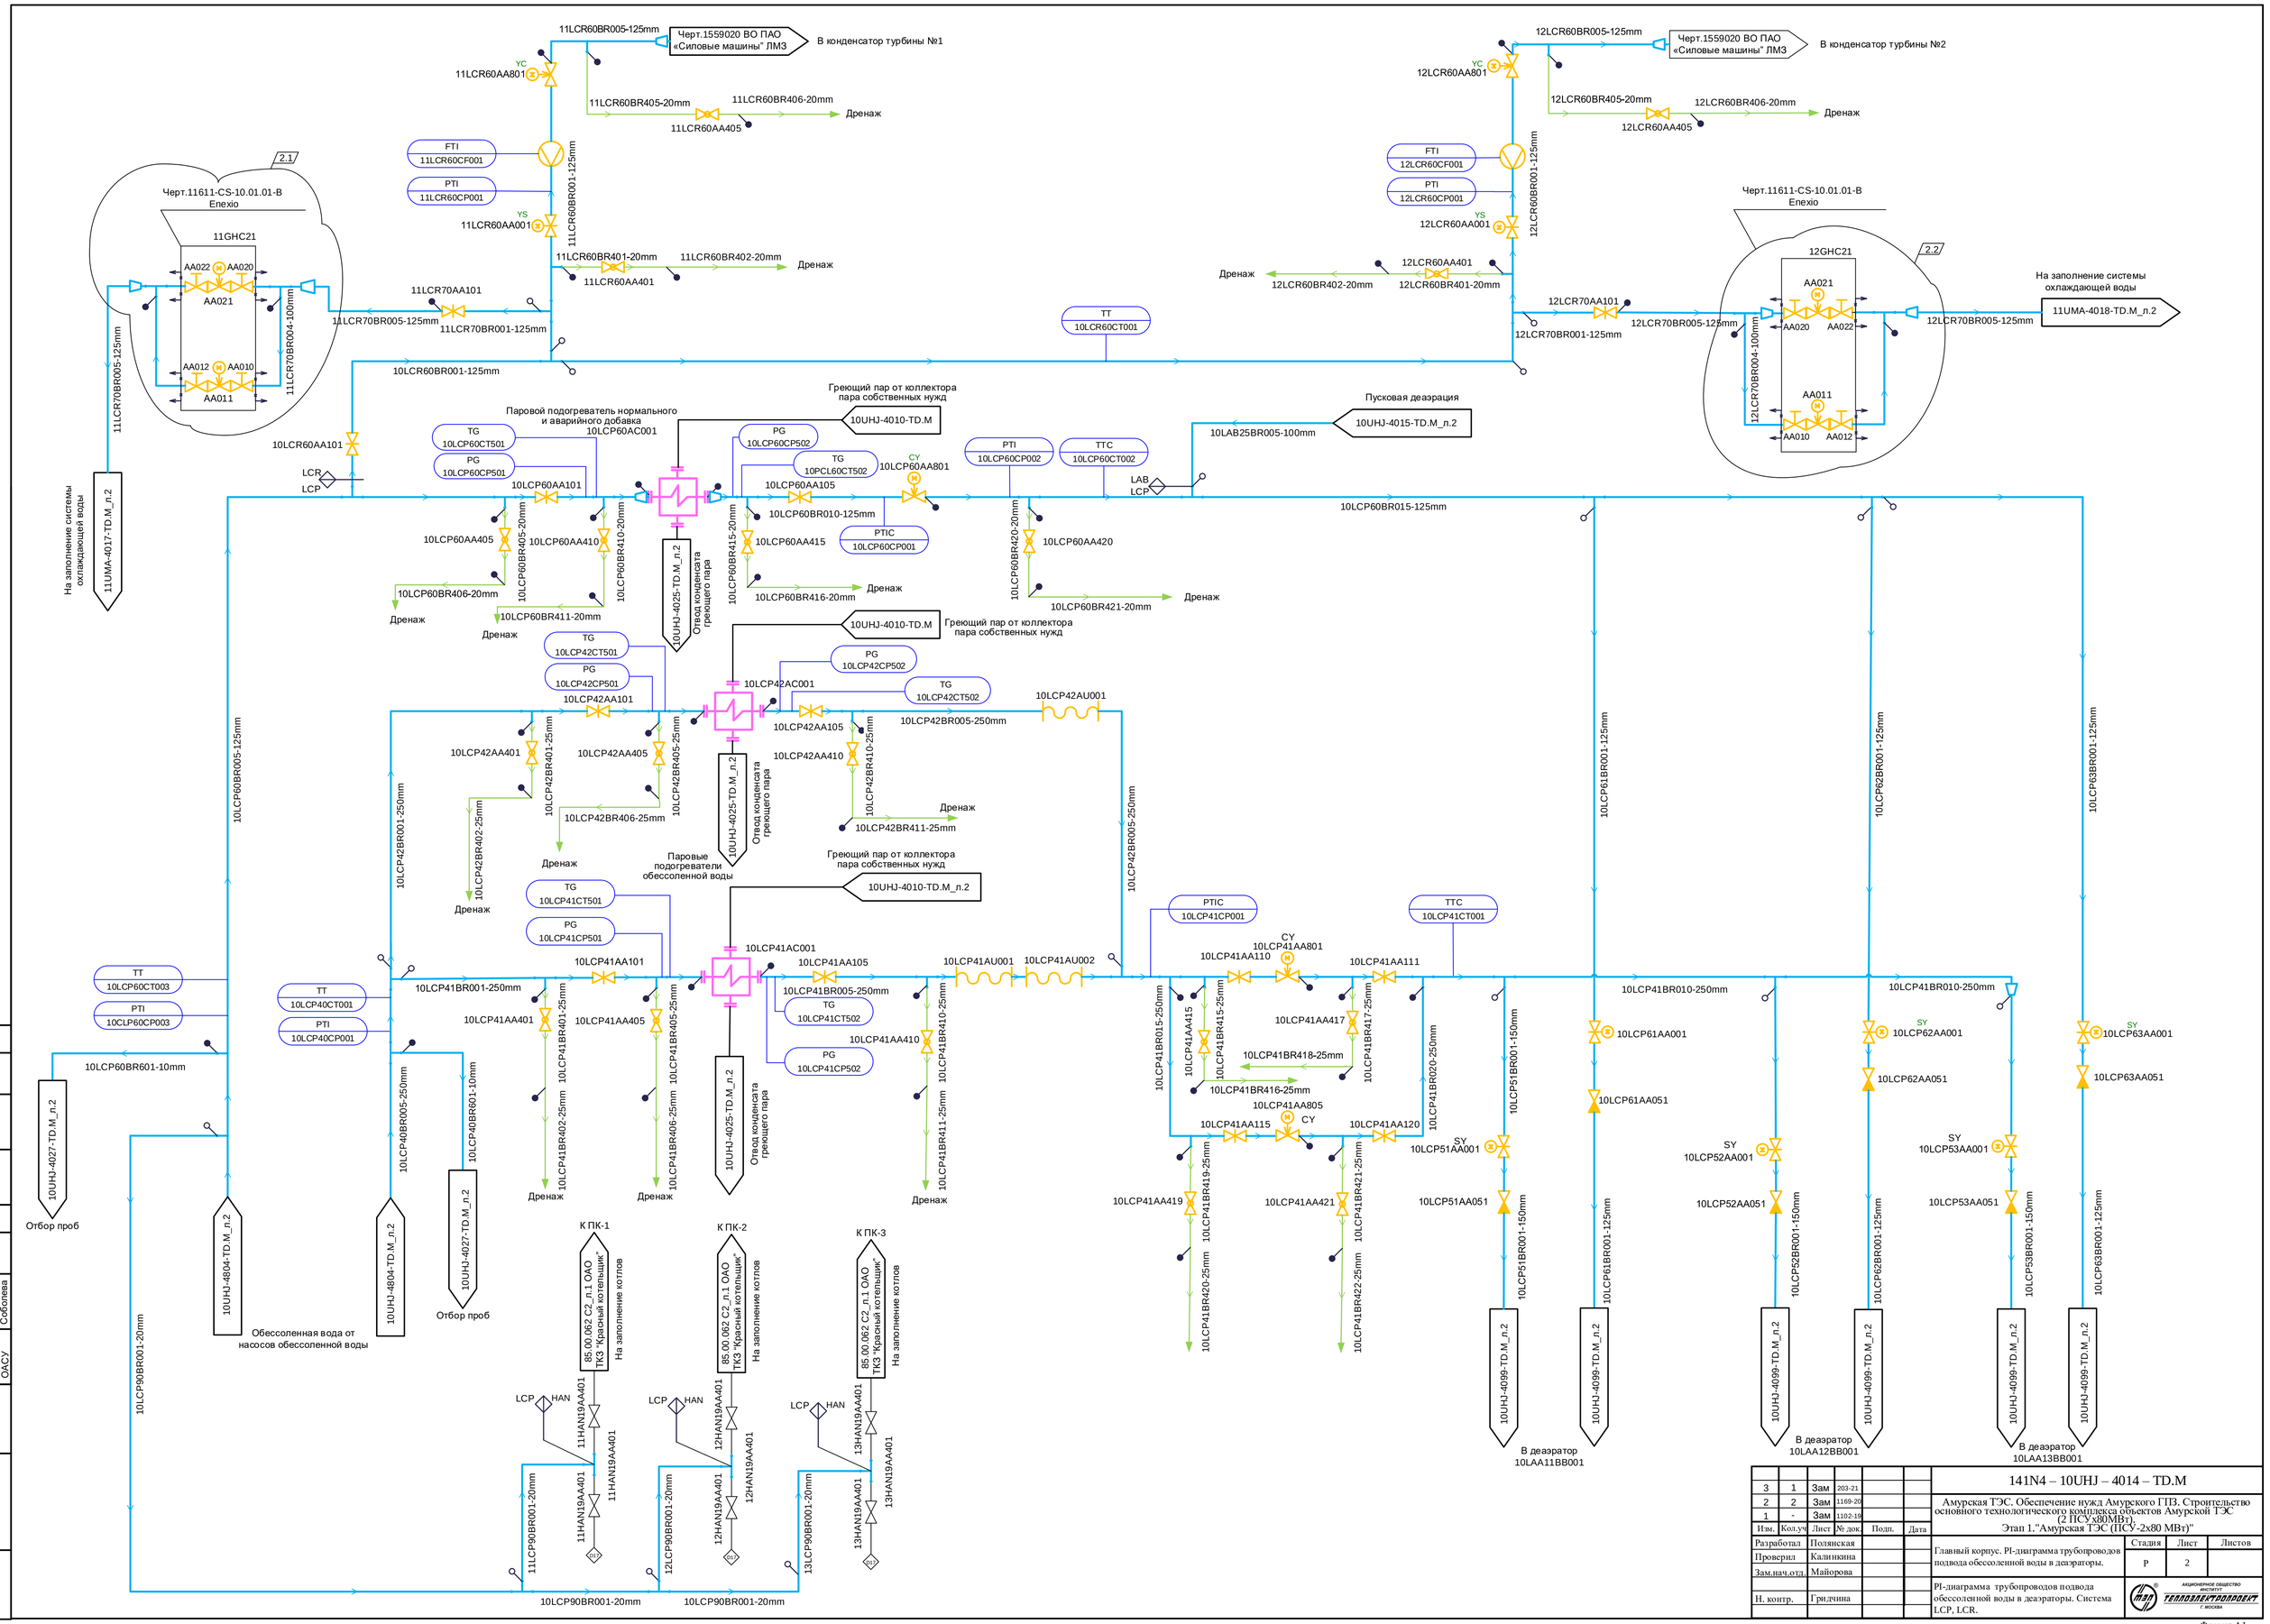

3	1	Зам	203-21			
2	2	Зам	1169-20			
1	-	Зам	1102-19			
Изм.	Кол.уч	Лист	№ док.	Подп.	Дата	

141N4 – 10UHJ – 4014 – TD.M

Амурская ТЭС. Обеспечение нужд Амурского ГПЗ. Строительство основного технологического комплекса объектов Амурской ТЭС (2 ПСУ х80МВт).
Этап 1."Амурская ТЭС (ПСУ-2х80 МВт)"

Разработал	Полянская	
Проверил	Калинкина	
Зам.нач.отд.	Майорова	
Н. контр.	Грядчина	

Главный корпус. PI-диаграмма трубопроводов подвода обессоленной воды в деаэраторы.

Стадия	Лист	Листов
Р	2	

PI-диаграмма трубопроводов подвода обессоленной воды в деаэраторы. Система LCP, LCR.

АКЦИОНЕРНОЕ ОБЩЕСТВО ИНСТИТУТ ТЕПЛОЭЛЕКТРОПРОЕКТ г. МОСКВА

Согласовано
ОАСУ Соболева
Взам. инв. №
Подпись и дата
Инв. № подл.

Формат А1