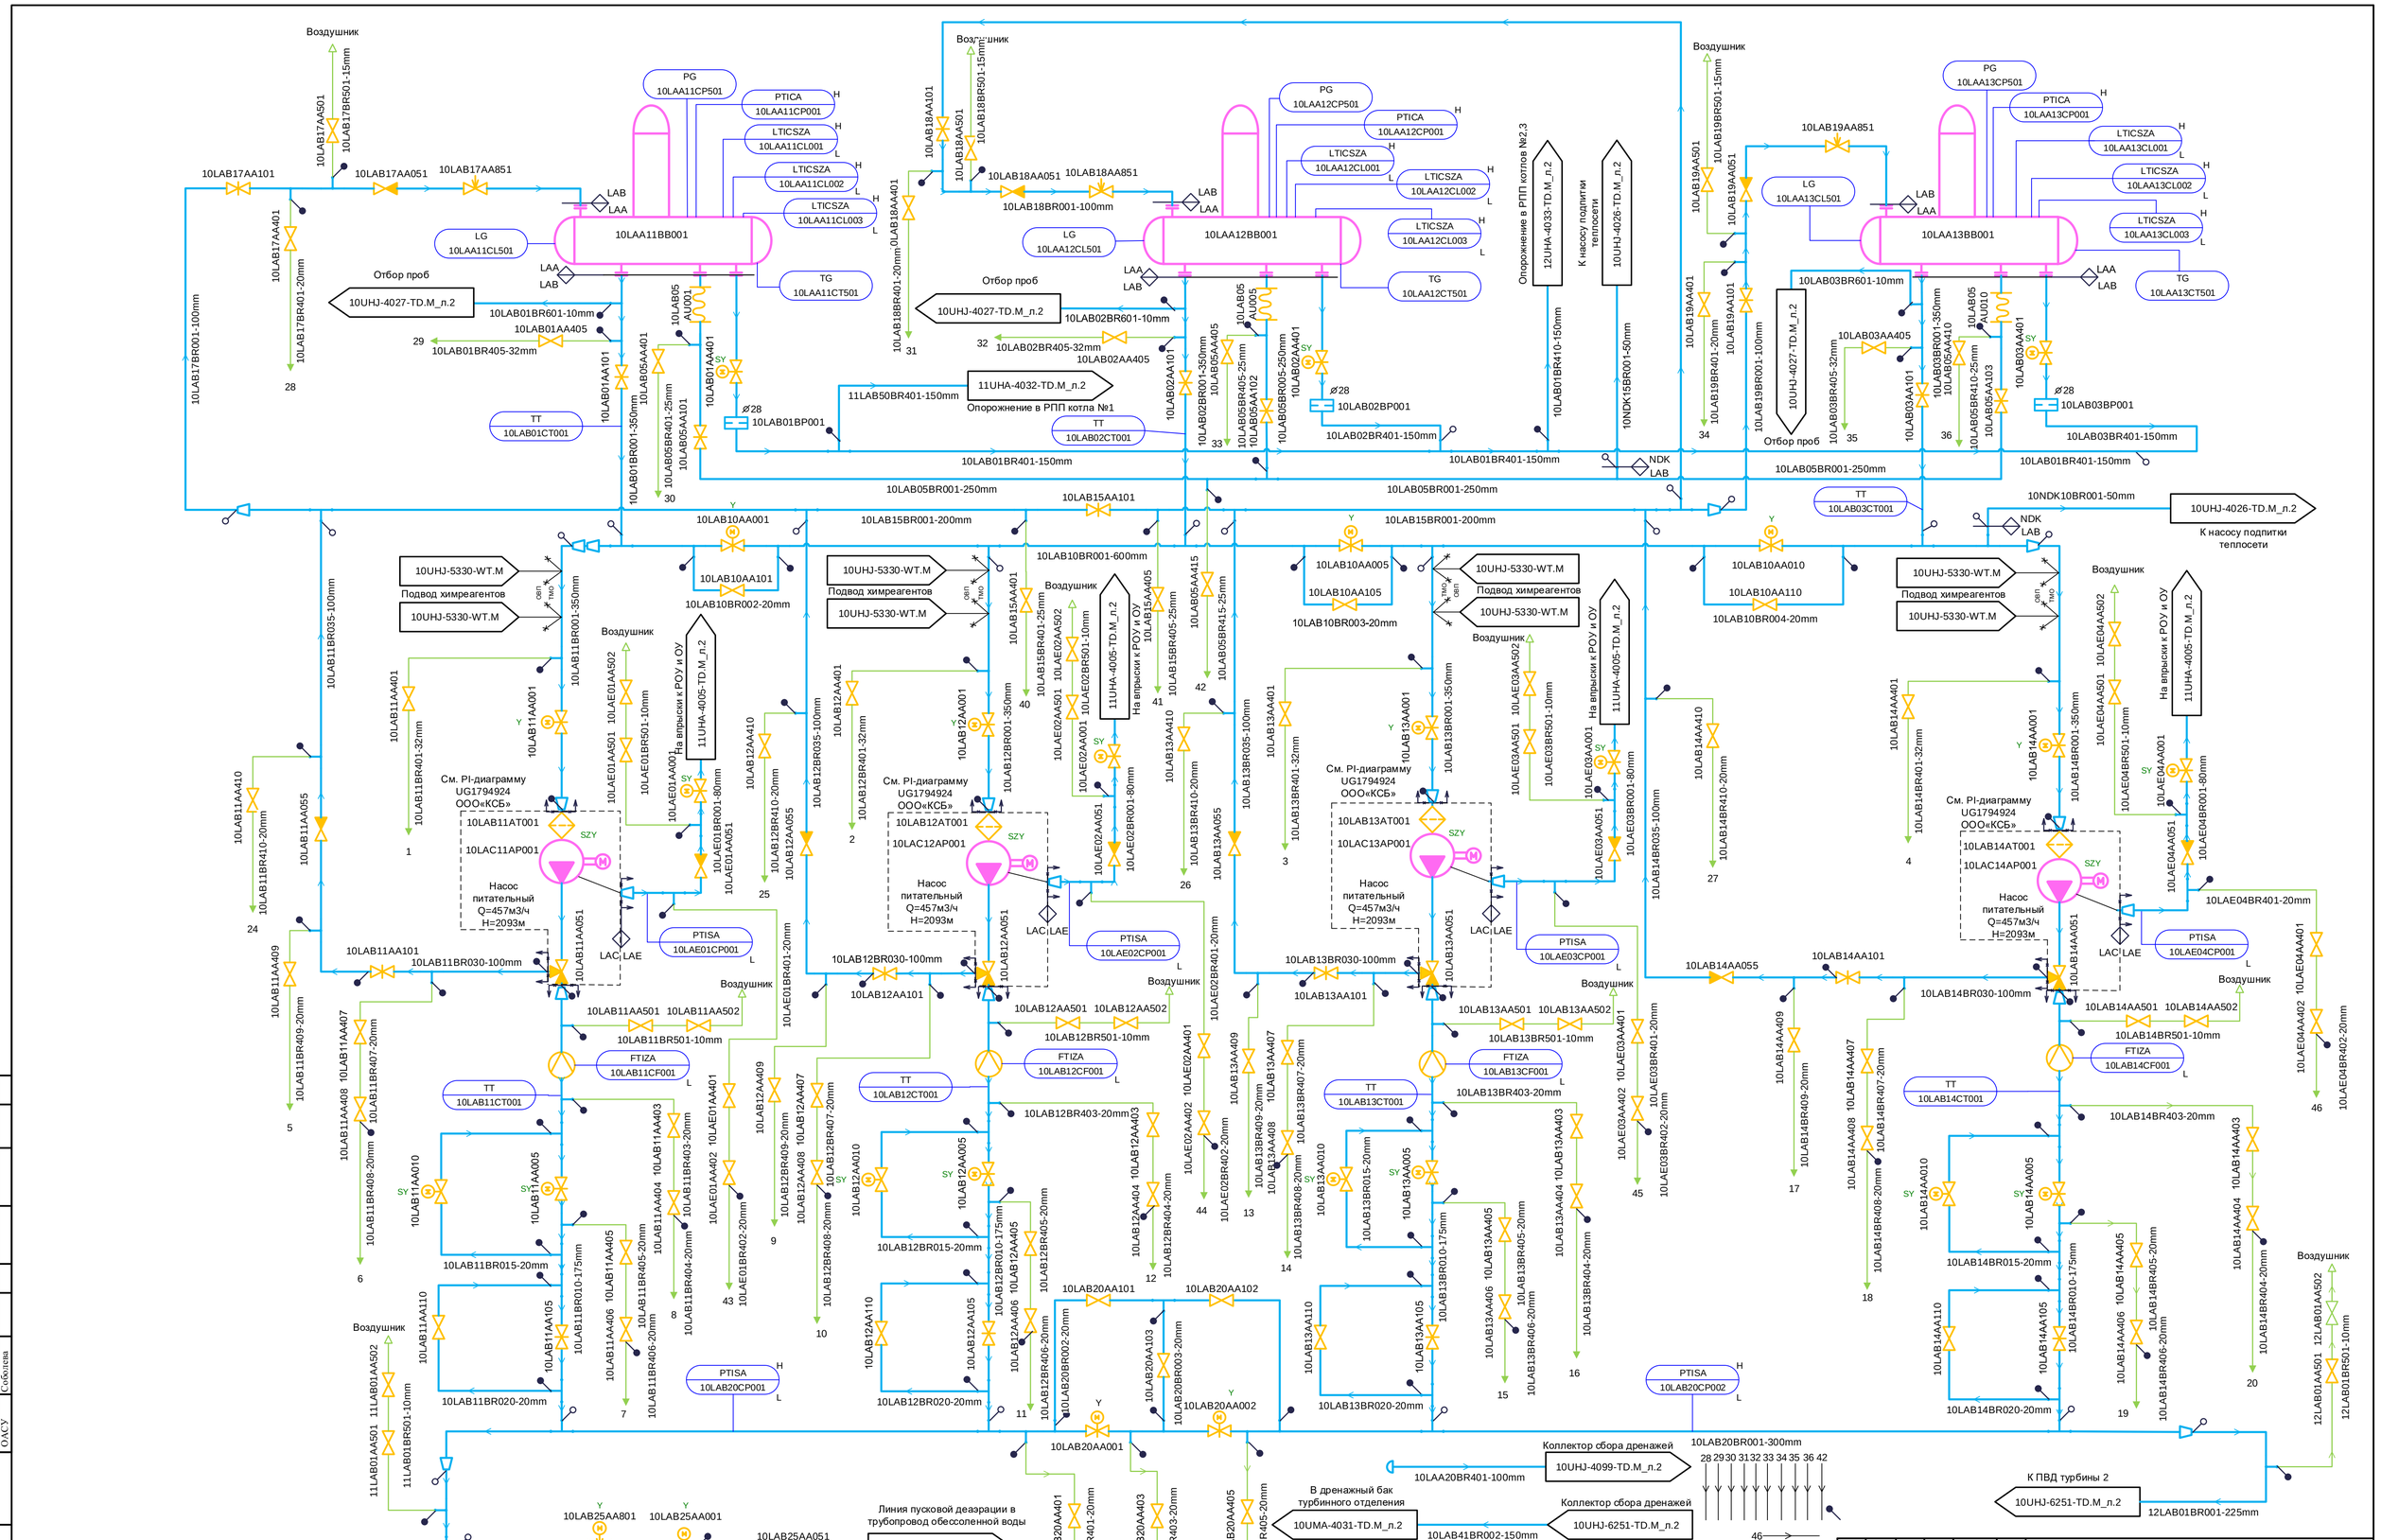
10LAA11BB001
10LAA12BB001
10LAA13BB001
Насос питательный Q=457м3/ч H=2093м
См. PI-диаграмму UG1794924 ООО«КСБ»
Подвод химреагентов
Отбор проб
Воздушник
К ПВД турбины 1
К ПВД турбины 2
Линия пусковой деаэрации в трубопровод обессоленной воды
Коллектор сбора дренажей
В дренажный бак турбинного отделения
Опорожнение в РПП котлов №2,3
Опорожнение в РПП котла №1
К насосу подпитки теплосети
На впрыски к РОУ и ОУ
141N4 – 10UHJ – 4015 – TD.M
Амурская ТЭС. Обеспечение нужд Амурского ГПЗ. Строительство основного технологического комплекса объектов Амурской ТЭС (2ПСУ×80 МВт). Этап 1. "Амурская ТЭС (ПСУ-2×80 МВт)".
Изм. Кол.уч Лист № док. Подп. Дата
Разработал Дёмина
Проверил Калинкина
Зам.нач.отд. Майорова
Н. контр. Астраханцев
Главный корпус. PI-диаграмма трубопроводов питательной воды ПЭН
PI-диаграмма трубопроводов питательной воды ПЭН. Система LAB, LAE
Стадия Лист Листов
Р 2
АКЦИОНЕРНОЕ ОБЩЕСТВО ВНИПИЭТ ТЕПЛОЭЛЕКТРОПРОЕКТ г. МОСКВА
Согласовано
ОАСУ Соболева
Взам. инв. №
Подпись и дата
Инв. № подл.
Формат А1