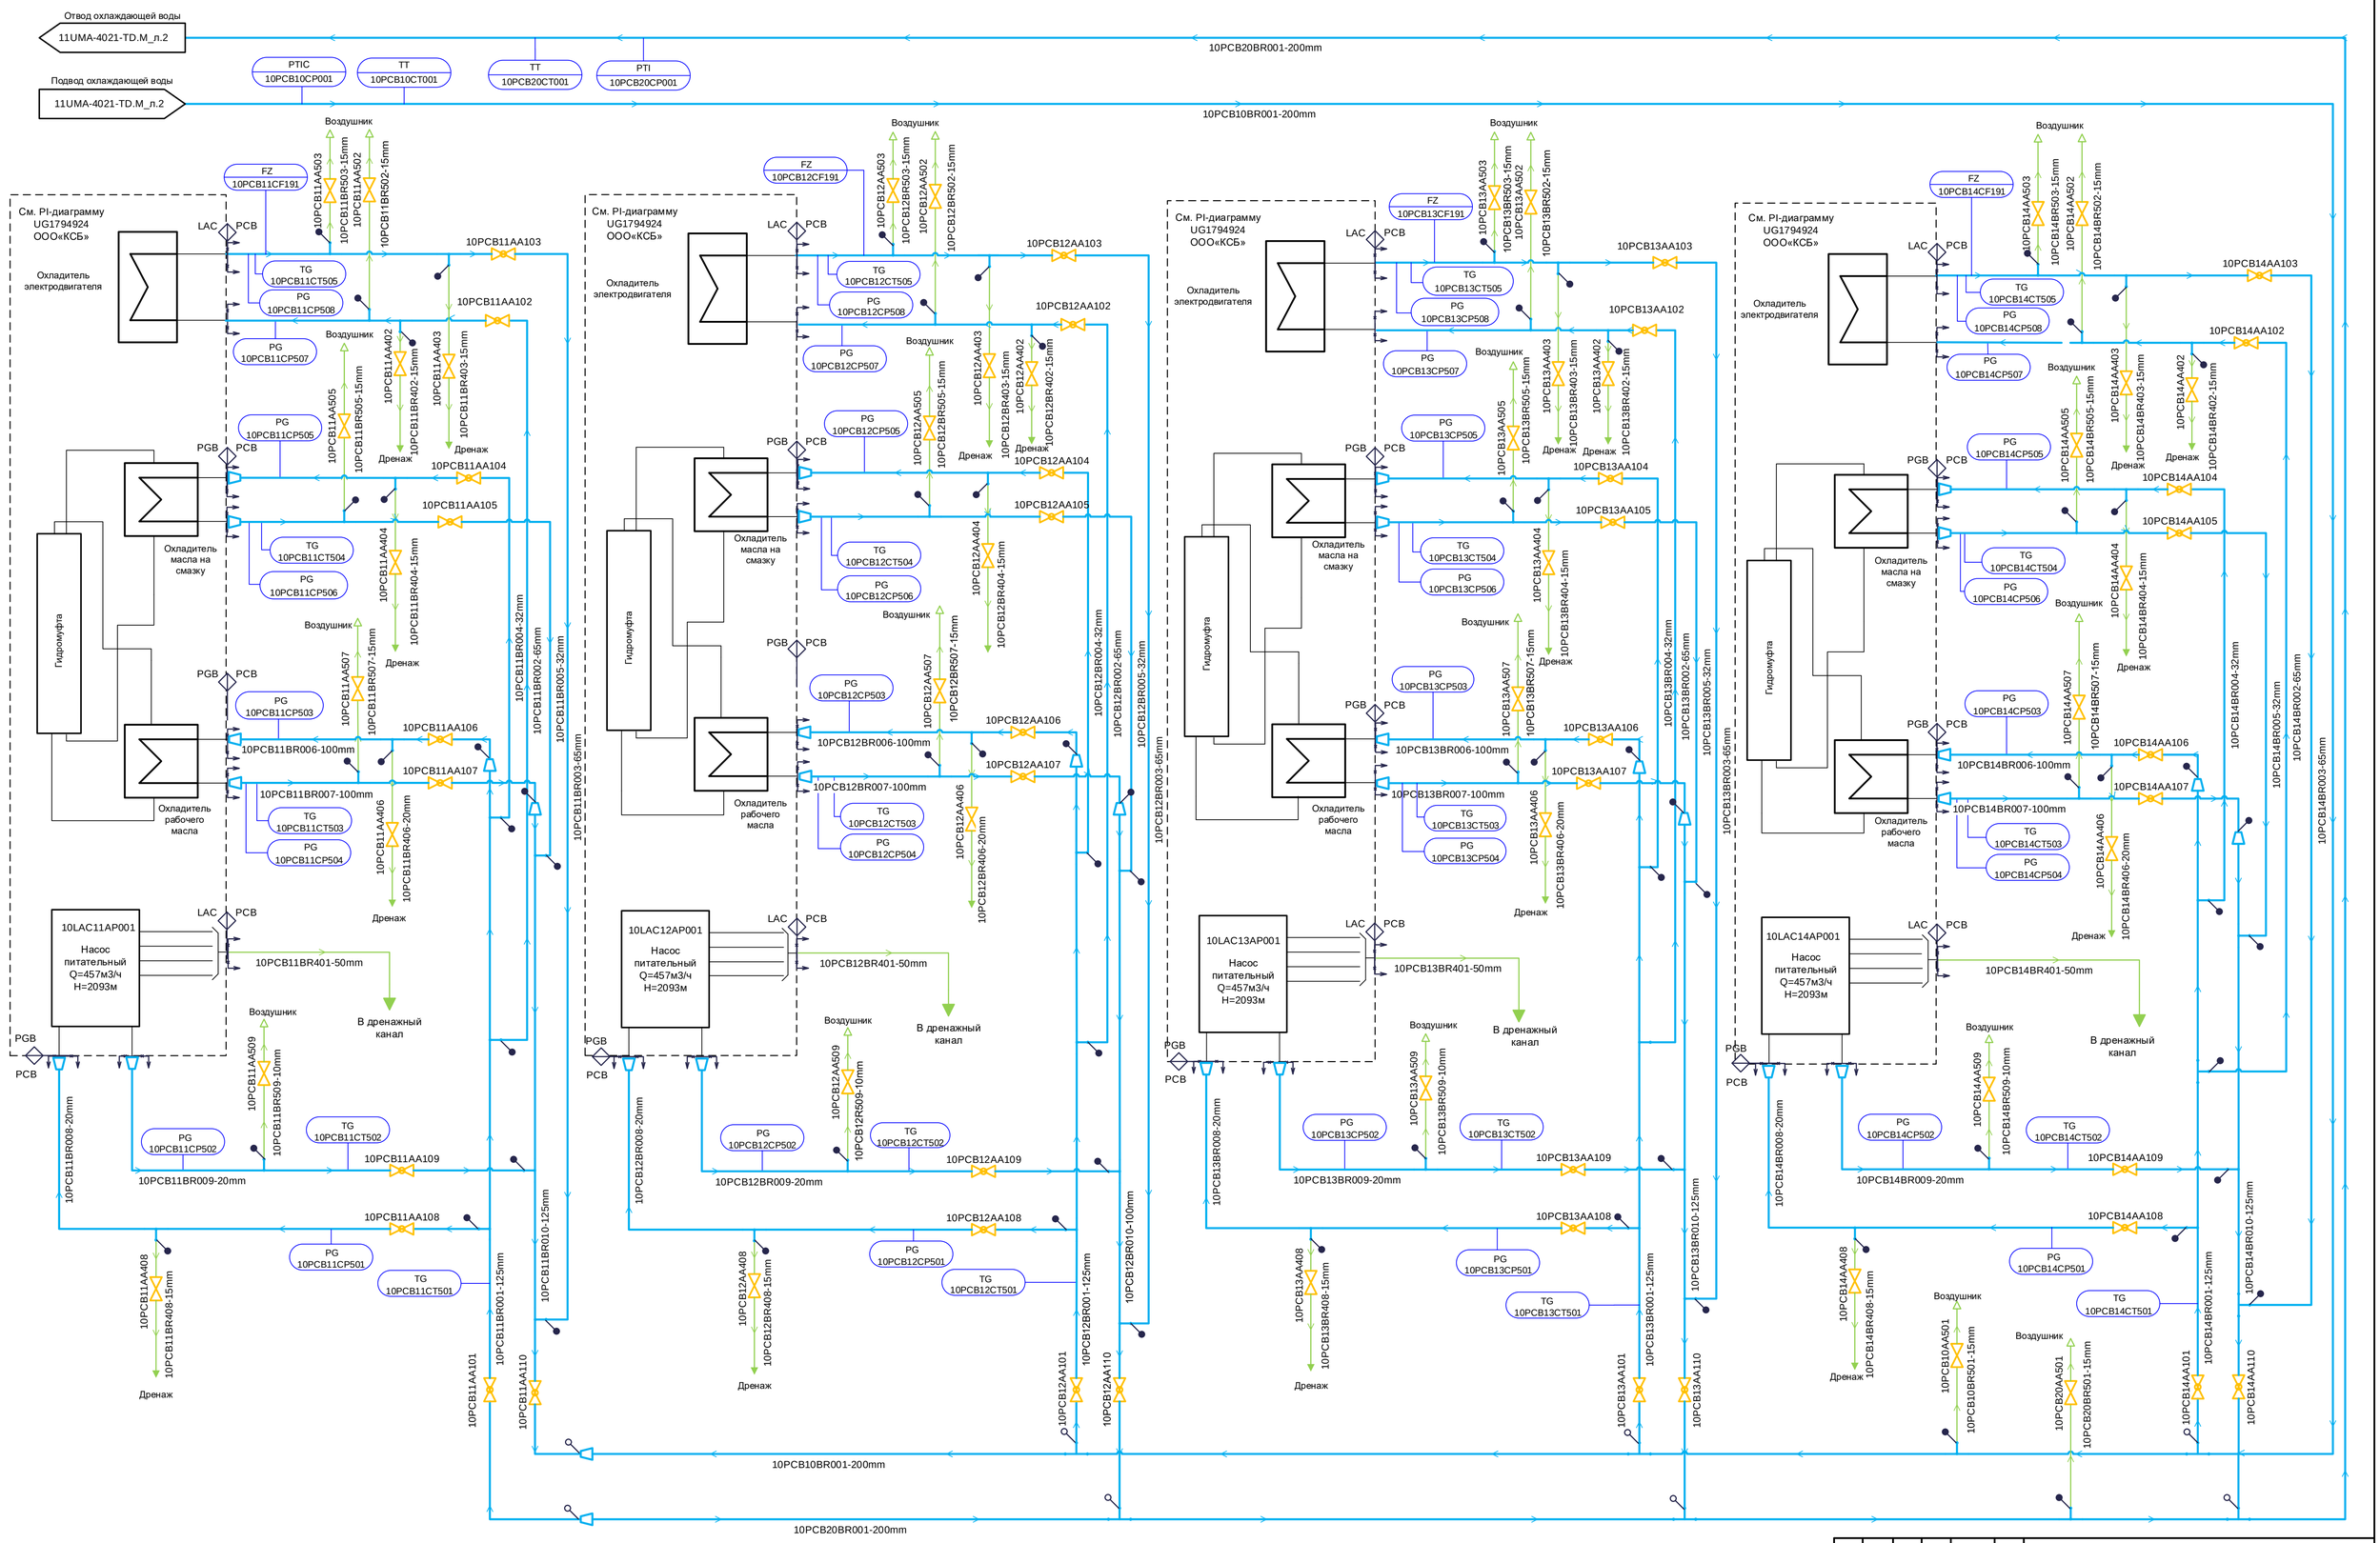

1	-	Зам.	1172-20		12.20	
Изм.	Кол.уч	Лист	№ док.	Подп.	Дата	

141N4 – 10UHJ – 4016 – TD.M

Амурская ТЭС. Обеспечение нужд Амурского ГПЗ. Строительство основного технологического комплекса объектов Амурской ТЭС (2ПСУх80 МВт). Этап 1. "Амурская ТЭС (ПСУ-2х80 МВт)".

Разработал	Дёмина	
Проверил	Калинкина	
Зам.нач.отд.	Майорова	
Н. контр.	Черемушкина	

Главный корпус, PI-диаграмма вспомогательных трубопроводов ПЭН

Стадия	Лист	Листов
Р	2	

PI-диаграмма вспомогательных трубопроводов ПЭН. Система PCB

АКЦИОНЕРНОЕ ОБЩЕСТВО ИНСТИТУТ ТЕПЛОЭЛЕКТРОПРОЕКТ г. МОСКВА

Согласовано

ОАСУ Соболева

Взам. инв. №

Подпись и дата

Инв. № подл.

Формат А1