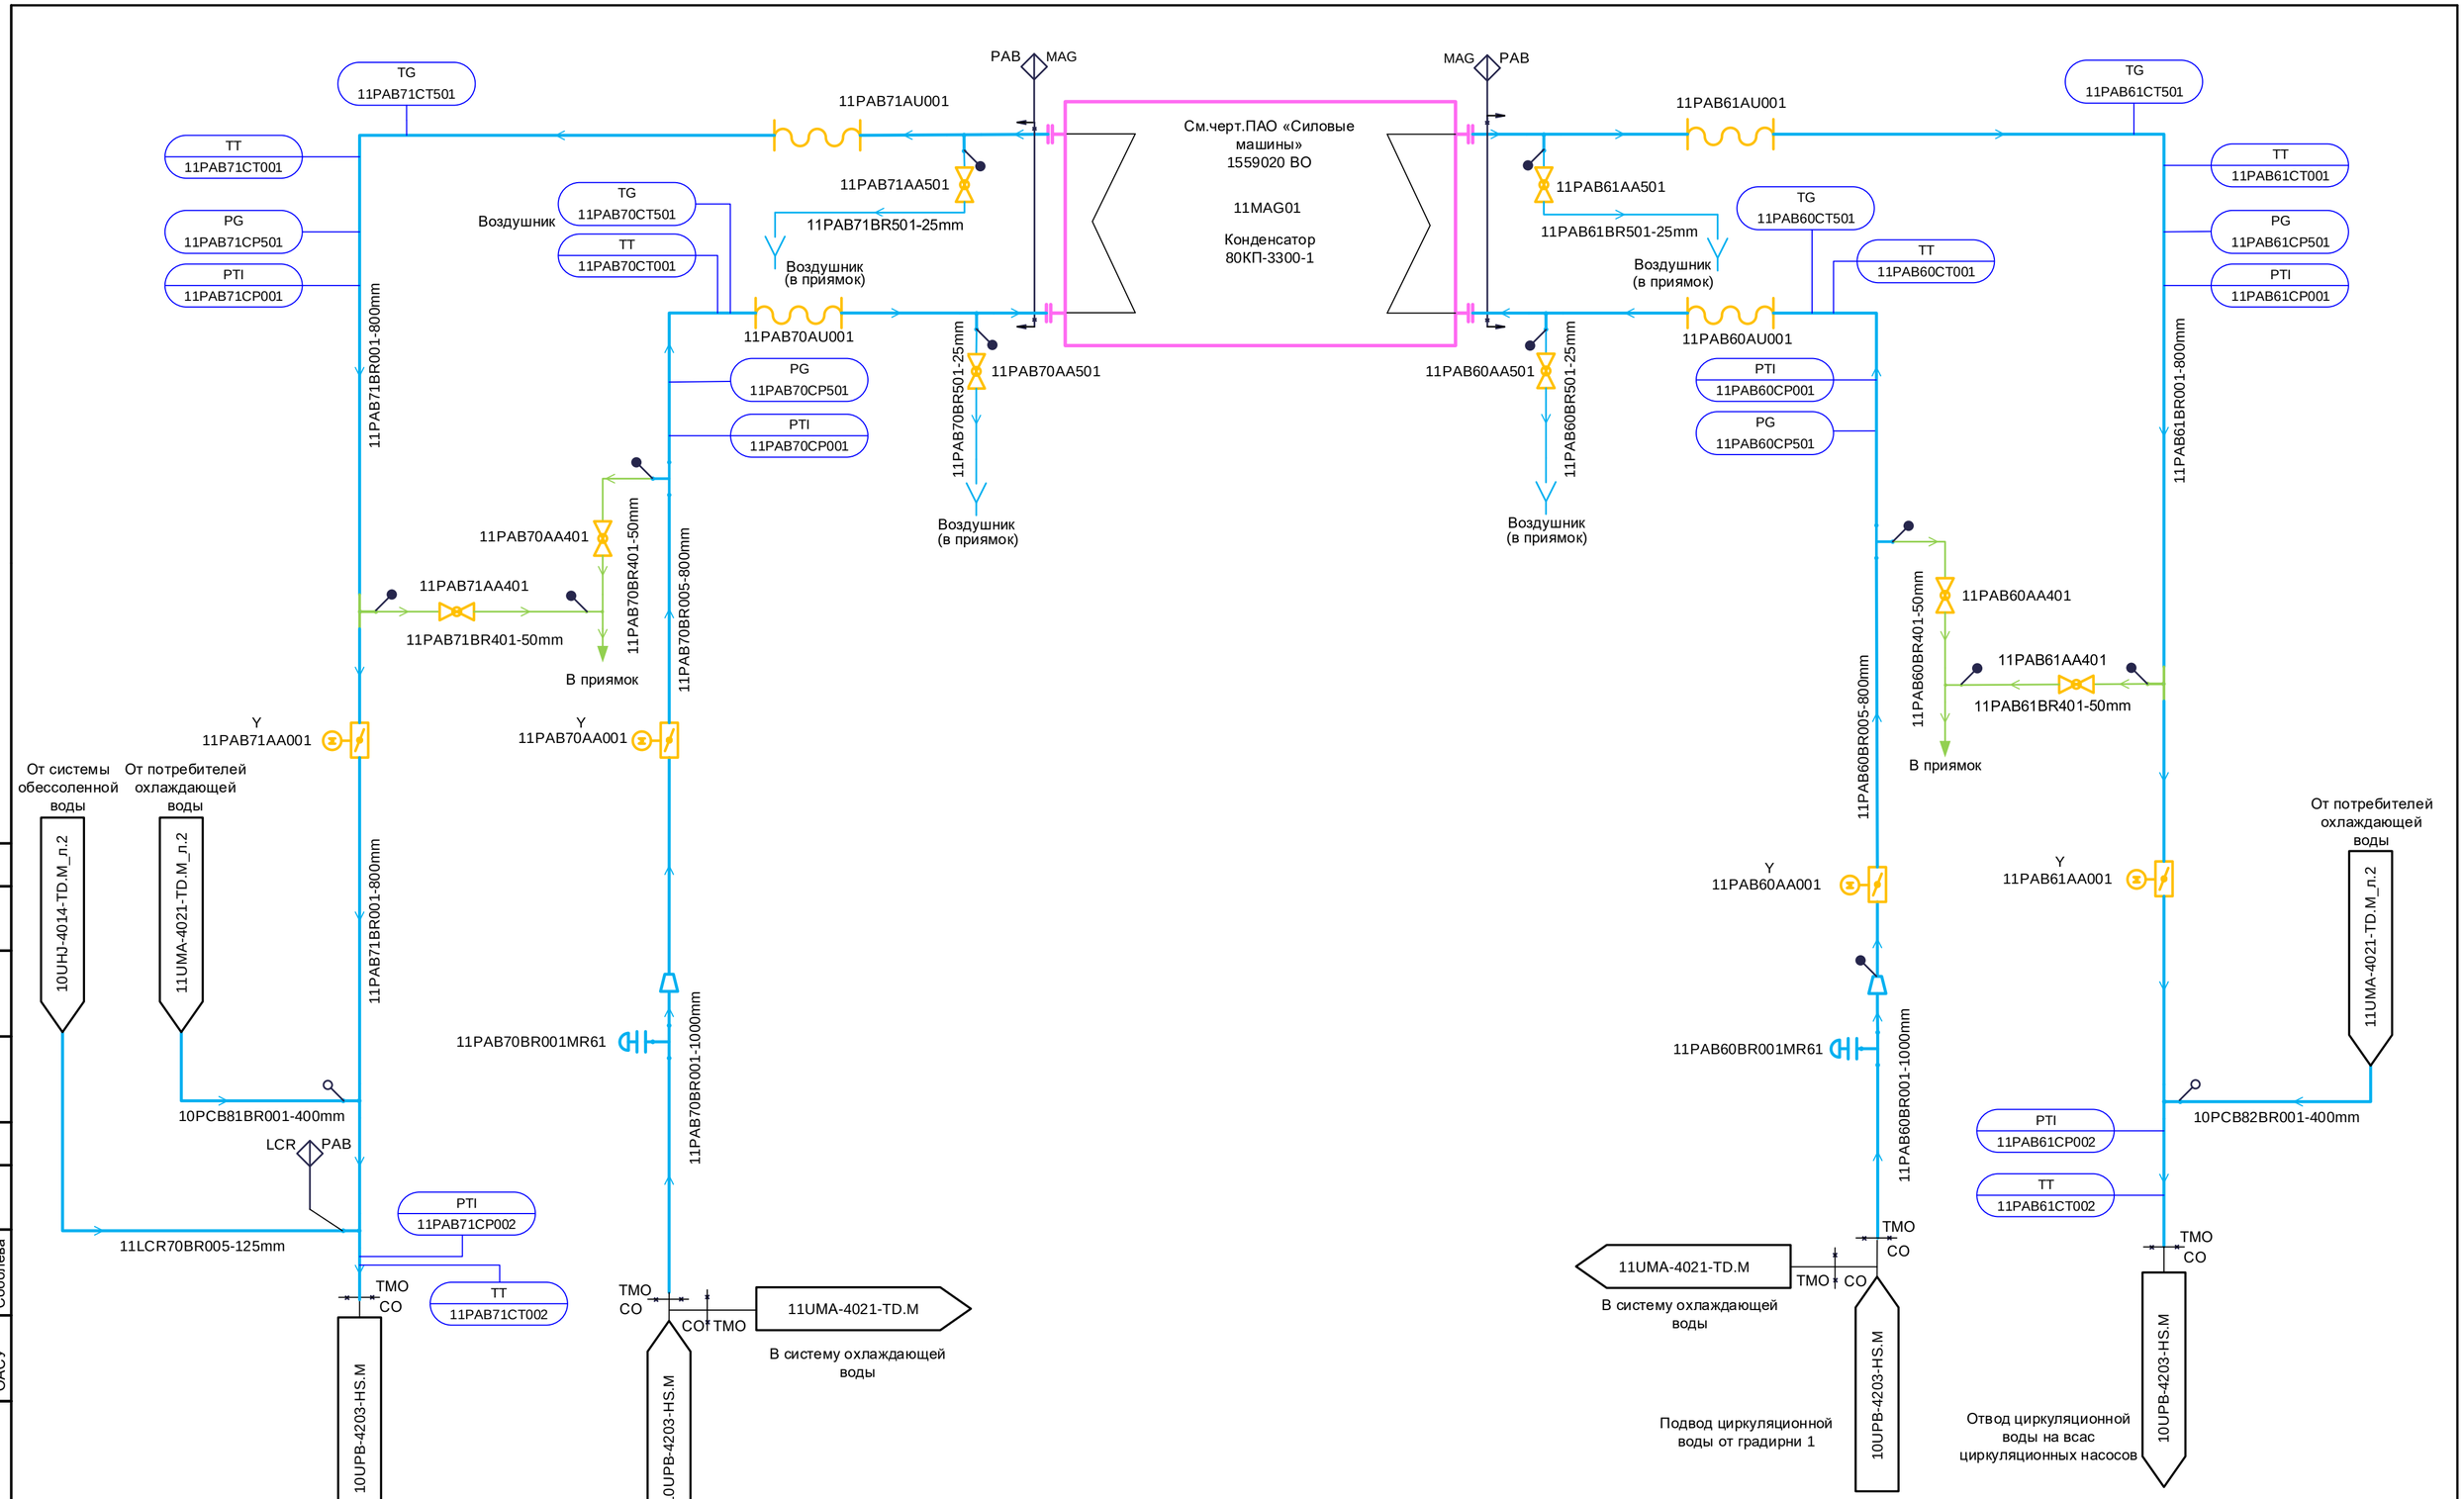

1	-	Зам	1102-19			
Изм.	Кол.уч	Лист	№ док.	Подп.	Дата	
Разработал		Полянская				
Проверил		Калинкина				
Зам.нач.отд.		Майорова				
Н. контр.		Гридчина				

141N4-11UMA-4017-TD.M

Амурская ТЭС. Обеспечение нужд Амурского ГПЗ. Строительство основного технологического комплекса объектов Амурской ТЭС (2ПСУх80 МВт). Этап 1. "Амурская ТЭС (ПСУ-2х80 МВт)".

Паротурбинное отделение. Паротурбинная установка №1. PI-диаграмма трубопроводов циркуляционной охлаждающей воды конденсатора турбины №1

PI-диаграмма трубопроводов циркуляционной охлаждающей воды конденсатора турбины №1. Система PAB

Стадия	Лист	Листов
Р	2	

АКЦИОНЕРНОЕ ОБЩЕСТВО ИНСТИТУТ ТЕПЛОЭЛЕКТРОПРОЕКТ Г. МОСКВА

Согласовано

ОАСУ Соболева

Взам. инв. №

Подпись и дата

Инв. № подл.

Формат А2