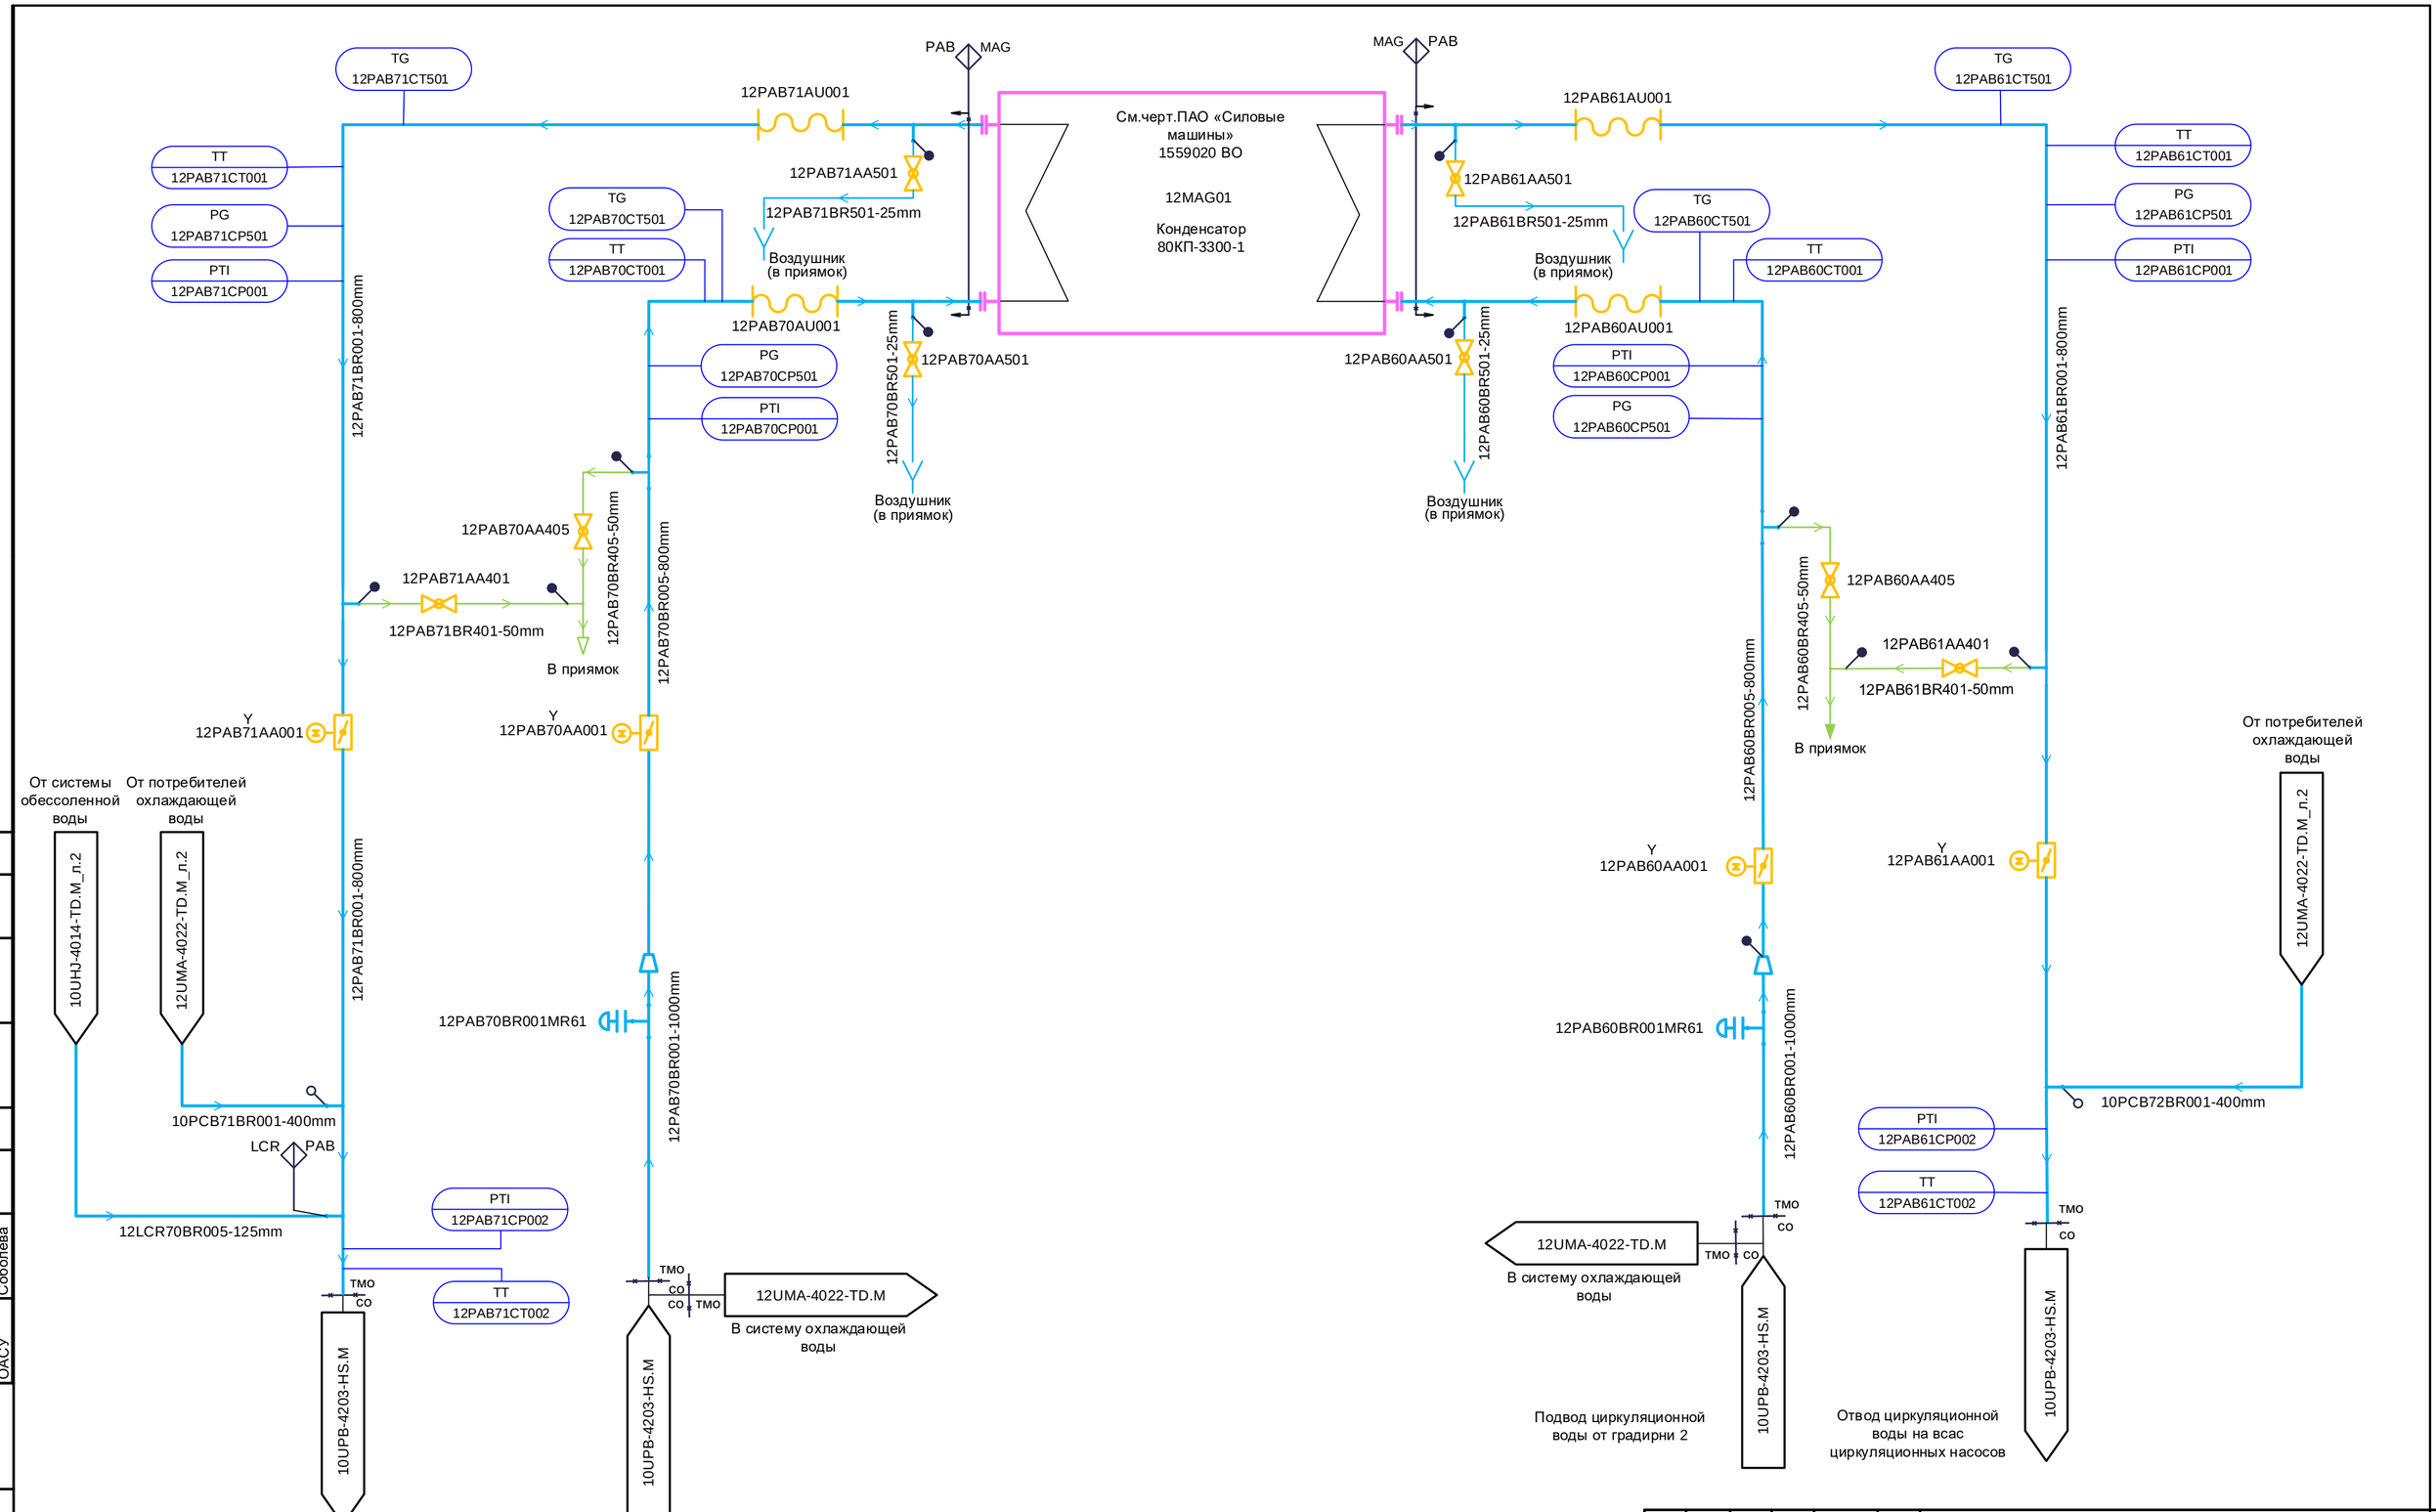

Изм.	Кол.уч	Лист	№ док.	Подп.	Дата
1	-	Зам	1102-19		

Разработал	Полянская	
Проверил	Калинкина	
Зам.нач.отд.	Майорова	
Н. контр.	Гридчина	

141N4 – 12UMA – 4018 – TD.M

Амурская ТЭС. Обеспечение нужд Амурского ГПЗ. Строительство основного технологического комплекса объектов Амурской ТЭС (2ПСУх80 МВт). Этап 1. “Амурская ТЭС (ПСУ-2х80 МВт)”.

Паротурбинное отделение. Паротурбинная установка №2. PI-Диаграмма трубопроводов циркуляционной охлаждающей воды конденсатора турбины №2

Стадия	Лист	Листов
Р	2	

PI-диаграмма трубопроводов циркуляционной охлаждающей воды конденсатора турбины №2. Система PAB

АКЦИОНЕРНОЕ ОБЩЕСТВО ИНСТИТУТ ТЕПЛОЭЛЕКТРОПРОЕКТ Г. МОСКВА

Согласовано: ОАСУ Соболева

Взам. инв. №

Подпись и дата

Инв. № подл.

Формат А2