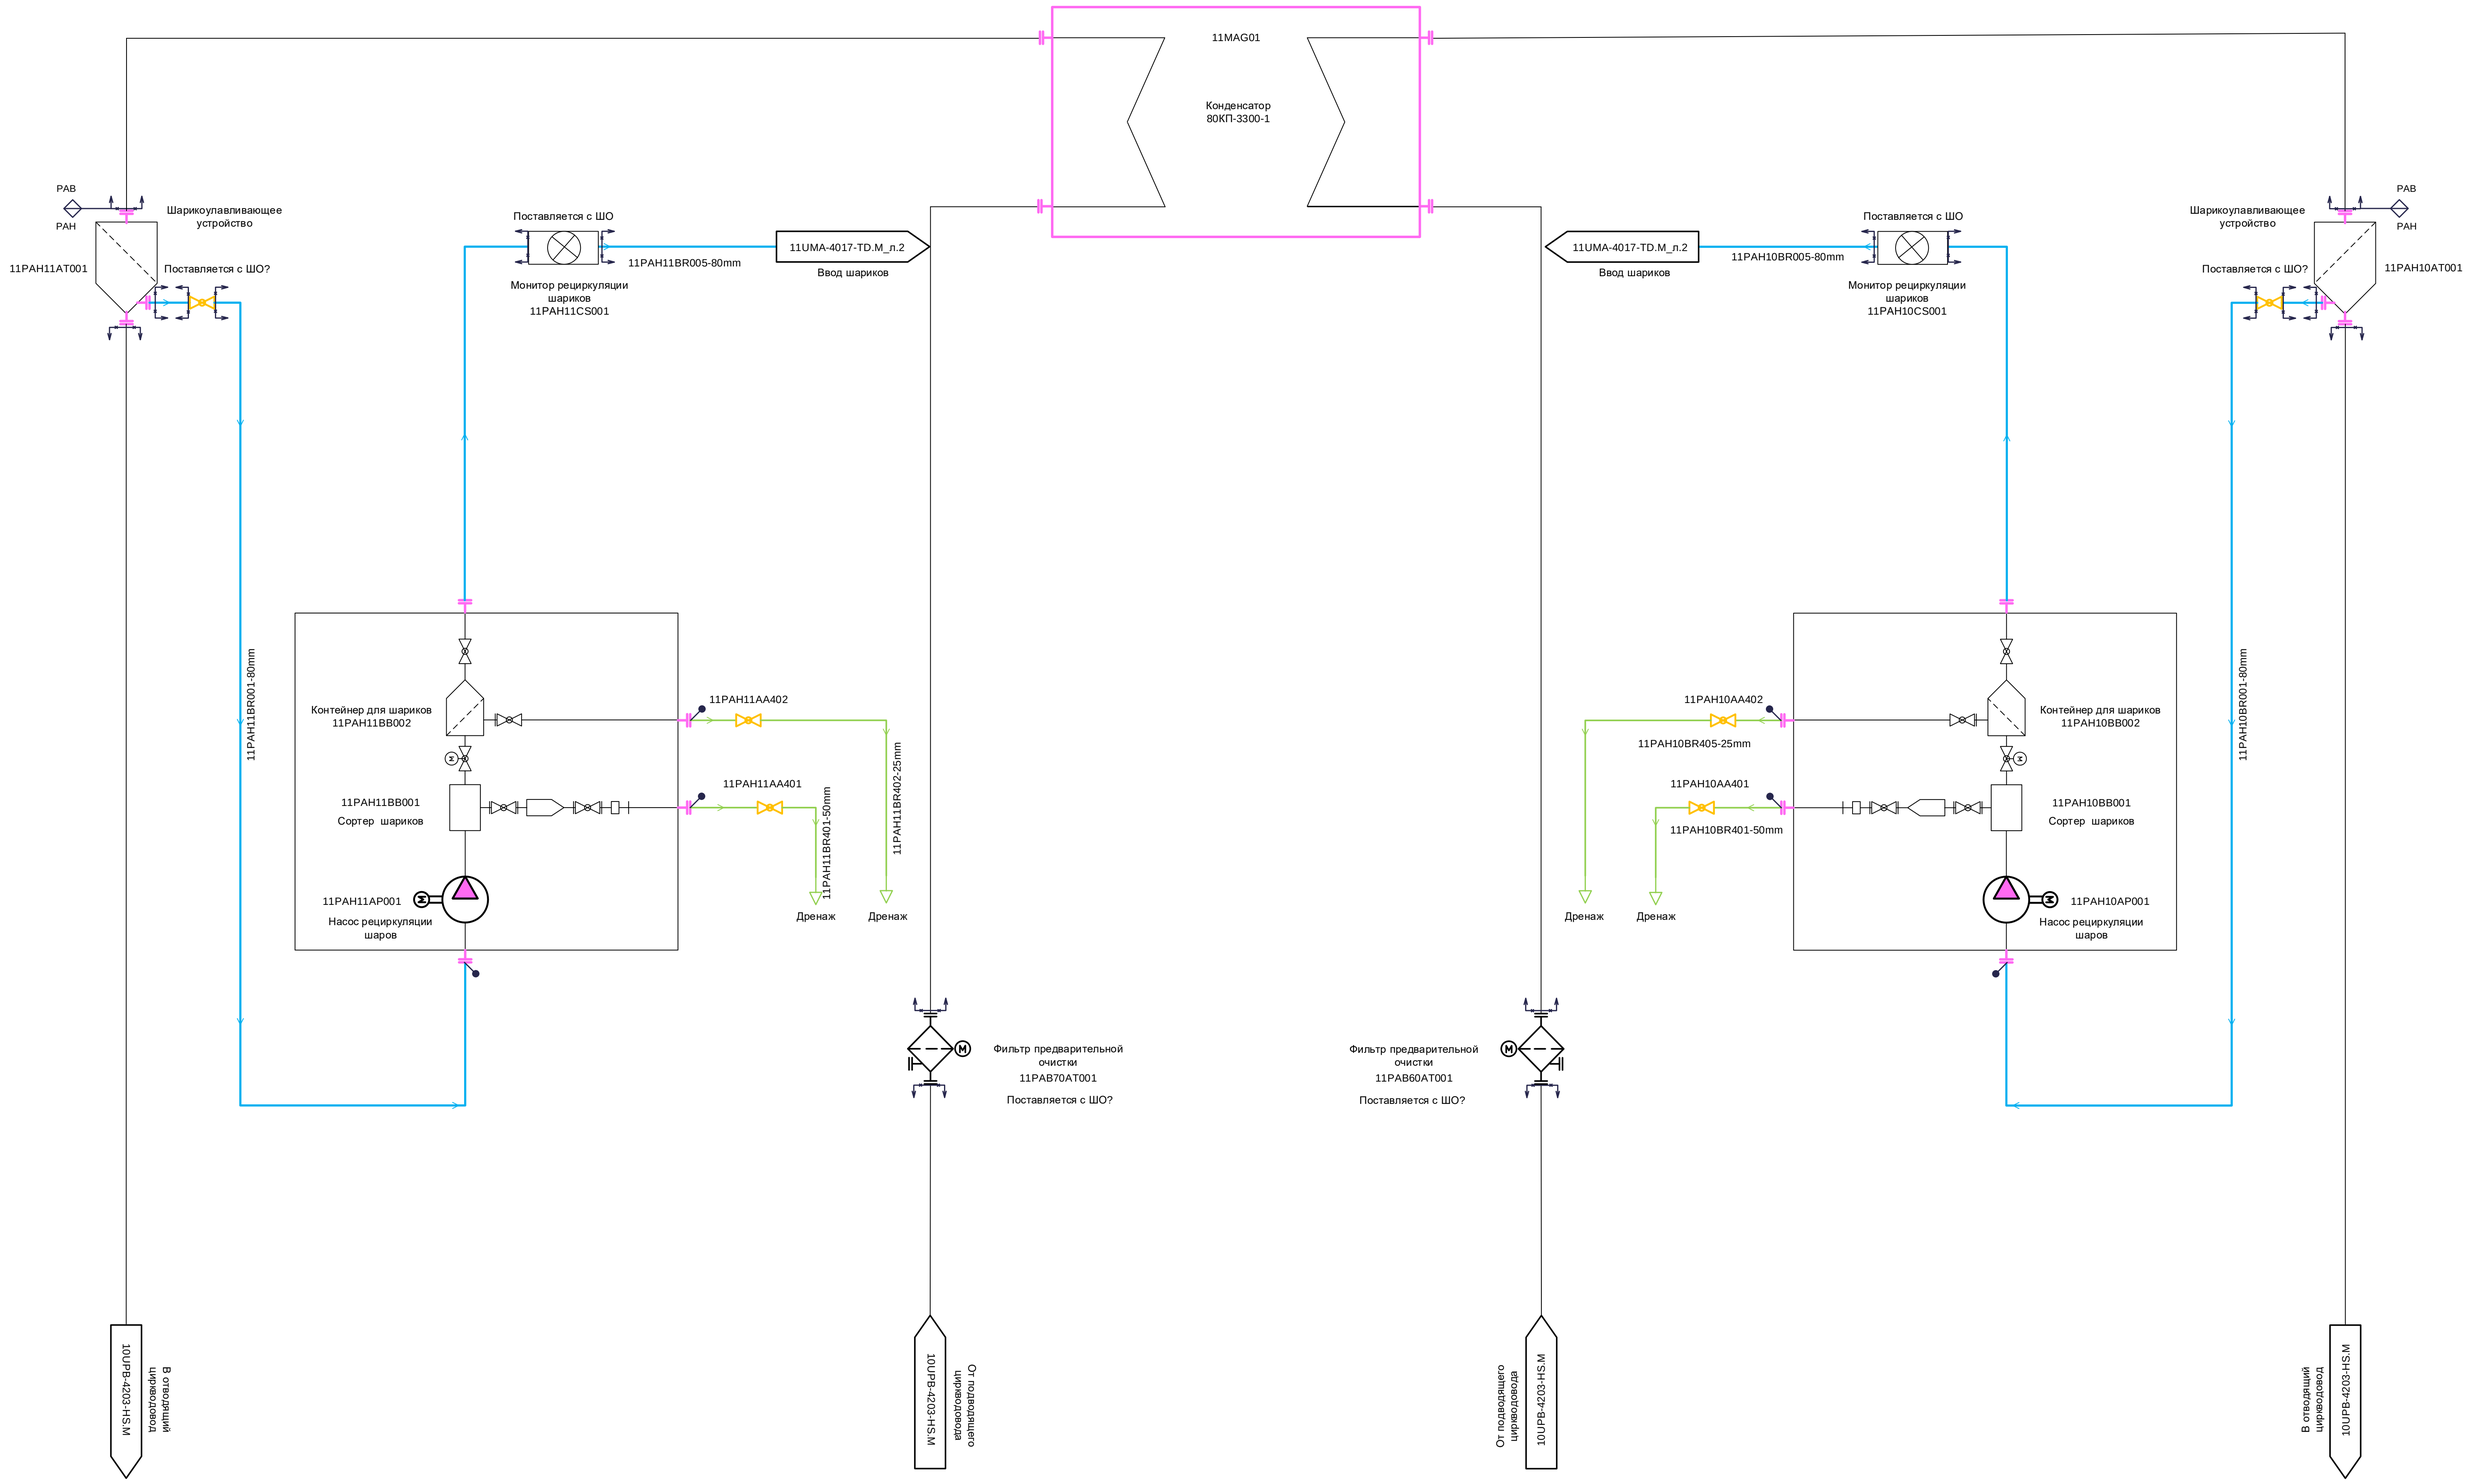


Согласовано

Взам. инв. №

Подпись и дата

Инв. № подл.

| Изм. | Кол.уч | Лист | № док. | Подп. | Дата |
|---|---|---|---|---|---|
| Разработал | | Полянская | | | |
| Проверил | | Калинкина | | | |
| Зам.нач.отд. | | Майорова | | | |
| Н. контр. | | Грядчина | | | |

141N4-11UMA-4019-TD.M

Амурская ТЭС. Обеспечение нужд Амурского ГПЗ.
Строительство основного технологического комплекса объектов Амурской ТЭС (2ПСУ х80 МВт). Этап 1. "Амурская ТЭС (2х80 МВт)".

Паротурбинное отделение. Паротурбинная установка №1. PI-Диаграмма трубопроводов шариковой очистки конденсаторов турбины№1

| Стадия | Лист | Листов |
|---|---|---|
| Р | 2 | |

PI-диаграмма трубопроводов шариковой очистки конденсатора турбины №1. Система РАН

АКЦИОНЕРНОЕ ОБЩЕСТВО ИНСТИТУТ ТЕПЛОЭЛЕКТРОПРОЕКТ г. МОСКВА

Формат А1