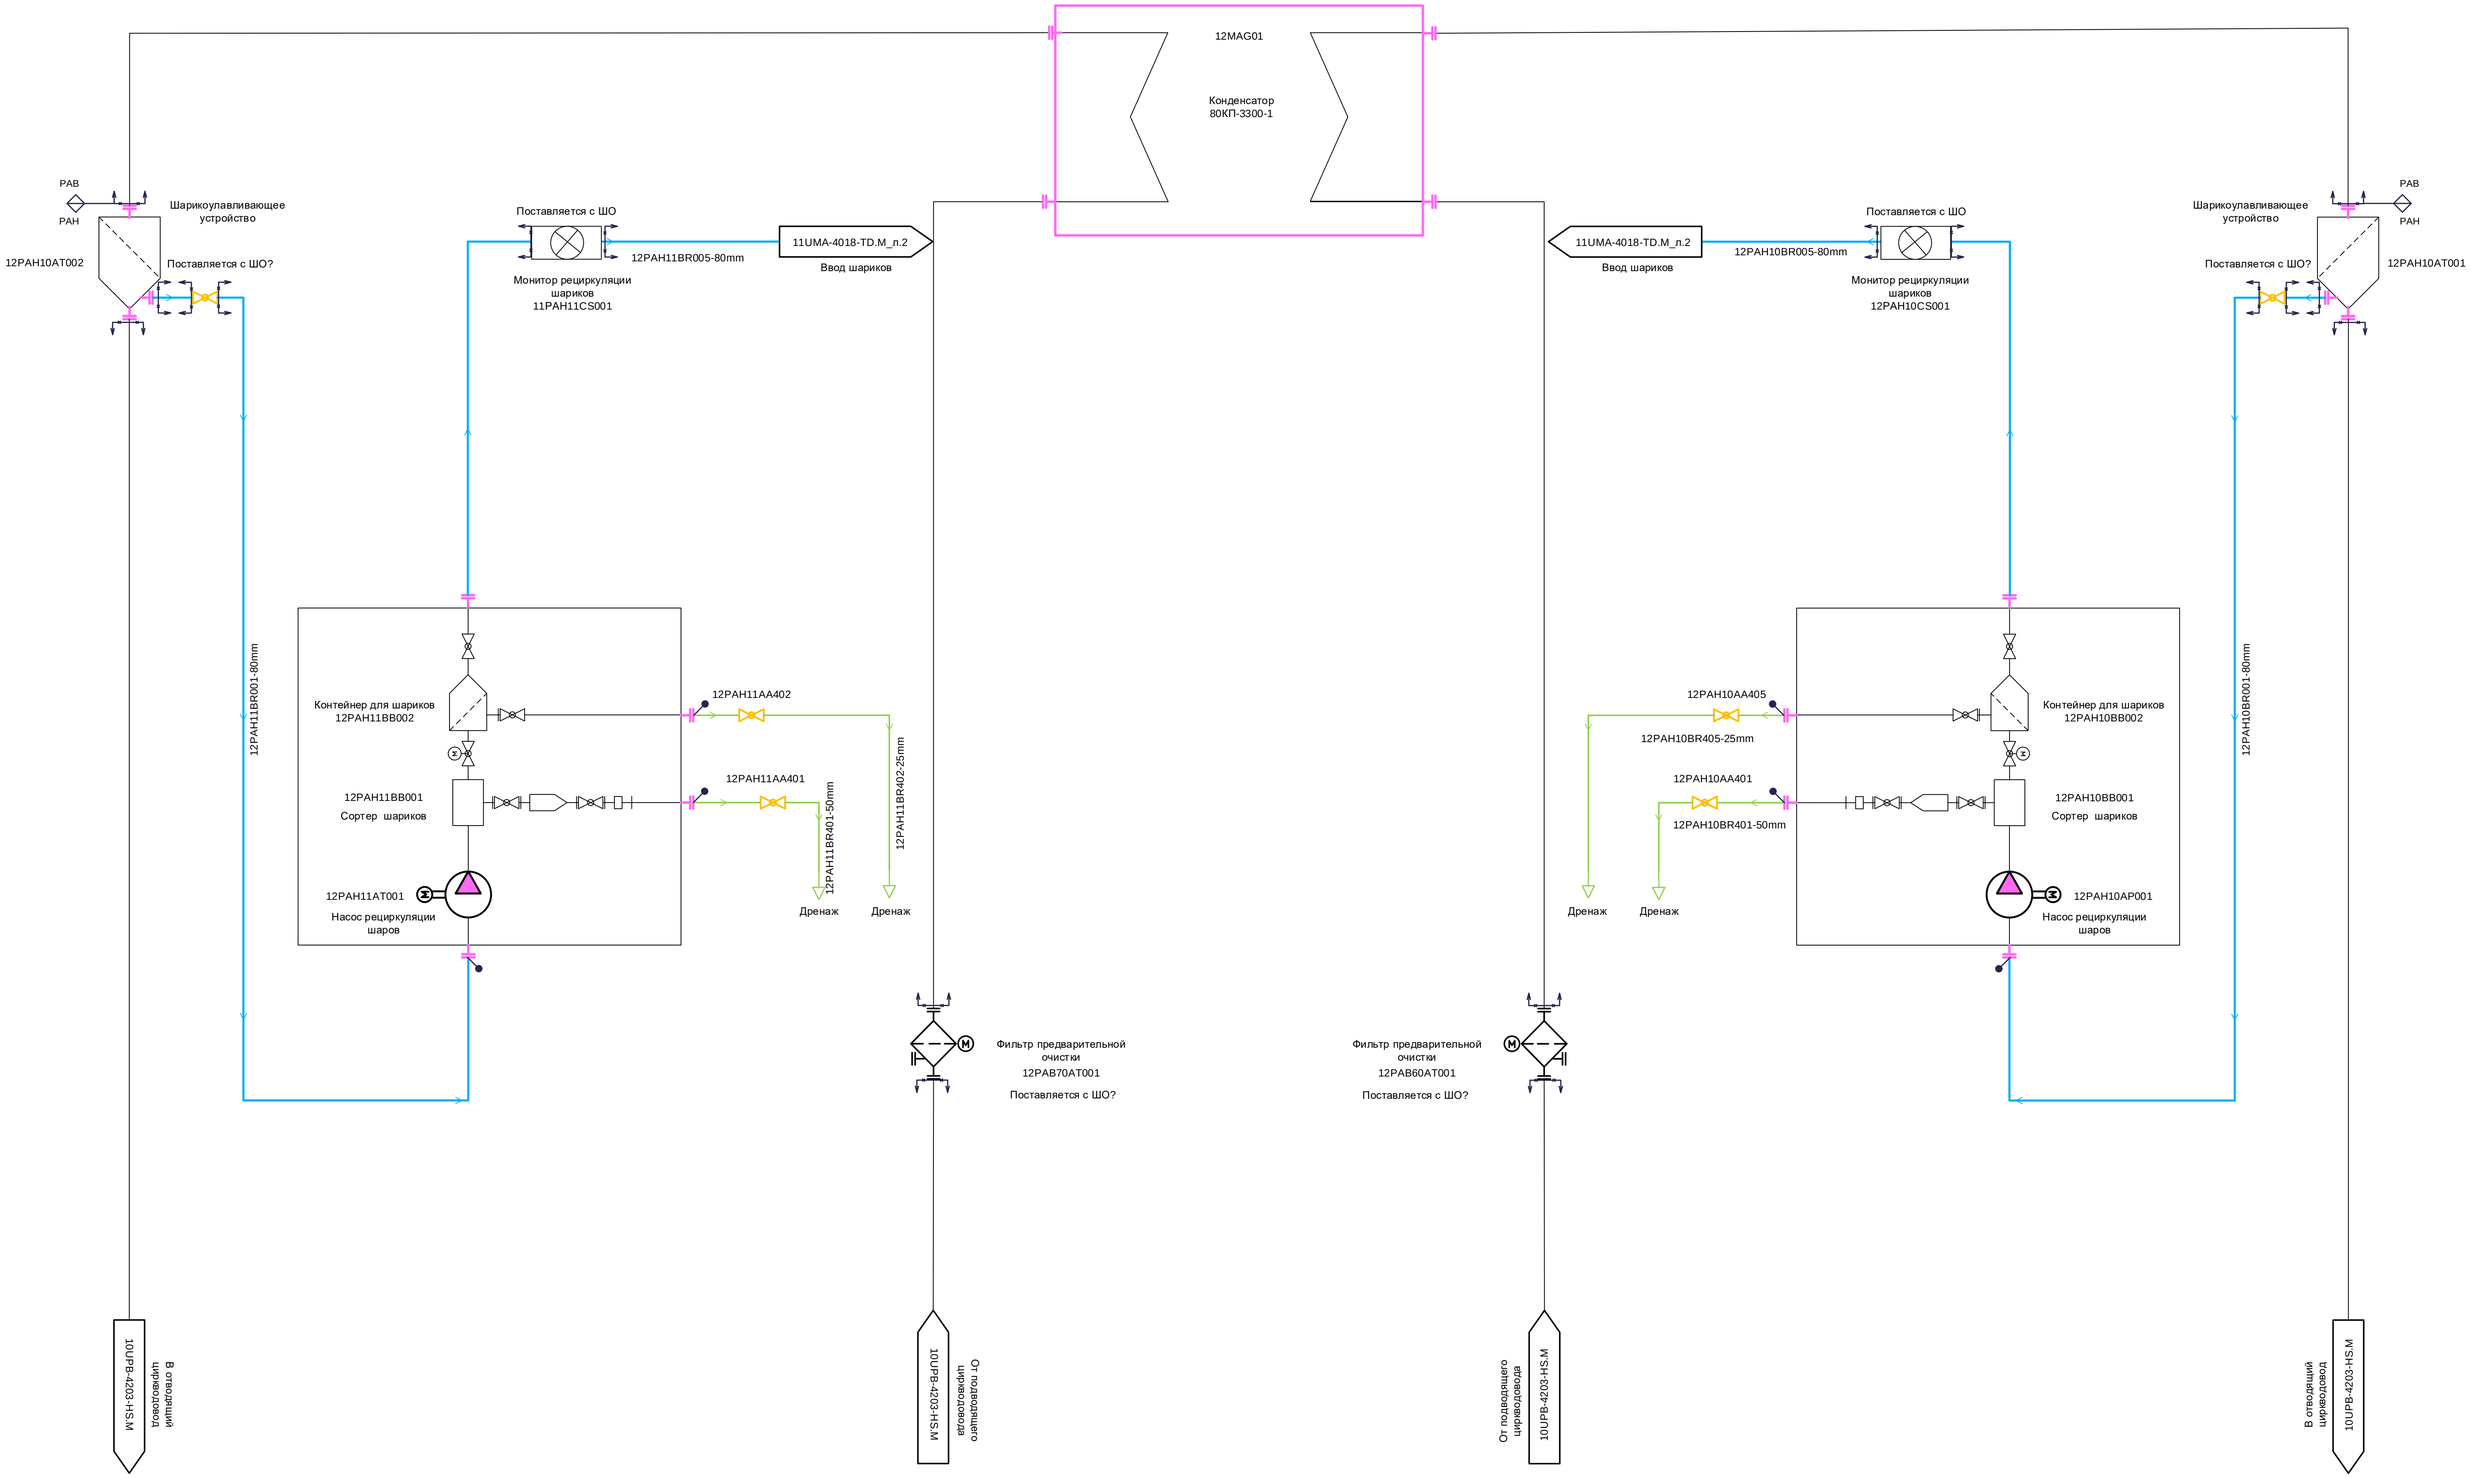

Изм.	Кол.уч.	Лист	№ док.	Подп.	Дата	141N4-12UMA-4020-TD.M
Разработал		Полянская				Амурская ТЭС. Обеспечение нужд Амурского ГПЗ. Строительство основного технологического комплекса объектов Амурской ТЭС (2ПСУ х80 МВт). Этап 1. "Амурская ТЭС (2х80 МВт)".
Проверил		Калинкина				Паротурбинное отделение. Паротурбинная установка №2. PI-Диаграмма трубопроводов шариковой очистки конденсаторов турбины№2
Зам.нач.отд.		Майорова				Стадия: Р; Лист: 2; Листов:
Н. контр.		Гридчина				PI-диаграмма трубопроводов шариковой очистки конденсатора турбины №2. Система РАН

АКЦИОНЕРНОЕ ОБЩЕСТВО ИНСТИТУТ ТЕПЛОЭЛЕКТРОПРОЕКТ г. МОСКВА

Согласовано

Взам. инв. №

Подпись и дата

Инв. № подл.

Формат А1