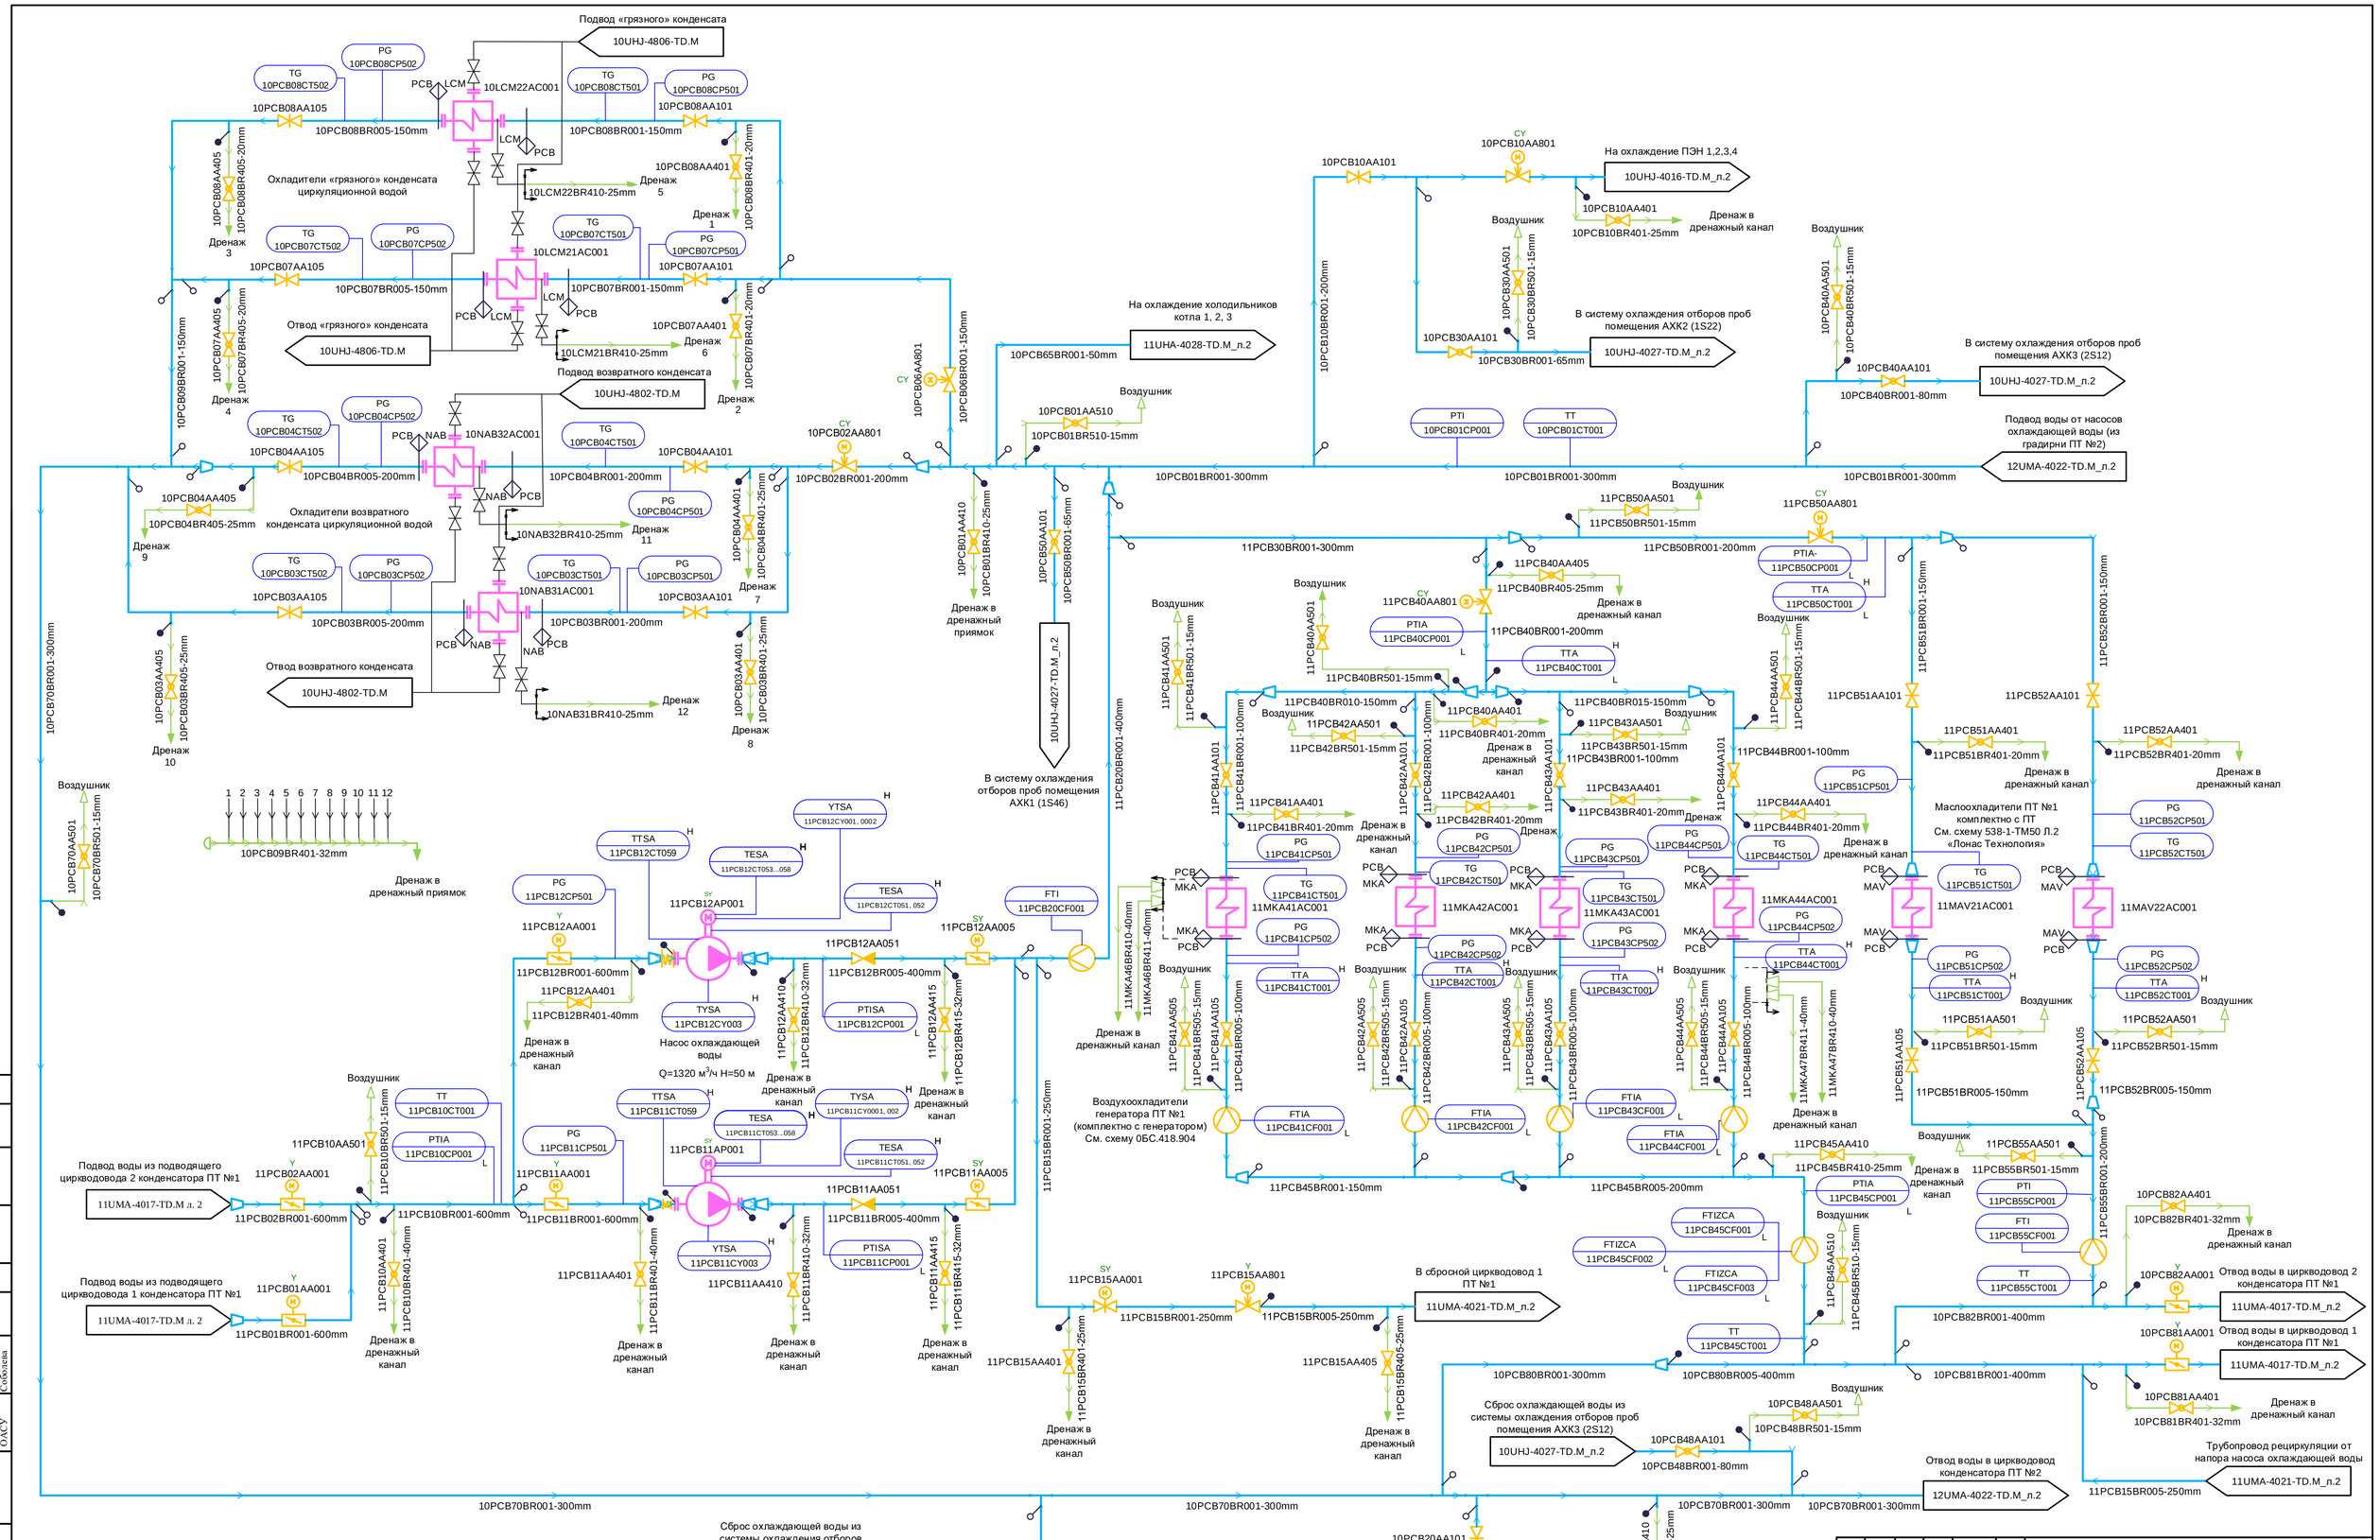

1						141N4-11UMA-4021-TD.M
Изм.	Кол.уч	Лист	№ док.	Подп.	Дата	Амурская ТЭС. Обеспечение нужд Амурского ГПЗ. Строительство основного технологического комплекса объектов Амурской ТЭС (2 ПСУх80МВт). Этап 1."Амурская ТЭС (ПСУ-2х80 МВт)"
Разработал	Калинкина					Паротурбинное отделение. Паротурбинная установка №1. PI-диаграмма трубопроводов охлаждающей воды собственных нужд из циркуляционного трубопровода конденсатора турбины №1
Проверил	Майорова					
Н. контр.	Грядчина					PI-диаграмма трубопроводов охлаждающей воды собственных нужд из циркуляционного трубопровода конденсатора турбины №1. Система РСВ

Стадия	Лист	Листов
Р	2	

АКЦИОНЕРНОЕ ОБЩЕСТВО ИНСТИТУТ ТЕПЛОЭЛЕКТРОПРОЕКТ г. Москва

Согласовано: ОАСУ, Соболева

Взам. инв. № | Подпись и дата | Инв. № подл.

Формат А1