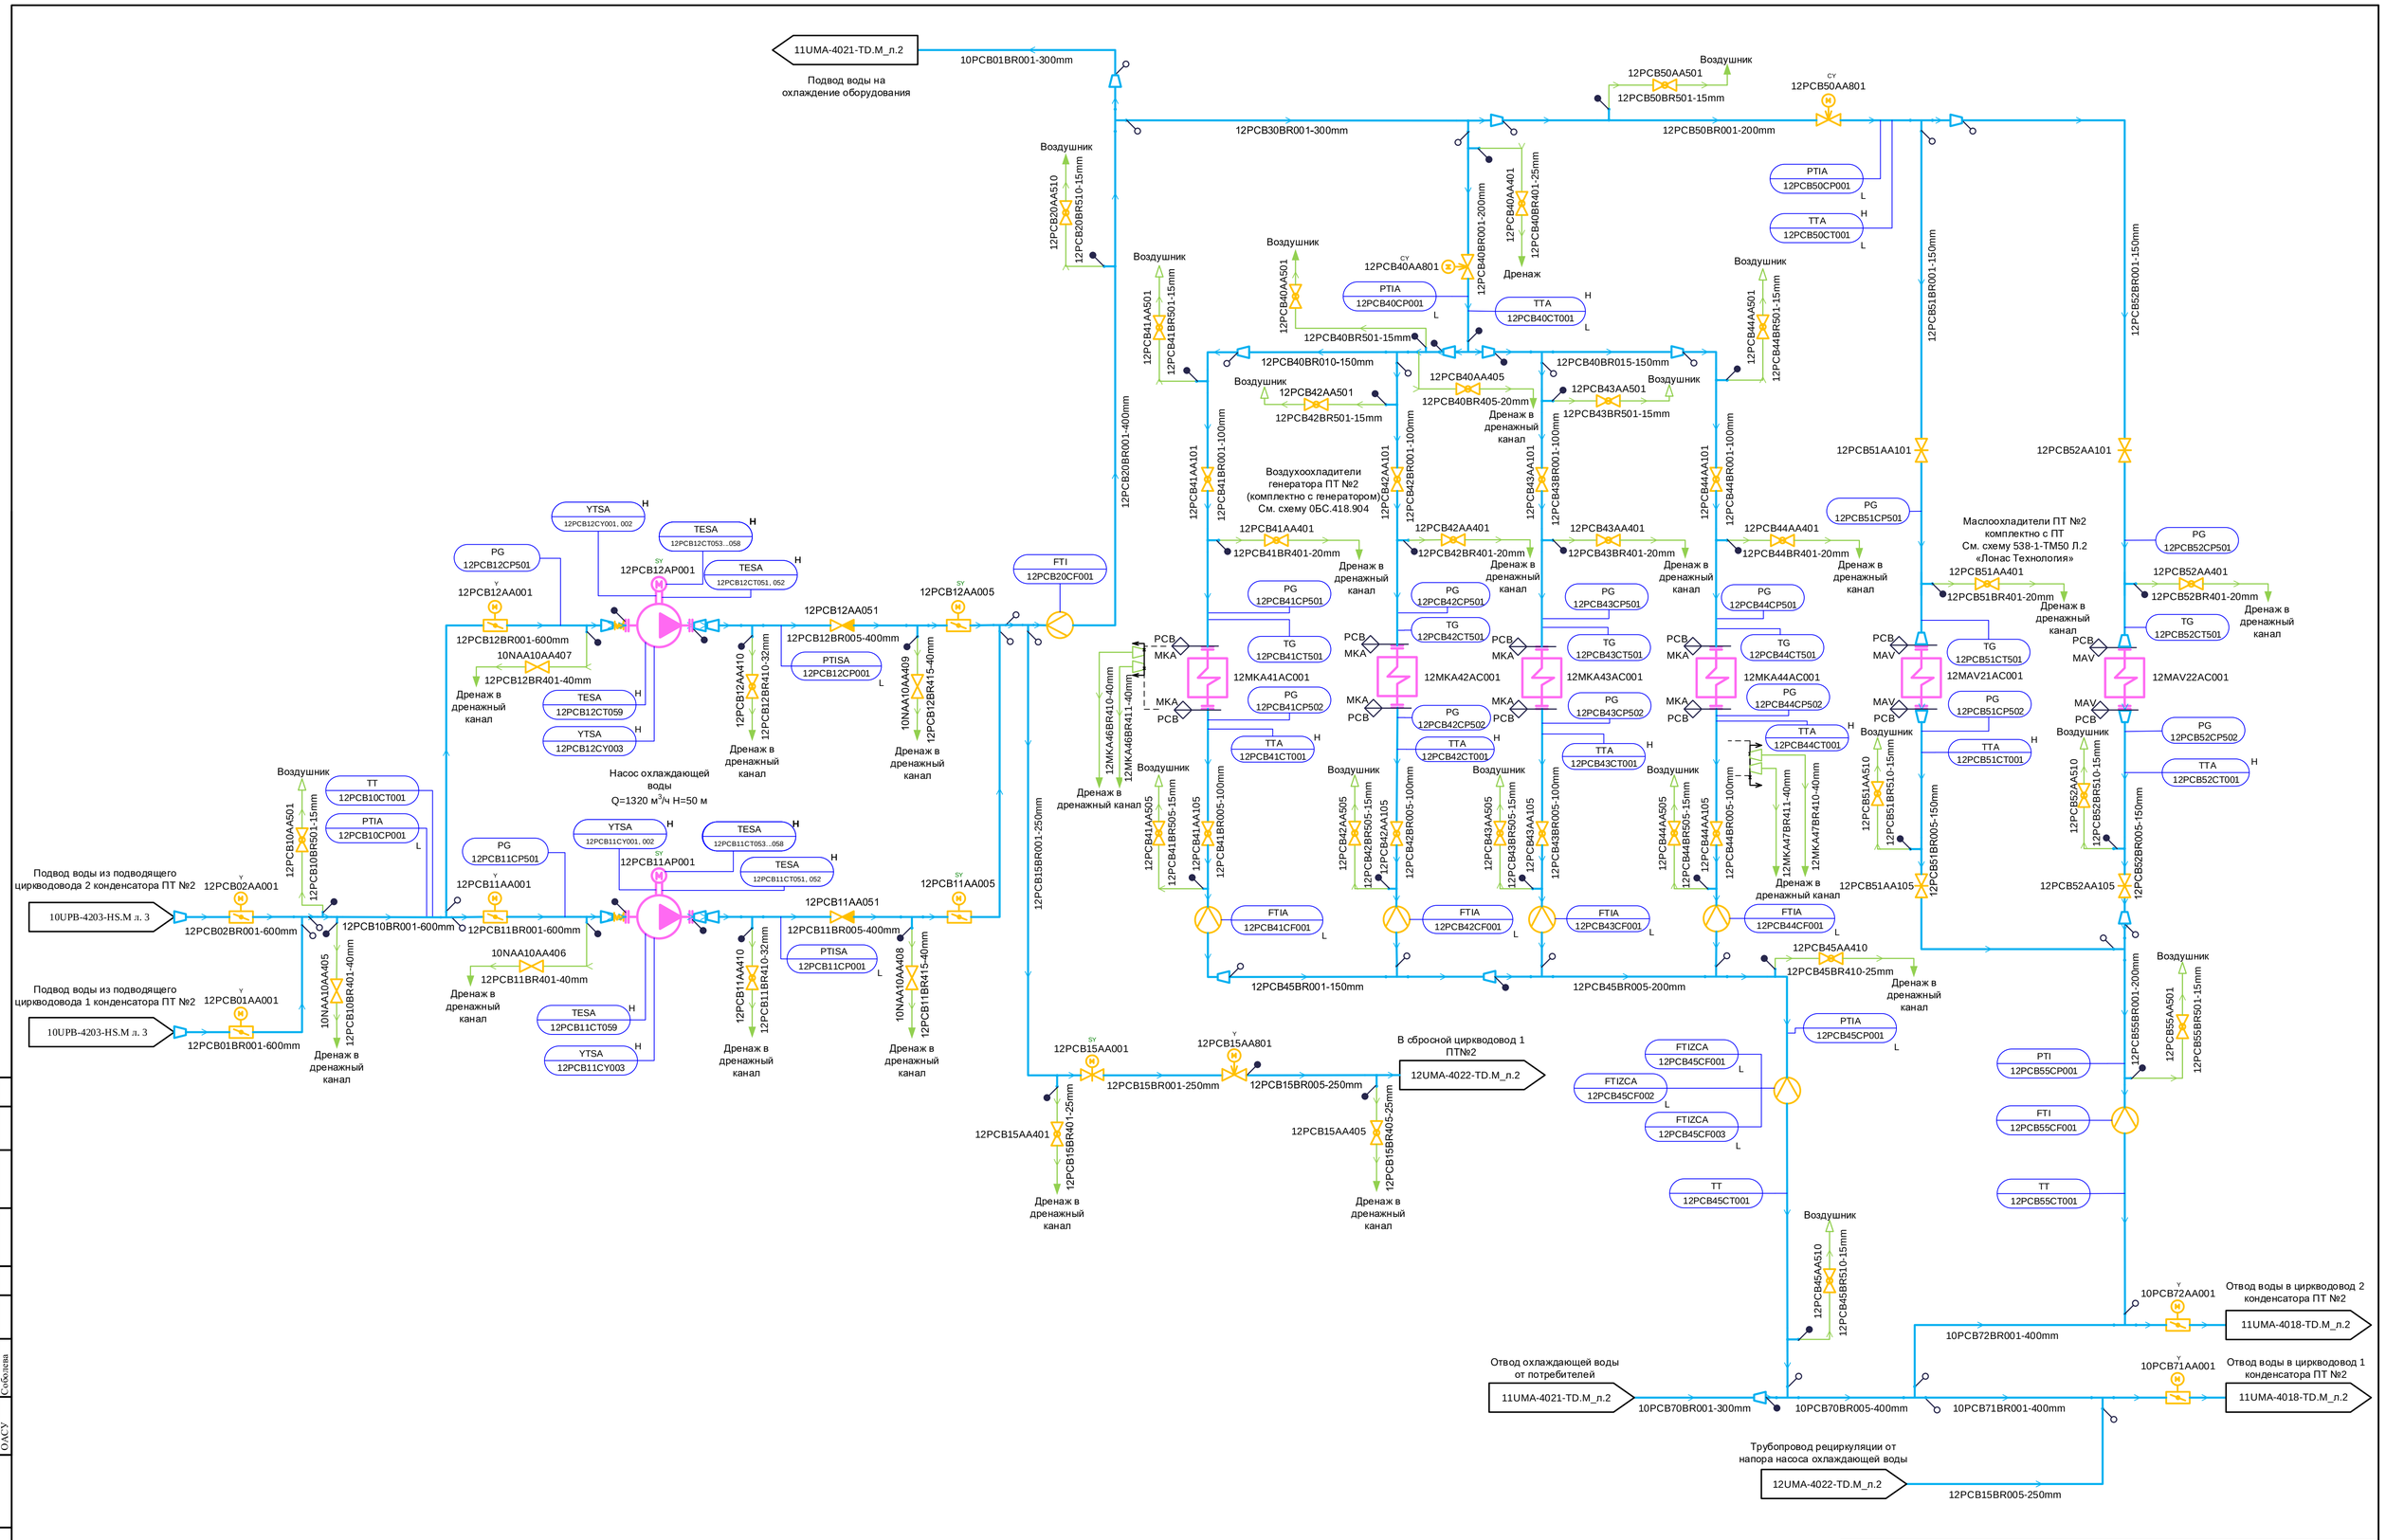

Изм.	Кол.уч	Лист	№ док.	Подп.	Дата	
Разработал	Калинкина					
Проверил	Майорова					
Н. контр.	Грядчина					

141N4-12UMA-4022-TD.M

Амурская ТЭС. Обеспечение нужд Амурского ГПЗ. Строительство основного технологического комплекса объектов Амурской ТЭС (2 ПСУх80МВт). Этап 1."Амурская ТЭС (ПСУ-2х80 МВт)"

Паротурбинное отделение. Паротурбинная установка №2.
PI-диаграмма трубопроводов охлаждающей воды собственных нужд из циркуляционного трубопровода конденсатора турбины №2
PI-диаграмма трубопроводов охлаждающей воды собственных нужд из циркуляционного трубопровода конденсатора турбины №2. Система РСВ

Стадия	Лист	Листов
Р	2	

АКЦИОНЕРНОЕ ОБЩЕСТВО ВНИИПИ ТЕПЛОЭЛЕКТРОПРОЕКТ г. МОСКВА

Согласовано
ОАСУ Соболева
Взам. инв. №
Подпись и дата
Инв. № подл.

Формат А1