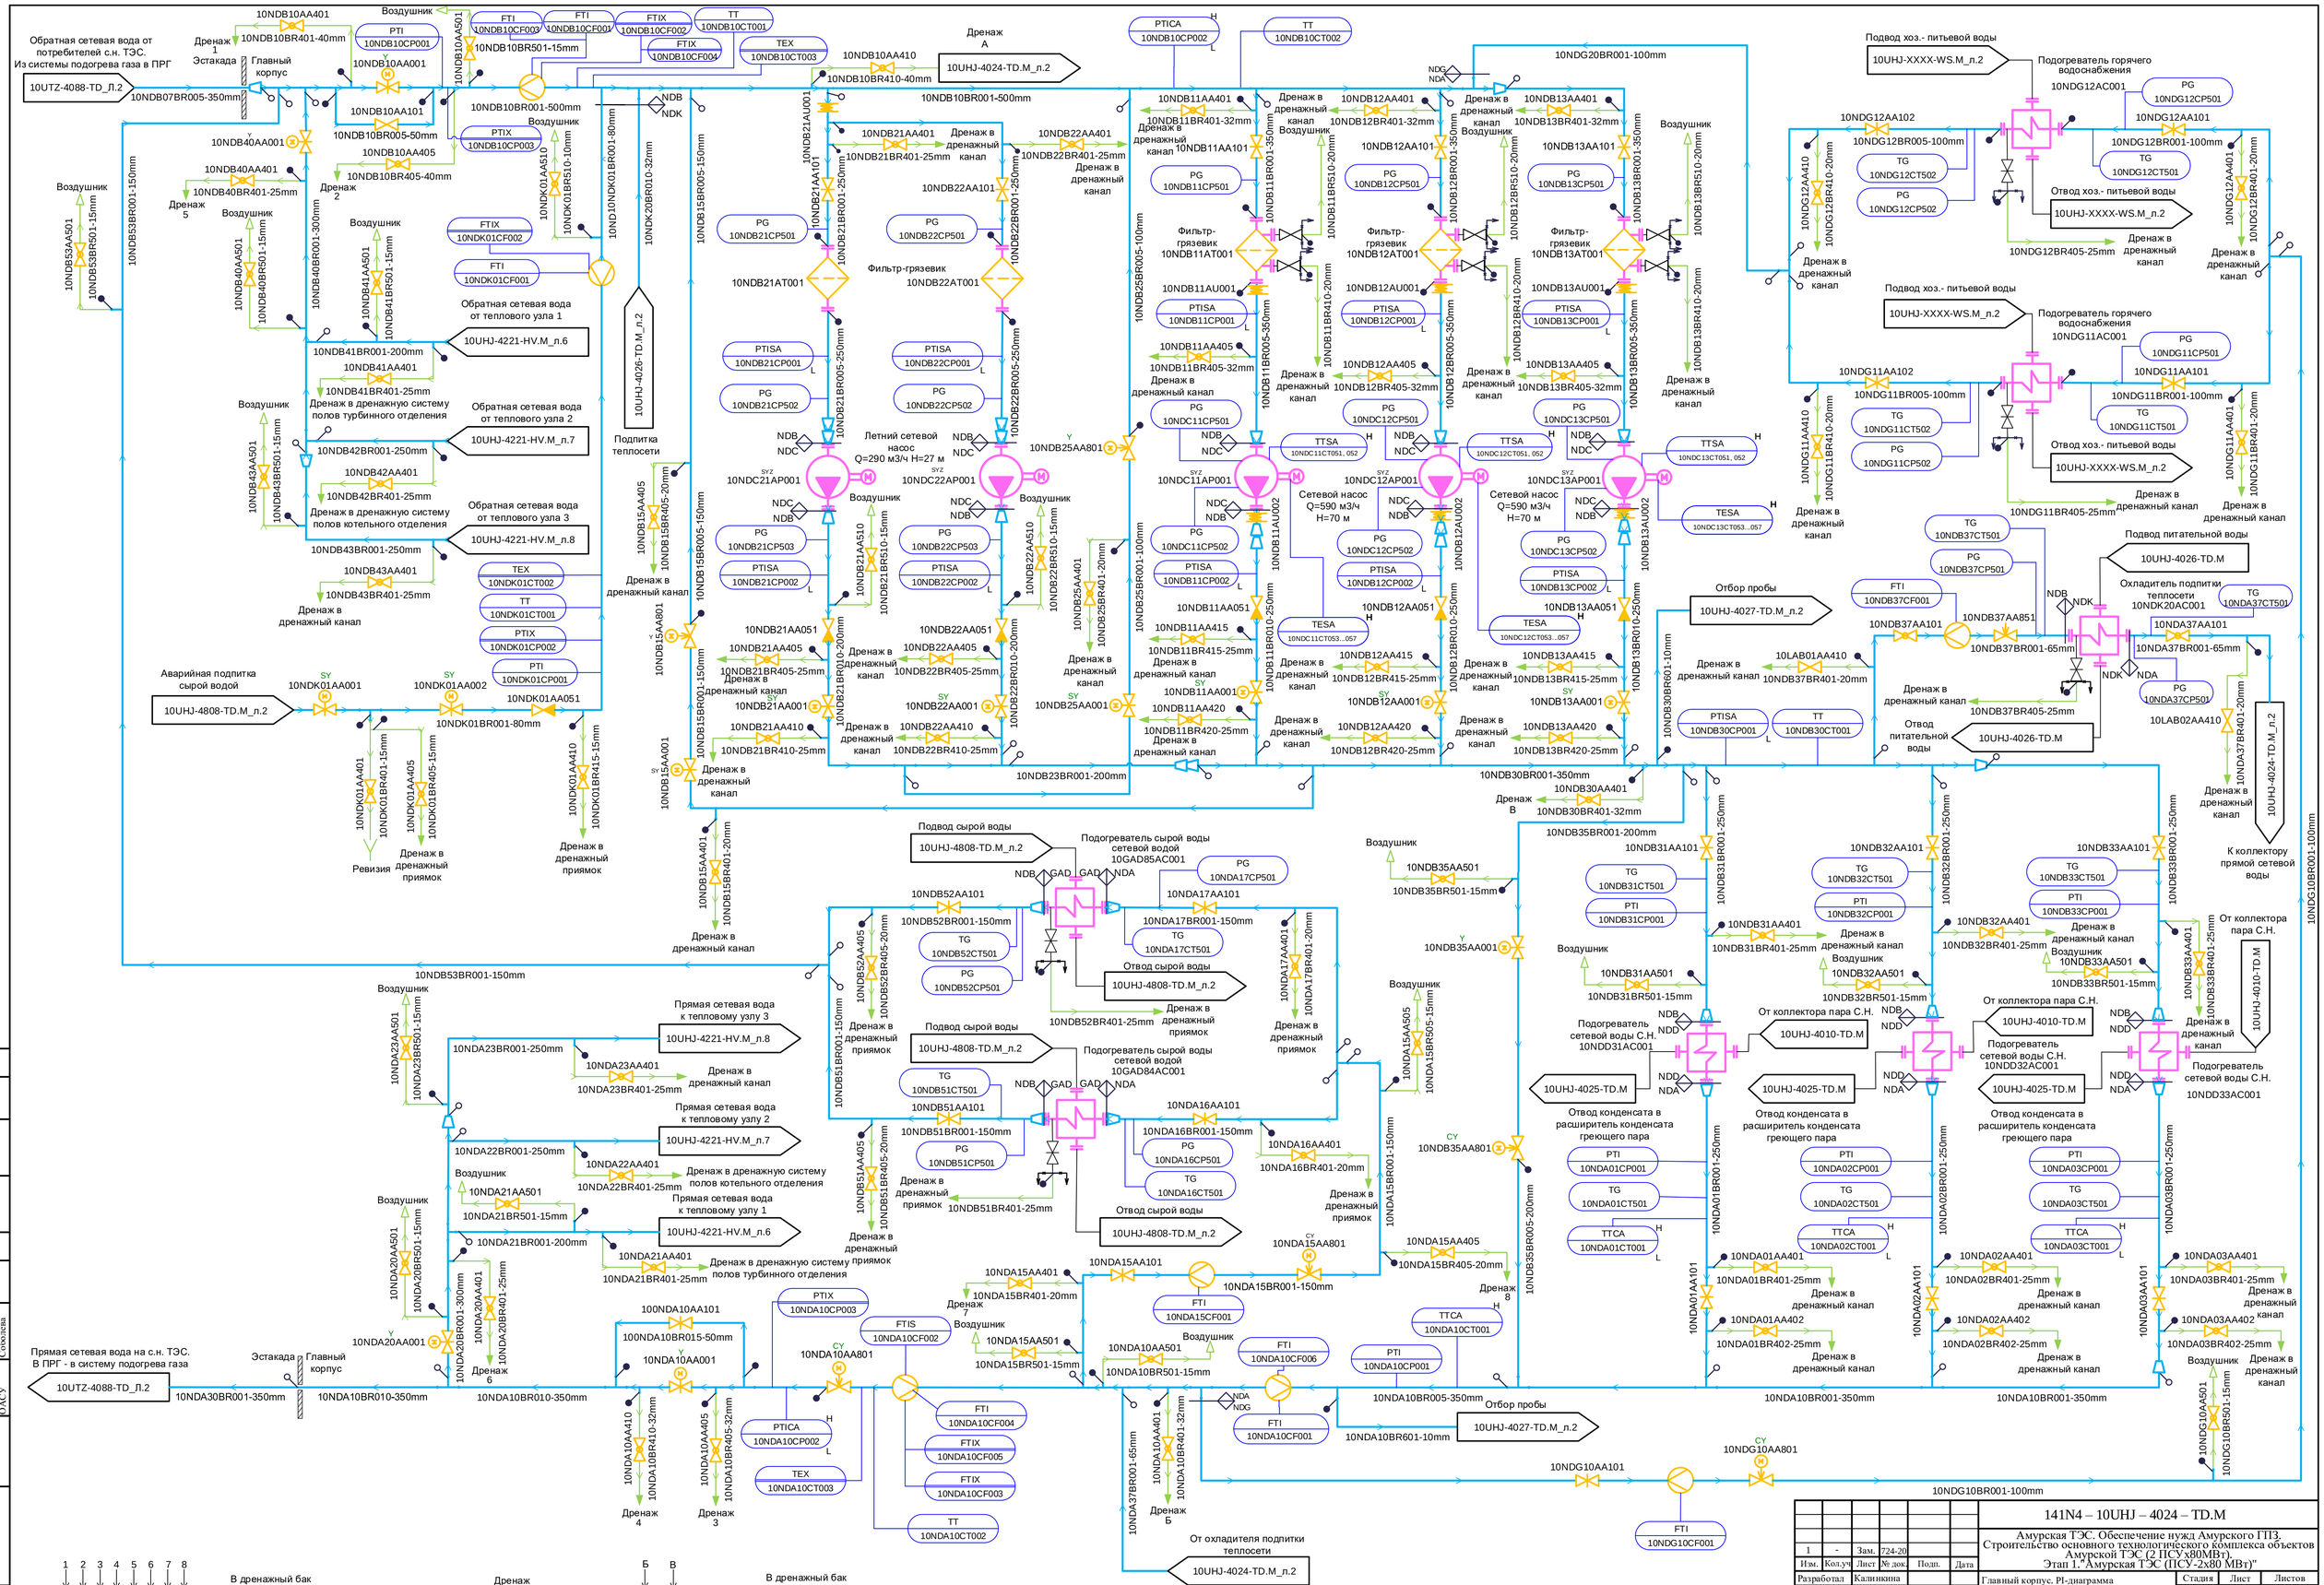

1	-	Зам.	724-20			
Изм.	Кол.уч	Лист	№ док.	Подп.	Дата	
Разработал	Калинкина					
Проверил	Майорова					
Н. контр.	Гридчина					

141N4 – 10UHJ – 4024 – TD.M

Амурская ТЭС. Обеспечение нужд Амурского ГПЗ. Строительство основного технологического комплекса объектов Амурской ТЭС (2 ПСУ х80МВт). Этап 1."Амурская ТЭС (ПСУ-2х80 МВт)"

Главный корпус. PI-диаграмма трубопроводов сетевой воды собственных нужд

PI-диаграмма трубопроводов сетевой воды собственных нужд. Система NDA, NDB, NDC, NDG

Стадия	Лист	Листов
Р	2	

АКЦИОНЕРНОЕ ОБЩЕСТВО ИНСТИТУТ ТЕПЛОЭЛЕКТРОПРОЕКТ г. МОСКВА

Согласовано

ОАСУ Соболева

Взам. инв. №

Подпись и дата

Инв. № подл.

Формат А1