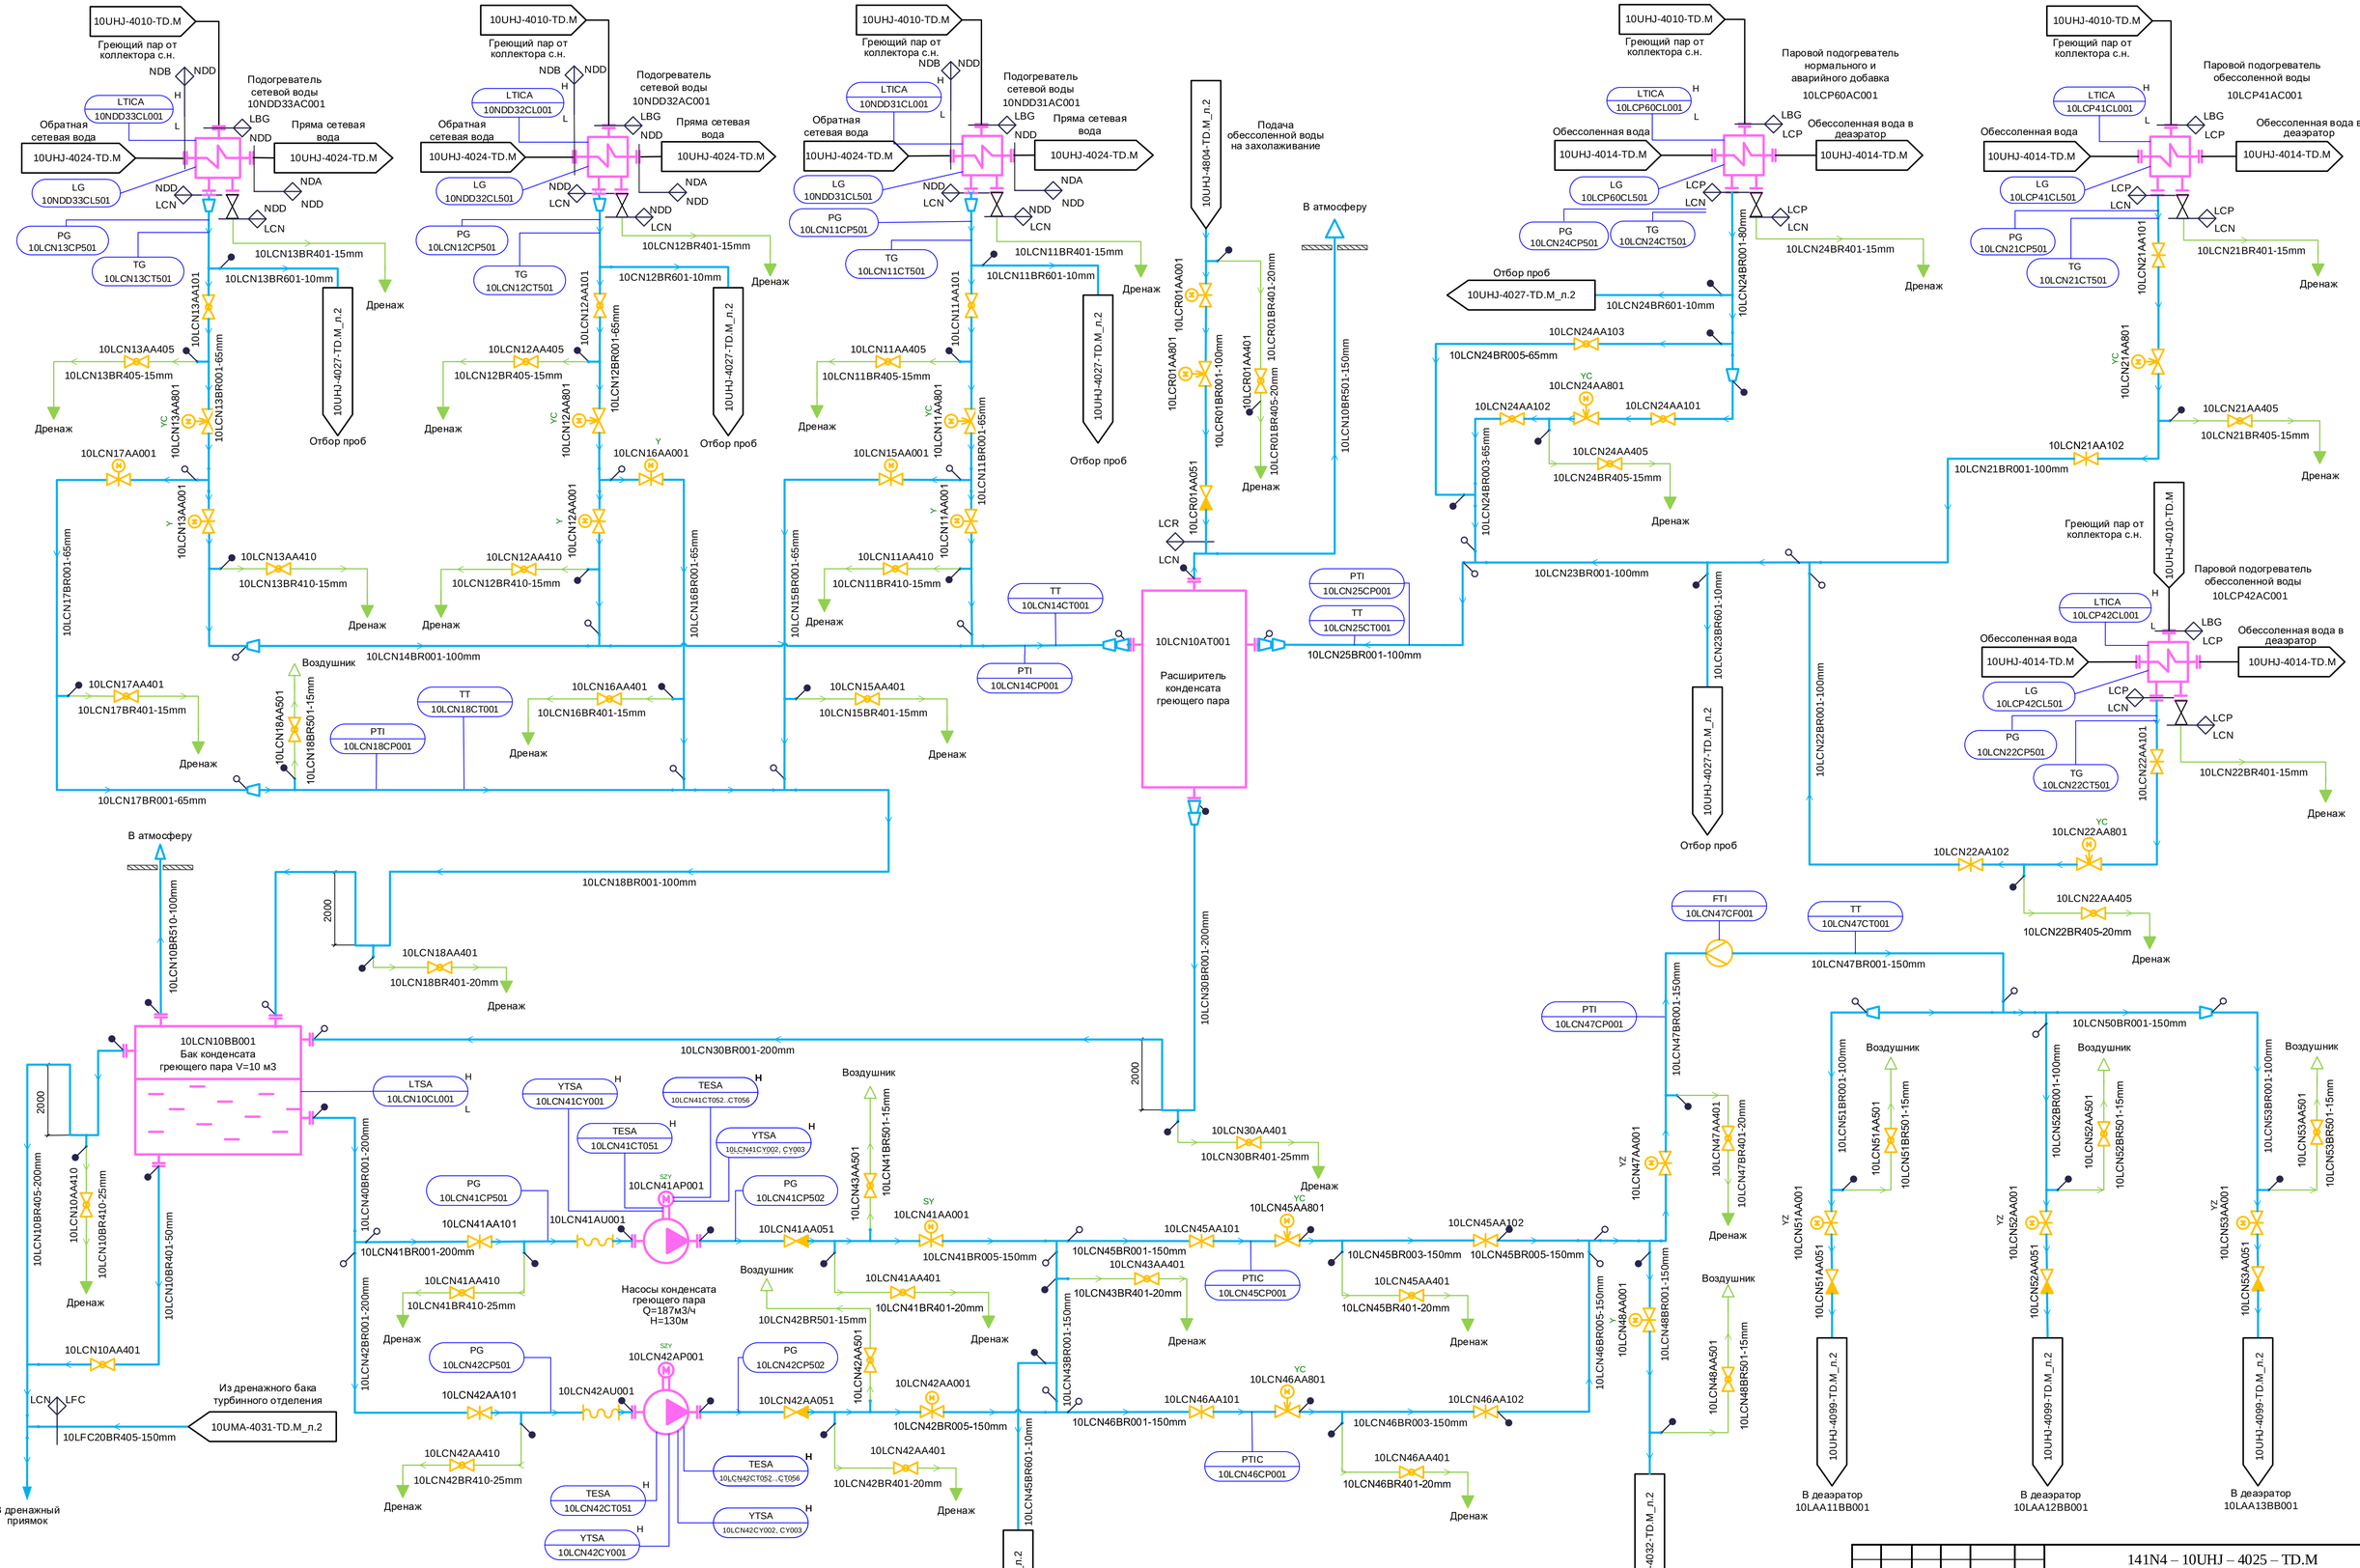


| | | | | | | |
|---|---|---|---|---|---|---|
| 1 | - | Зам. | 1172-20 | | 12.2008 | |
| Изм. | Кол.уч | Лист | № док. | Подп. | Дата | |

141N4 – 10UHJ – 4025 – TD.M

Амурская ТЭС. Обеспечение нужд Амурского ГПЗ. Строительство основного технологического комплекса объектов Амурской ТЭС (2 ПСУ х80МВт). Этап 1."Амурская ТЭС (ПСУ-2х80 МВт)"

| | | |
|---|---|---|
| Разработал | Смирнова | |
| Проверил | Калинкина | |
| Зам.нач.отд. | Майорова | |
| Н. контр. | Гридчина | |

Главный корпус. PI-диаграмма трубопроводов конденсата греющего пара подогревателей сетевой воды, подогревателей обессоленной воды и подогревателя нормального и аварийного добавка

| Стадия | Лист | Листов |
|---|---|---|
| Р | 2 | |

PI-диаграмма трубопроводов конденсата греющего пара подогревателей сетевой воды, подогревателей обессоленной воды и подогревателя нормального и аварийного добавка. Система LCN.

АКЦИОНЕРНОЕ ОБЩЕСТВО ВНИИПИ ТЕПЛОЭЛЕКТРОПРОЕКТ г. МОСКВА

Согласовано: ОАСУ Соболева

Взам. инв. №

Подпись и дата

Инв. № подл.

Формат А1