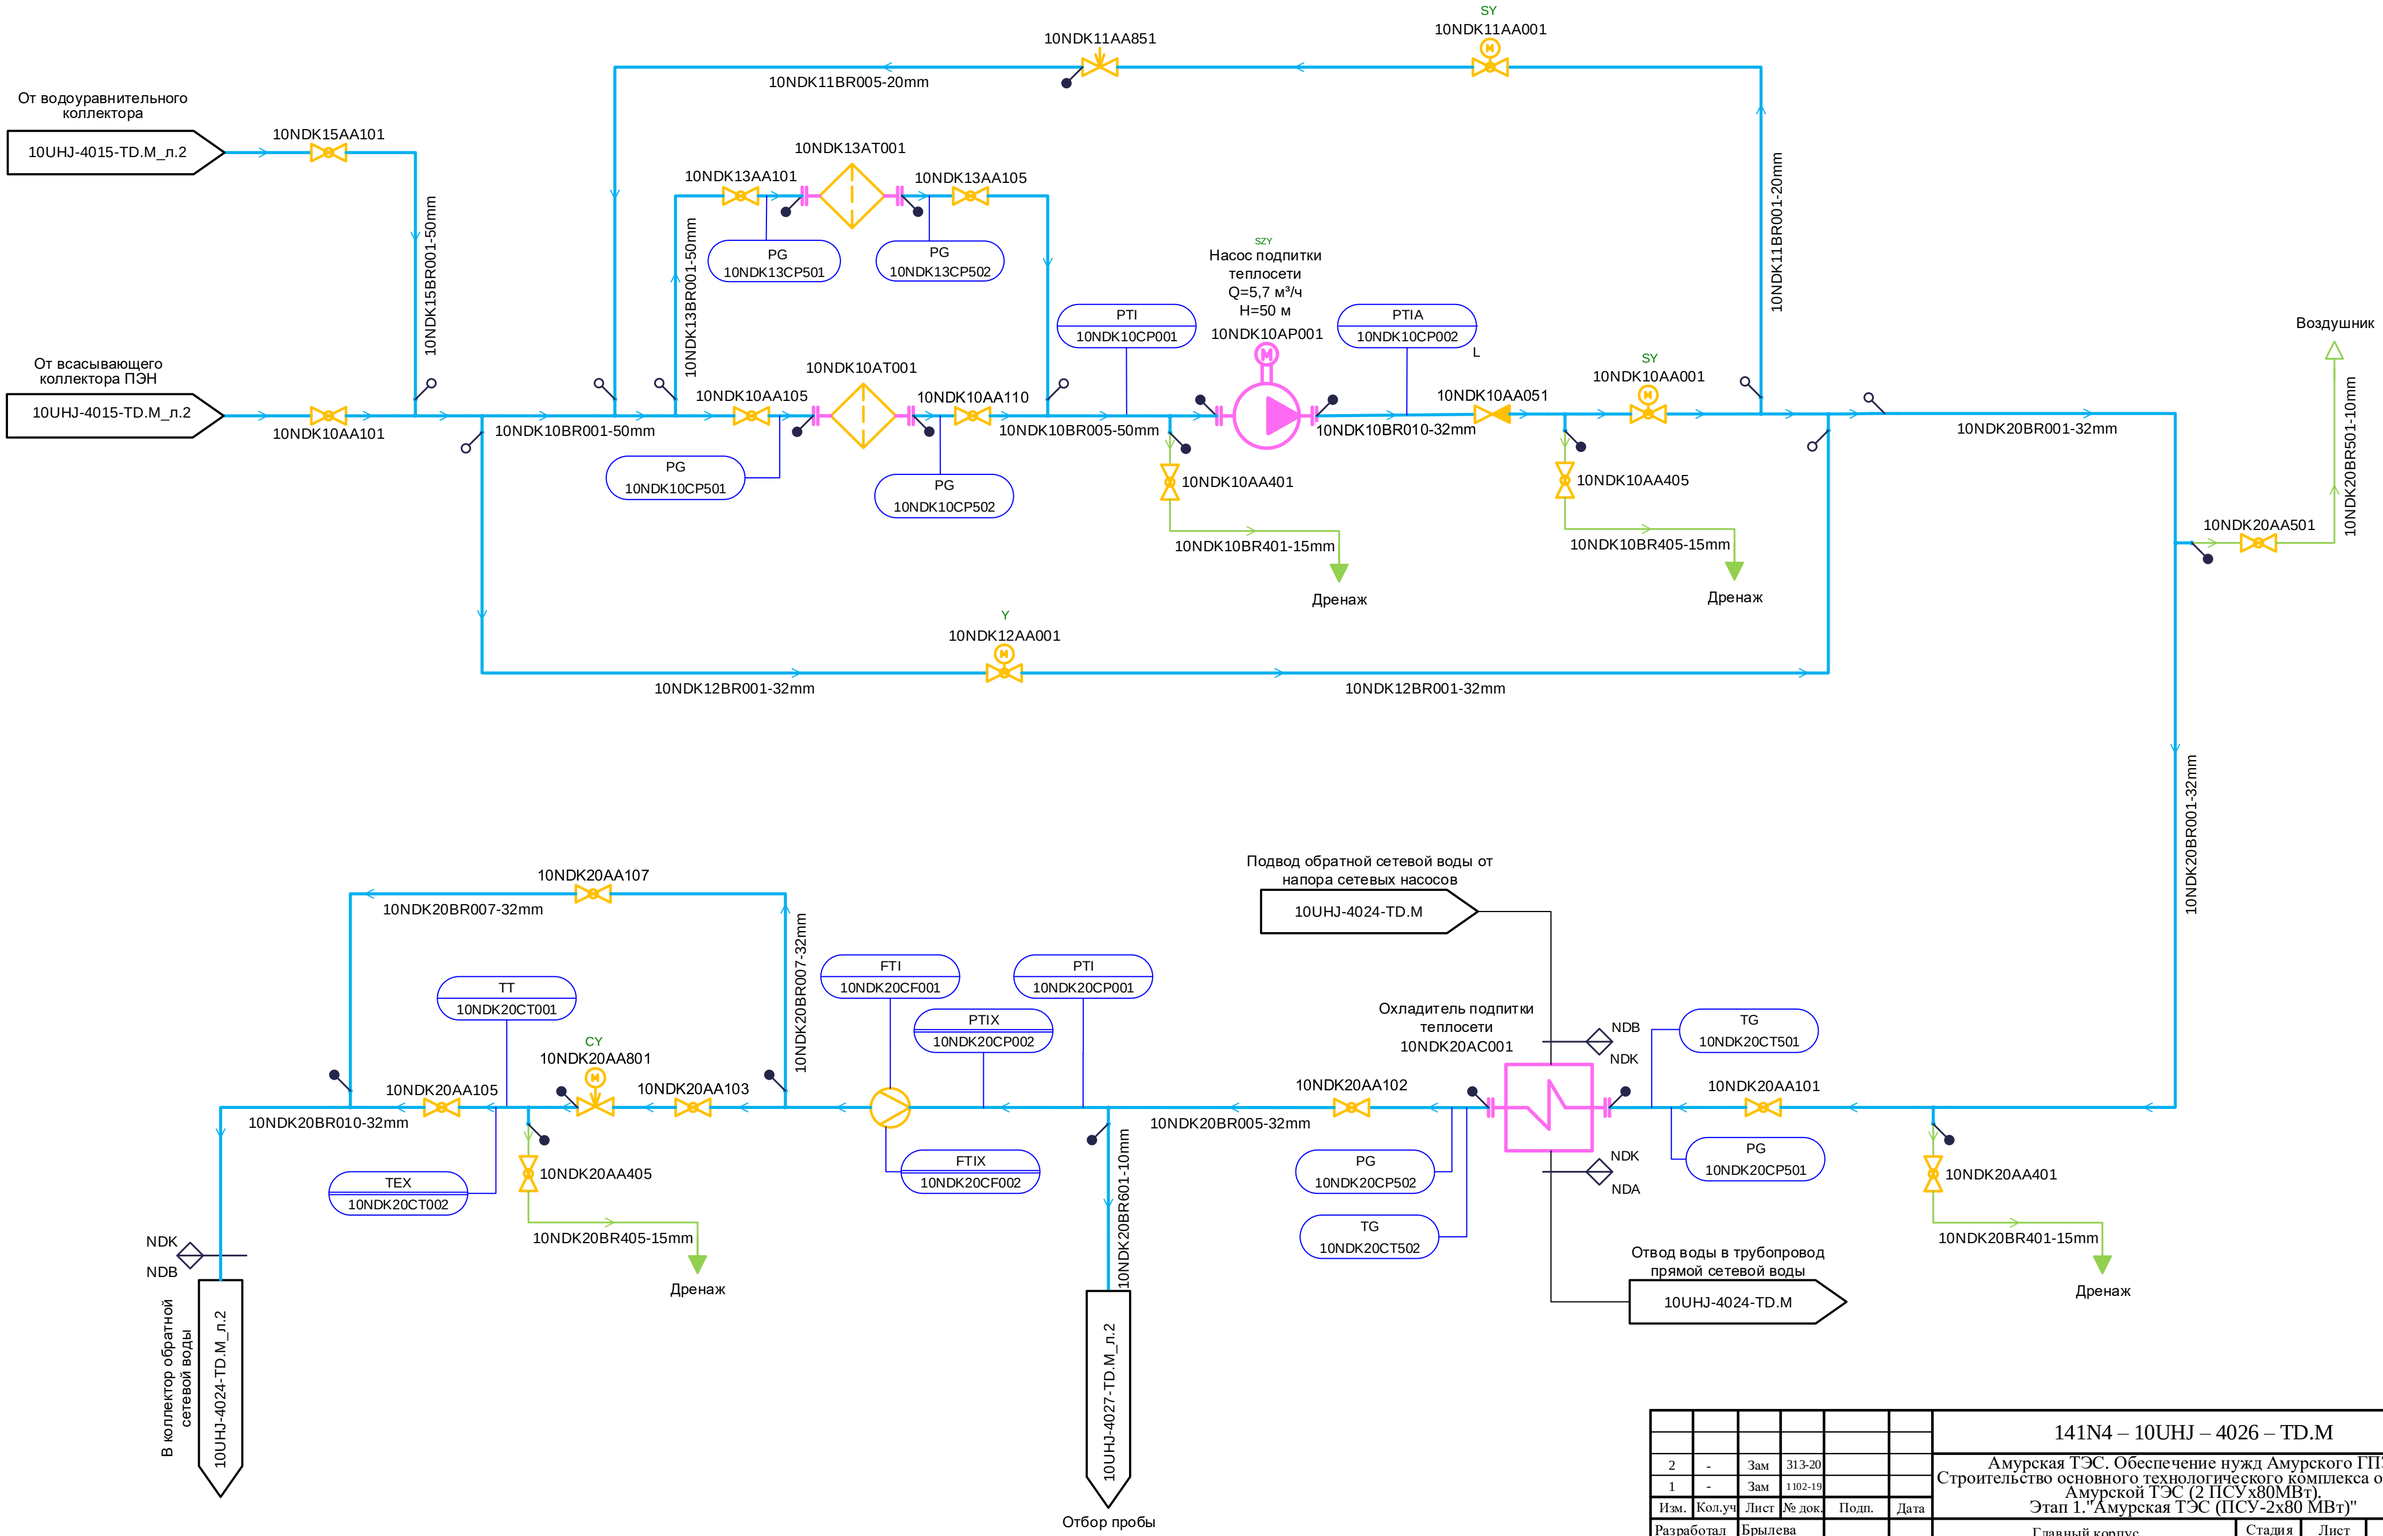

2	-	Зам	313-20			
1	-	Зам	1102-19			
Изм.	Кол.уч	Лист	№ док.	Подп.	Дата	
Разработал		Брылева				
Проверил		Калинкина				
Зам.нач.отд.		Майорова				
Н. контр.		Гридчина				

141N4 – 10UHJ – 4026 – TD.M

Амурская ТЭС. Обеспечение нужд Амурского ГПЗ. Строительство основного технологического комплекса объектов Амурской ТЭС (2 ПСУх80МВт). Этап 1."Амурская ТЭС (ПСУ-2х80 МВт)"

Главный корпус
PI-диаграмма трубопроводов подпитки теплосети

Стадия	Лист	Листов
Р	2	

PI-диаграмма трубопроводов подпитки теплосети. Система NDK

АКЦИОНЕРНОЕ ОБЩЕСТВО ИНСТИТУТ ТЕПЛОЭЛЕКТРОПРОЕКТ Г. МОСКВА

Согласовано
ОАСУ Соболева
Взам. инв. №
Подпись и дата
Инв. № подл.

Формат А2