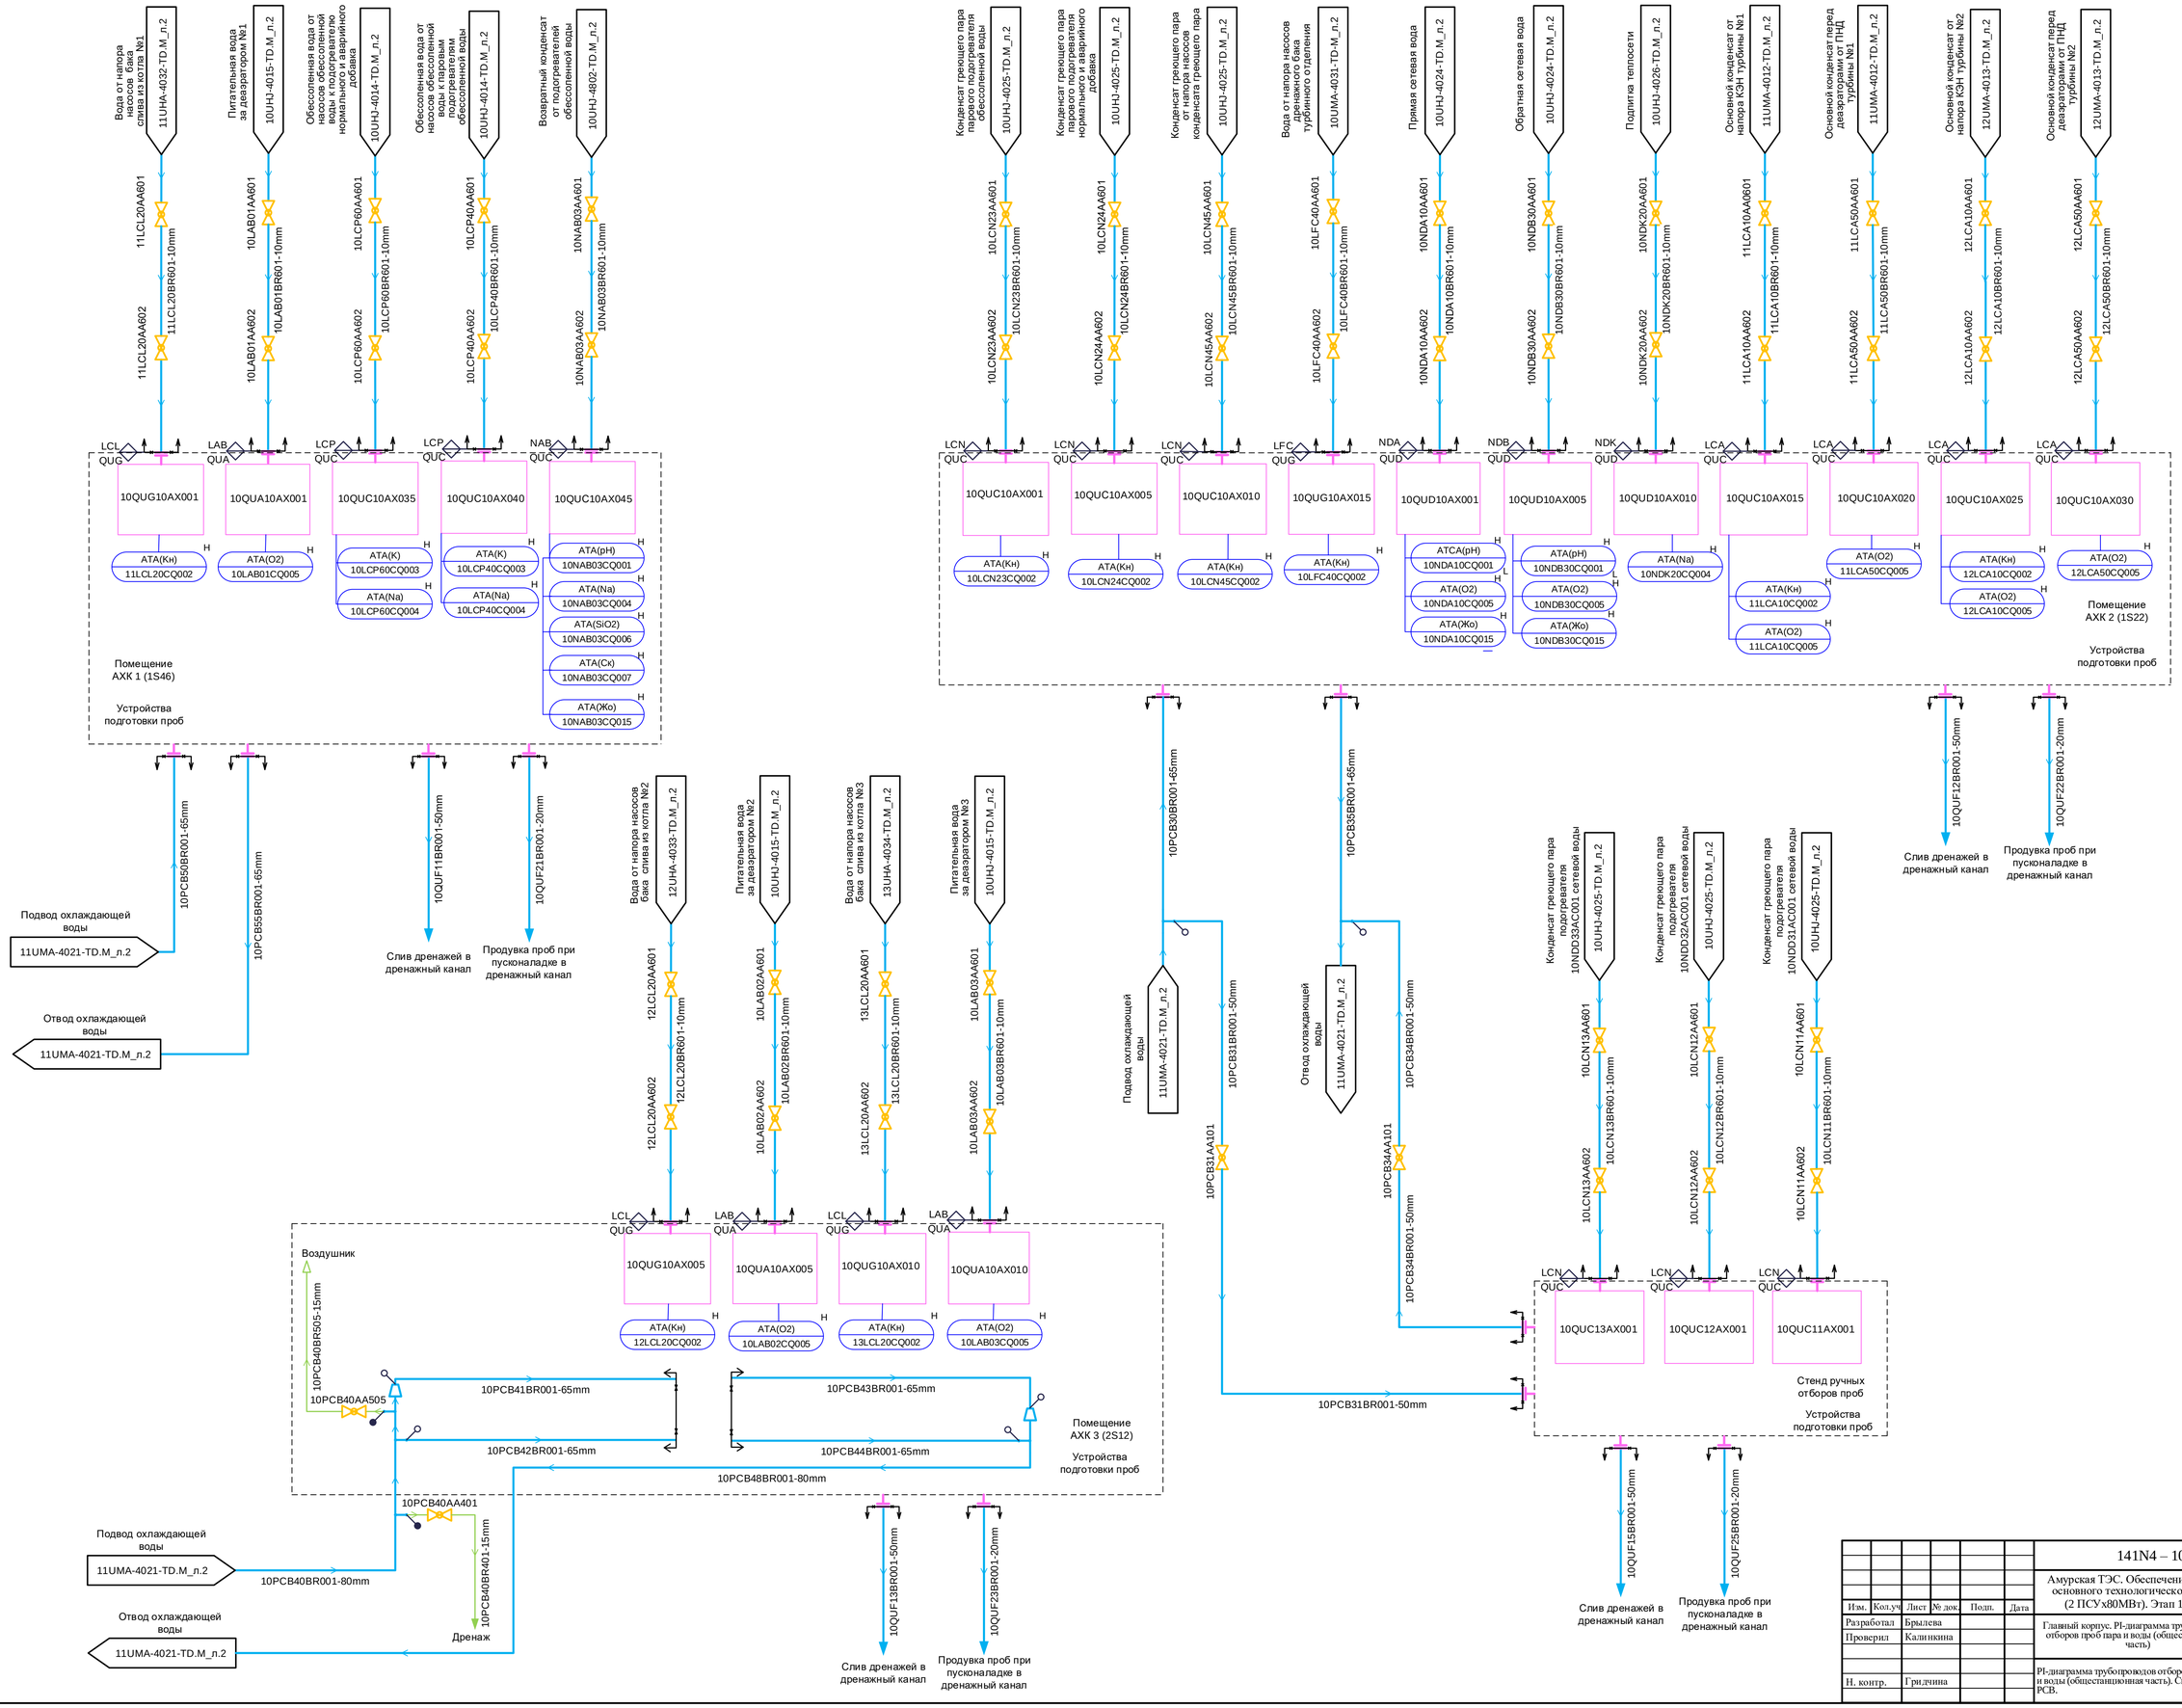

Изм.	Кол.уч	Лист	№ док.	Подп.	Дата	141N4 – 10UHJ – 4027 – TD.M
Разработал		Брылева				Амурская ТЭС. Обеспечение нужд Амурского ГПЗ. Строительство основного технологического комплекса объектов Амурской ТЭС (2 ПСУх80МВт). Этап 1. "Амурская ТЭС (ПСУ-2х80 МВт)"
Проверил		Калинкина				Главный корпус. PI-диаграмма трубопроводов отборов проб пара и воды (общестанционная часть)
Н. контр.		Грядчина				PI-диаграмма трубопроводов отборов проб пара и воды (общестанционная часть). Системы QU, PCB.

Стадия	Лист	Листов
Р	2	

АКЦИОНЕРНОЕ ОБЩЕСТВО ИНСТИТУТ ТЕПЛОЭЛЕКТРОПРОЕКТ г. МОСКВА

Согласовано
ОАСУ Морозова

Взам. инв. №
Подпись и дата
Инв. № подл.

Формат А1