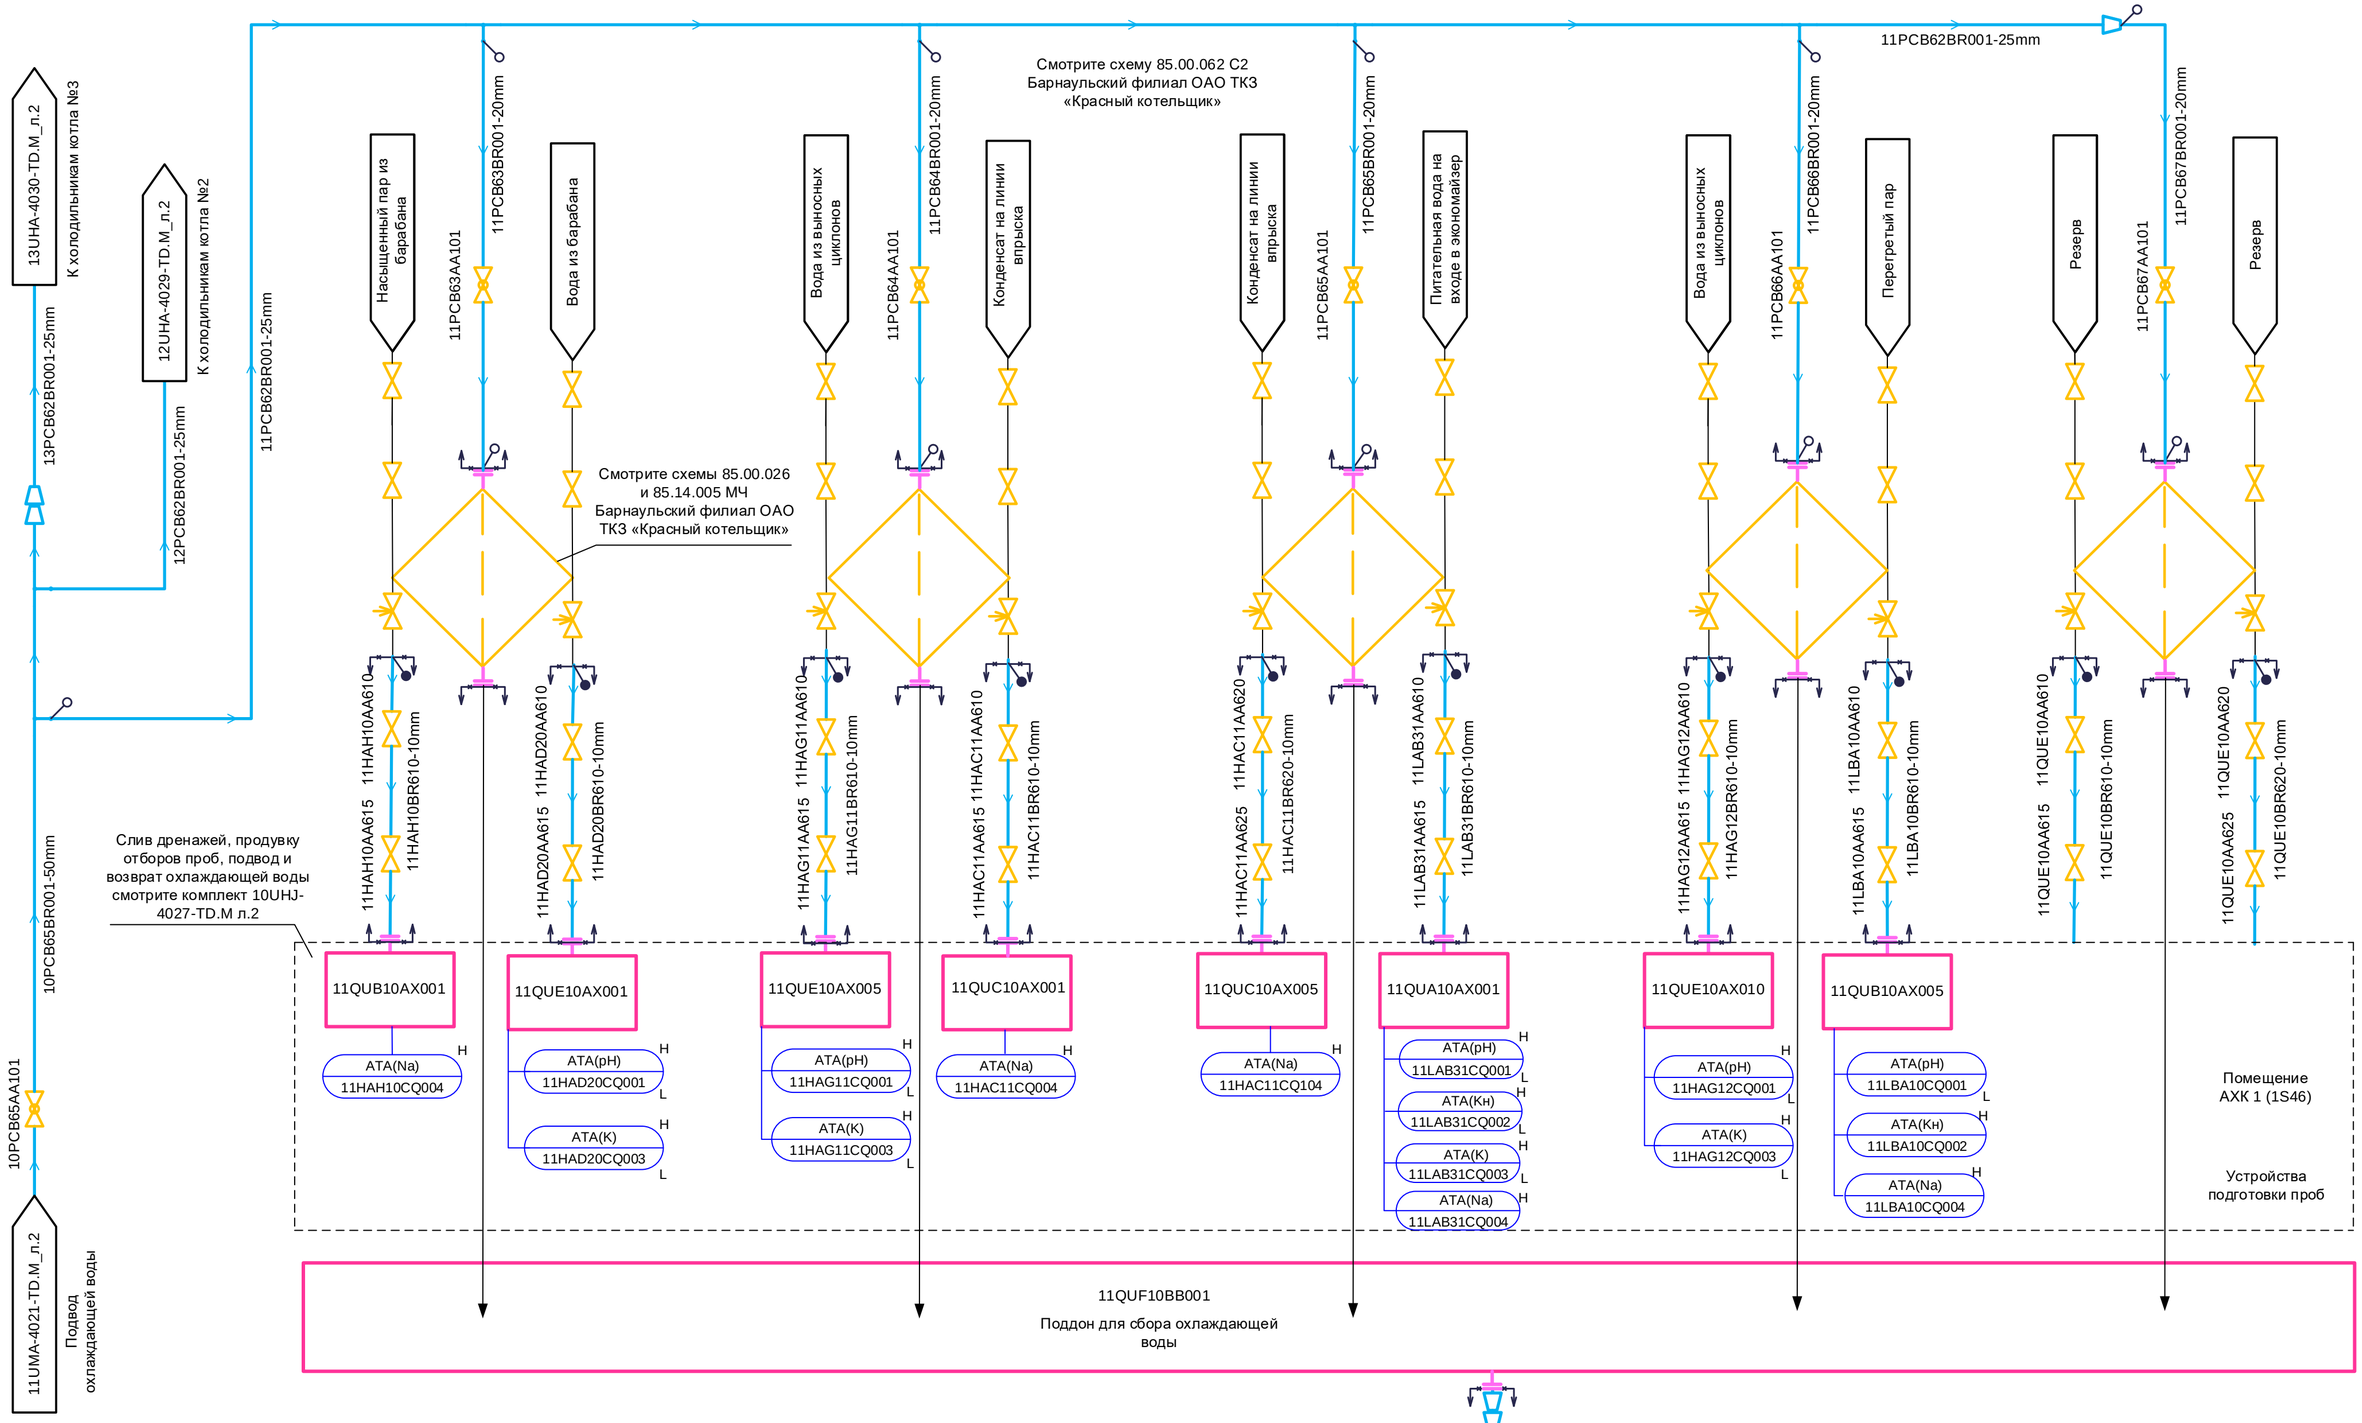

Изм.	Кол.уч	Лист	№ док.	Подп.	Дата
Разработал		Брылева			
Проверил		Калинкина			
Зам.нач.отд.		Майорова			
Н. контр.		Гридчина			

141N4 – 11UHA – 4028 – TD.M

Амурская ТЭС. Обеспечение нужд Амурского ГПЗ. Строительство основного технологического комплекса объектов Амурской ТЭС (2 ПСУх80МВт). Этап 1. “Амурская ТЭС (ПСУ-2х80 МВт)”

Котельное отделение. Паровой котел №1
PI-диаграмма трубопроводов отборов проб пара и воды котла №1

Стадия	Лист	Листов
Р	2	

PI-диаграмма трубопроводов отборов проб пара и воды котла №1. Системы QU, PCB.

АКЦИОНЕРНОЕ ОБЩЕСТВО ИНСТИТУТ ТЕПЛОЭЛЕКТРОПРОЕКТ г. МОСКВА

Согласовано
ОАСУ Морозова

Взам. инв. №
Подпись и дата
Инв. № подл.

Формат А2