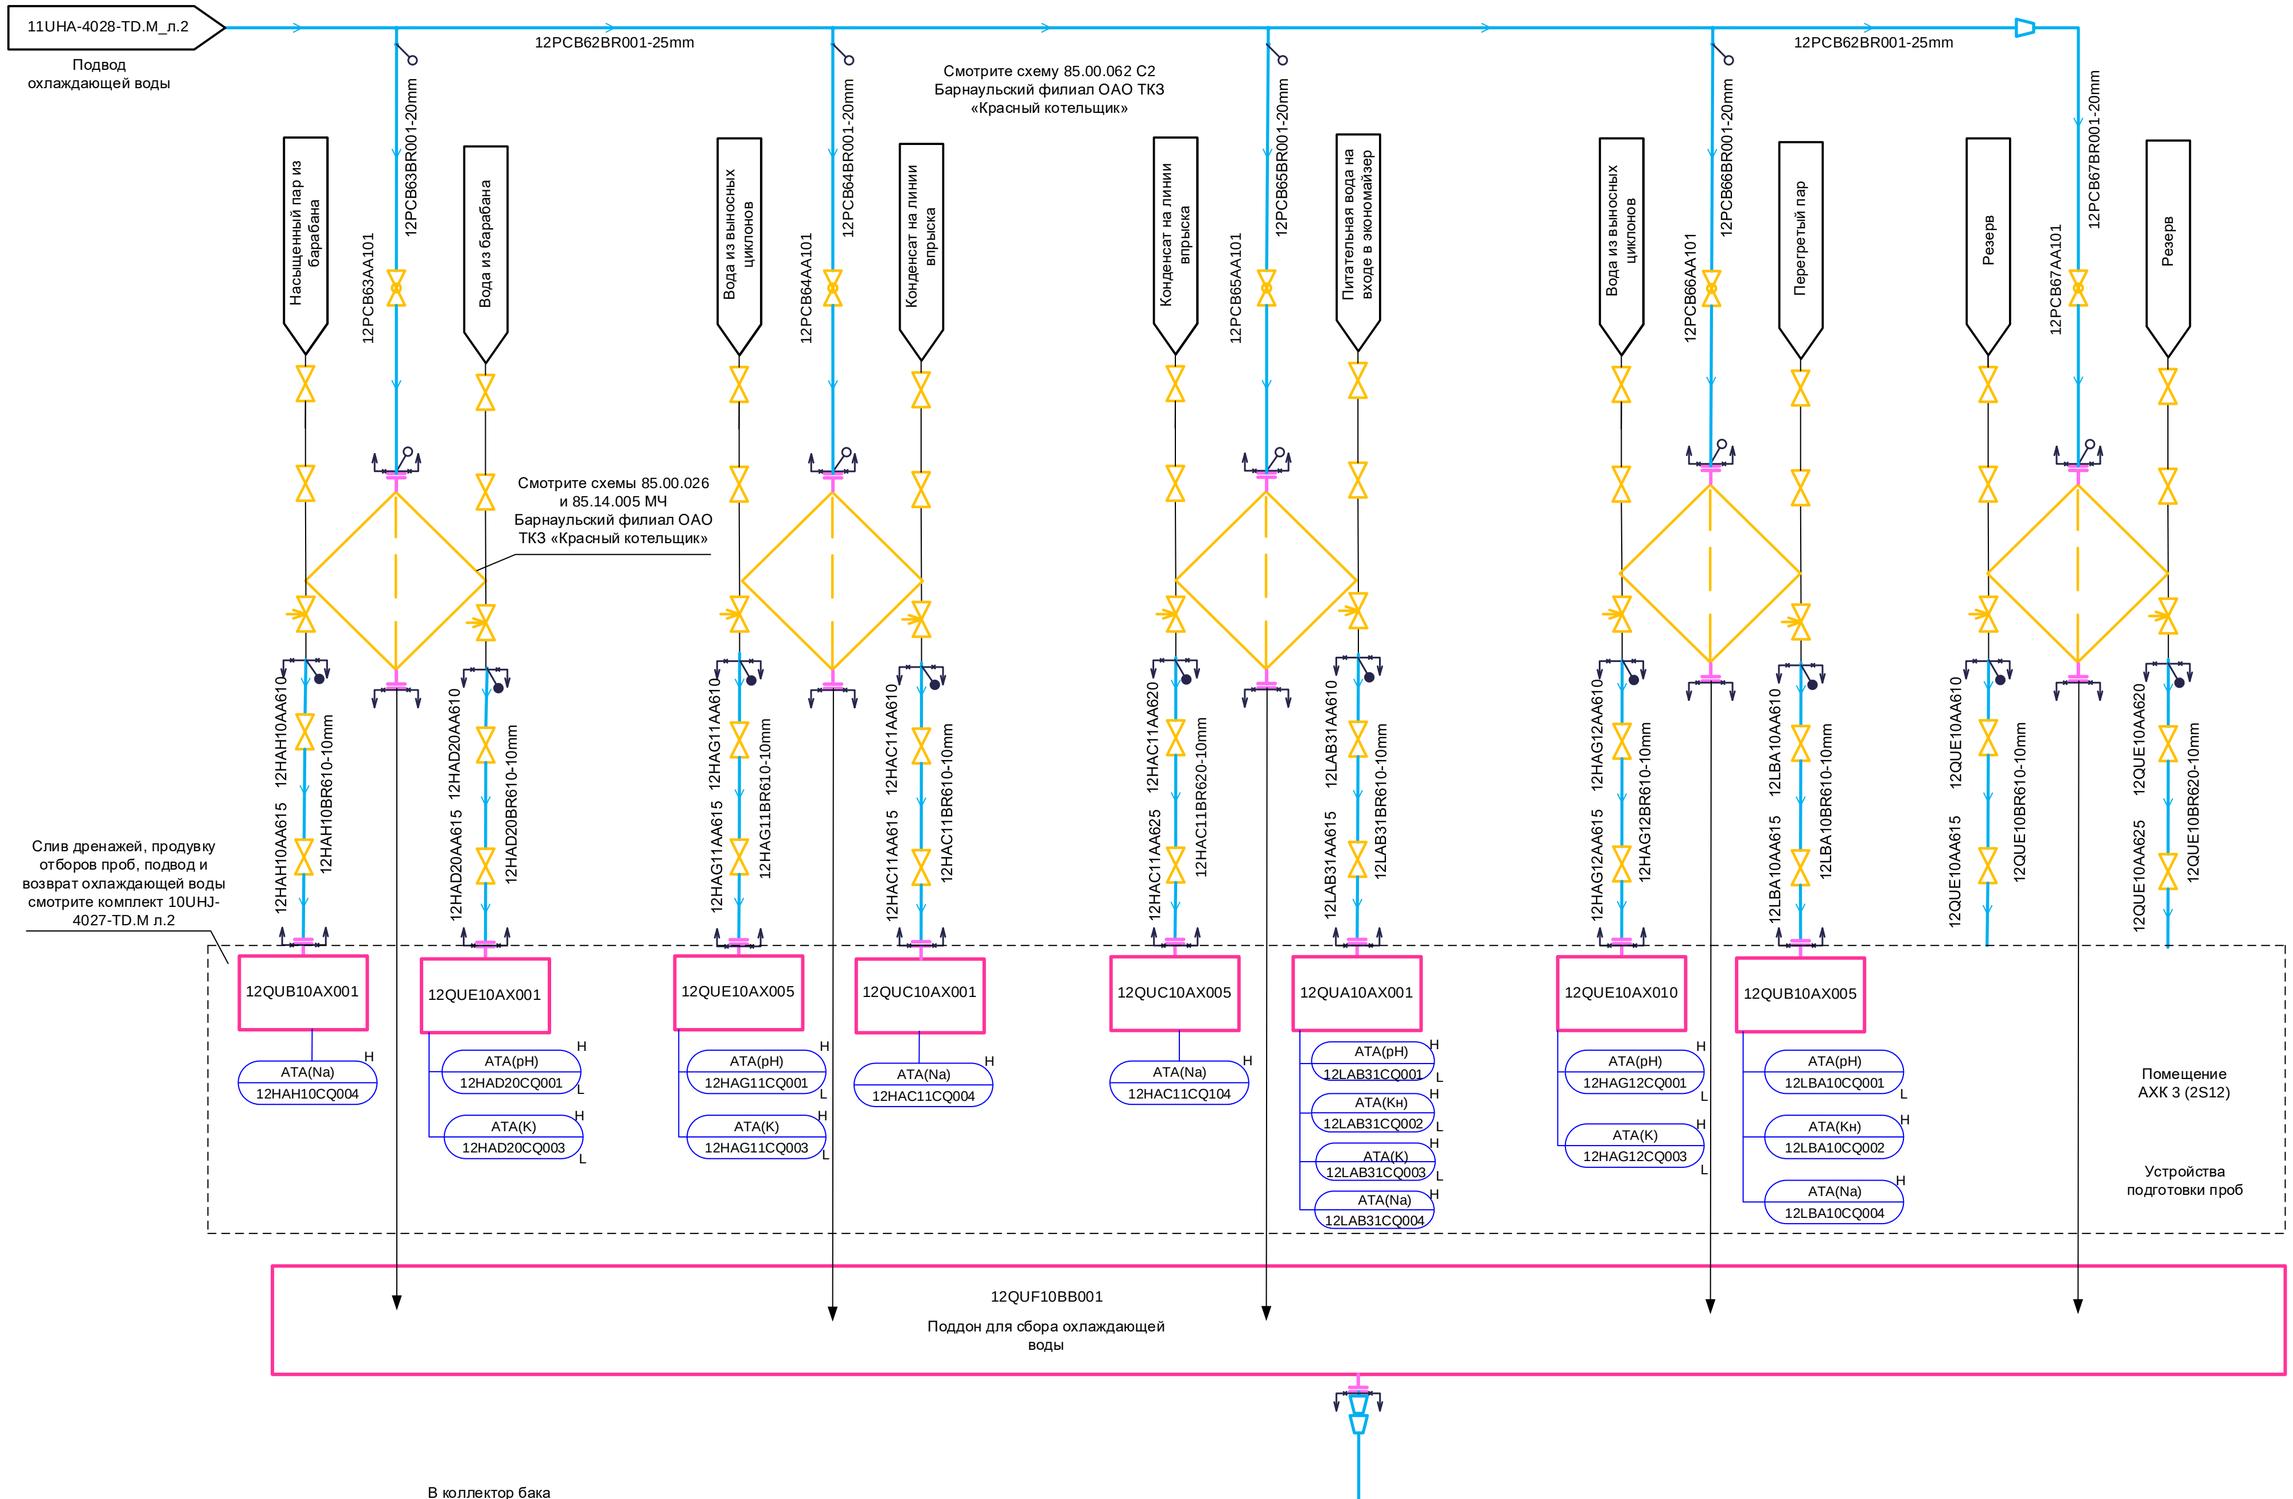

Изм.	Кол.уч	Лист	№ док.	Подп.	Дата	141N4 – 12UHA – 4029 – TD.M
						Амурская ТЭС. Обеспечение нужд Амурского ГПЗ. Строительство основного технологического комплекса объектов Амурской ТЭС (2 ПСУх80МВт). Этап 1. “Амурская ТЭС (ПСУ-2х80 МВт)”
Разработал		Брылева				Котельное отделение. Паровой котел №2 PI-диаграмма трубопроводов отборов проб пара и воды котла №2
Проверил		Калинкина				Стадия: Р; Лист: 2; Листов:
Зам.нач.отд.		Майорова				
Н. контр.		Гридчина				PI-диаграмма трубопроводов отборов проб пара и воды котла №2. Системы QU, PCB.
						АКЦИОНЕРНОЕ ОБЩЕСТВО ИНСТИТУТ ТЕПЛОЭЛЕКТРОПРОЕКТ Г. МОСКВА

Согласовано
ОАСУ Морозова
Взам. инв. №
Подпись и дата
Инв. № подл.

Формат А2